




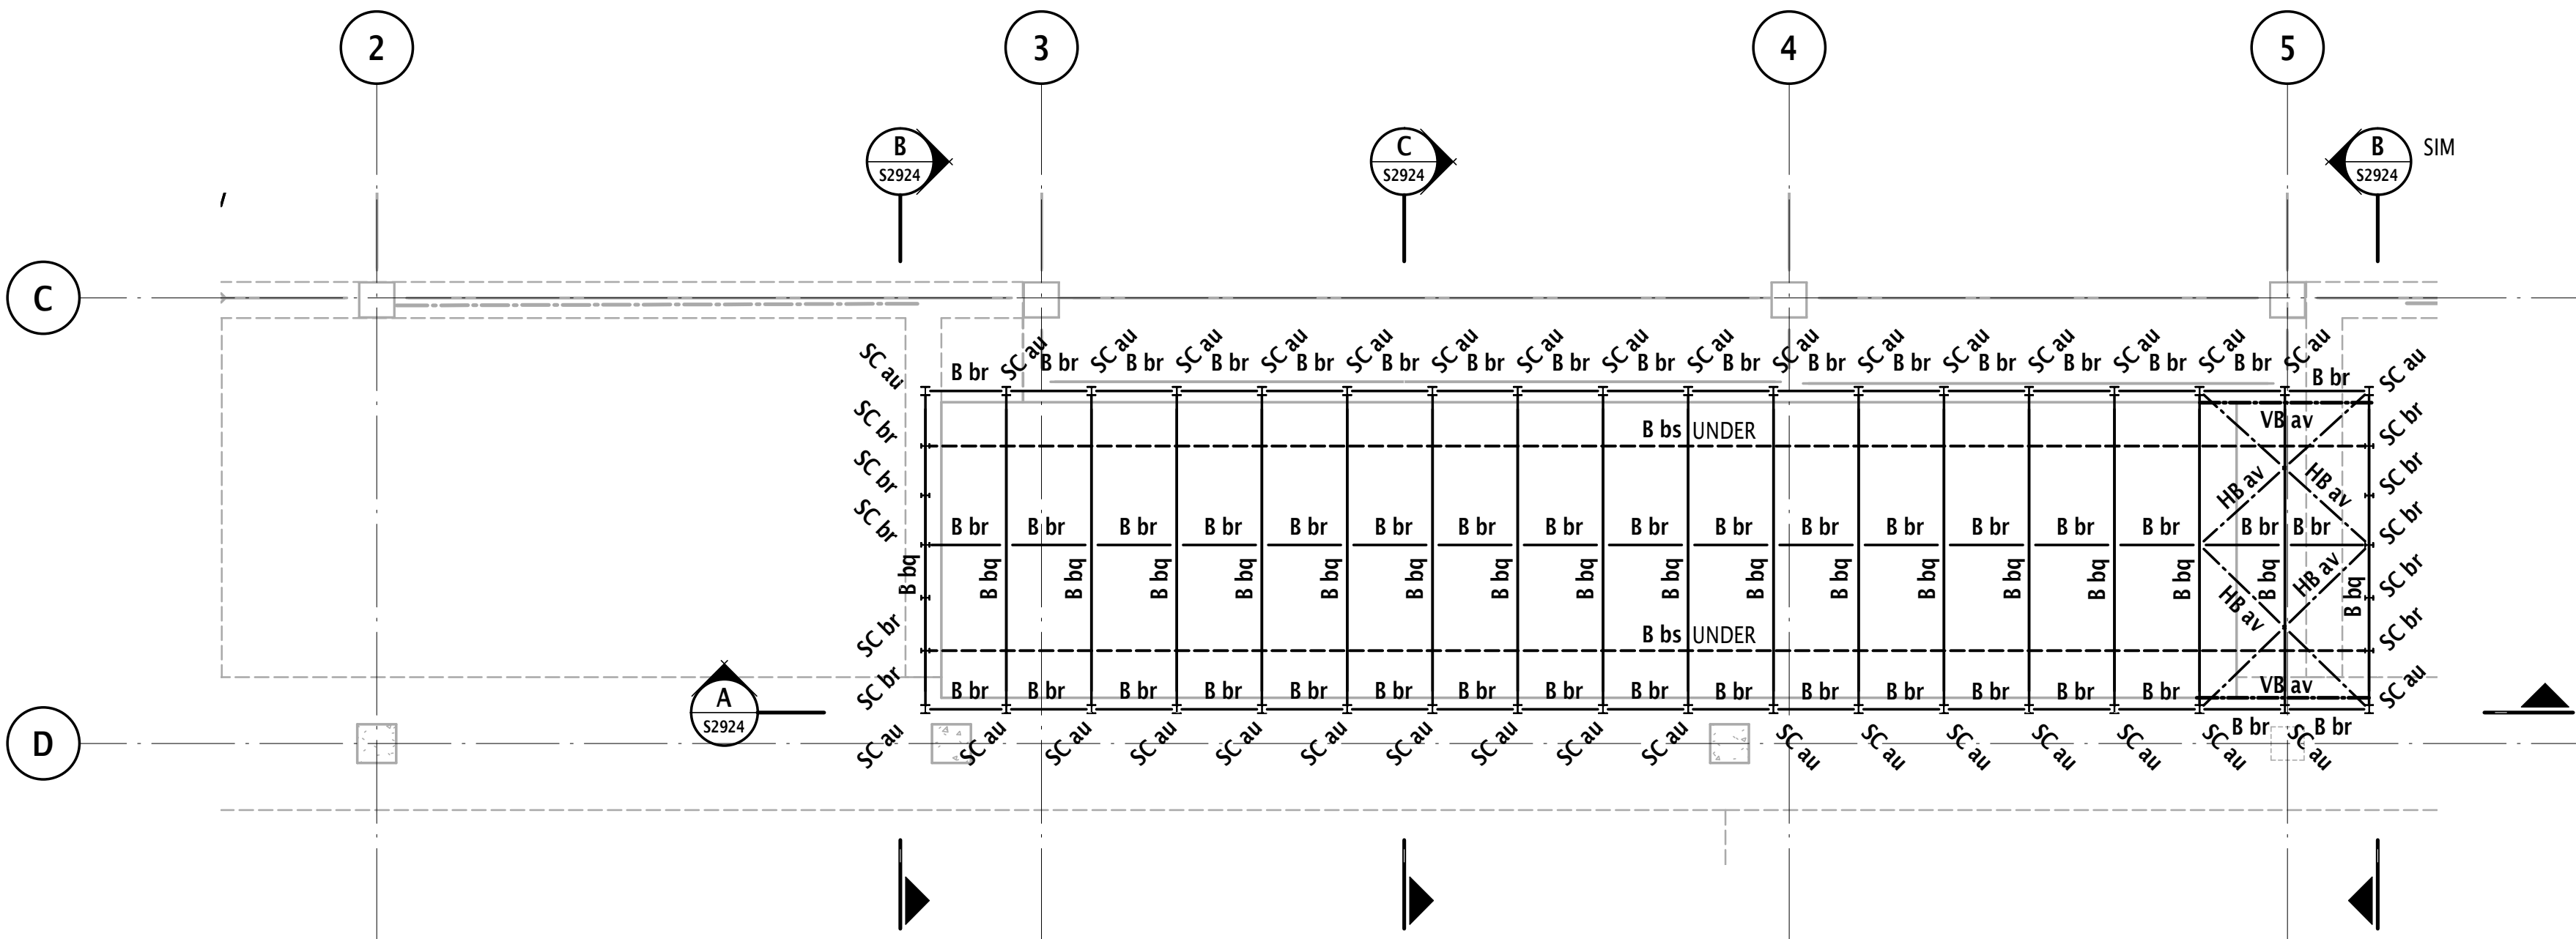


L13 ATRIUM ROOF STEEL FRAMING PLAN
SCALE 1 : 100

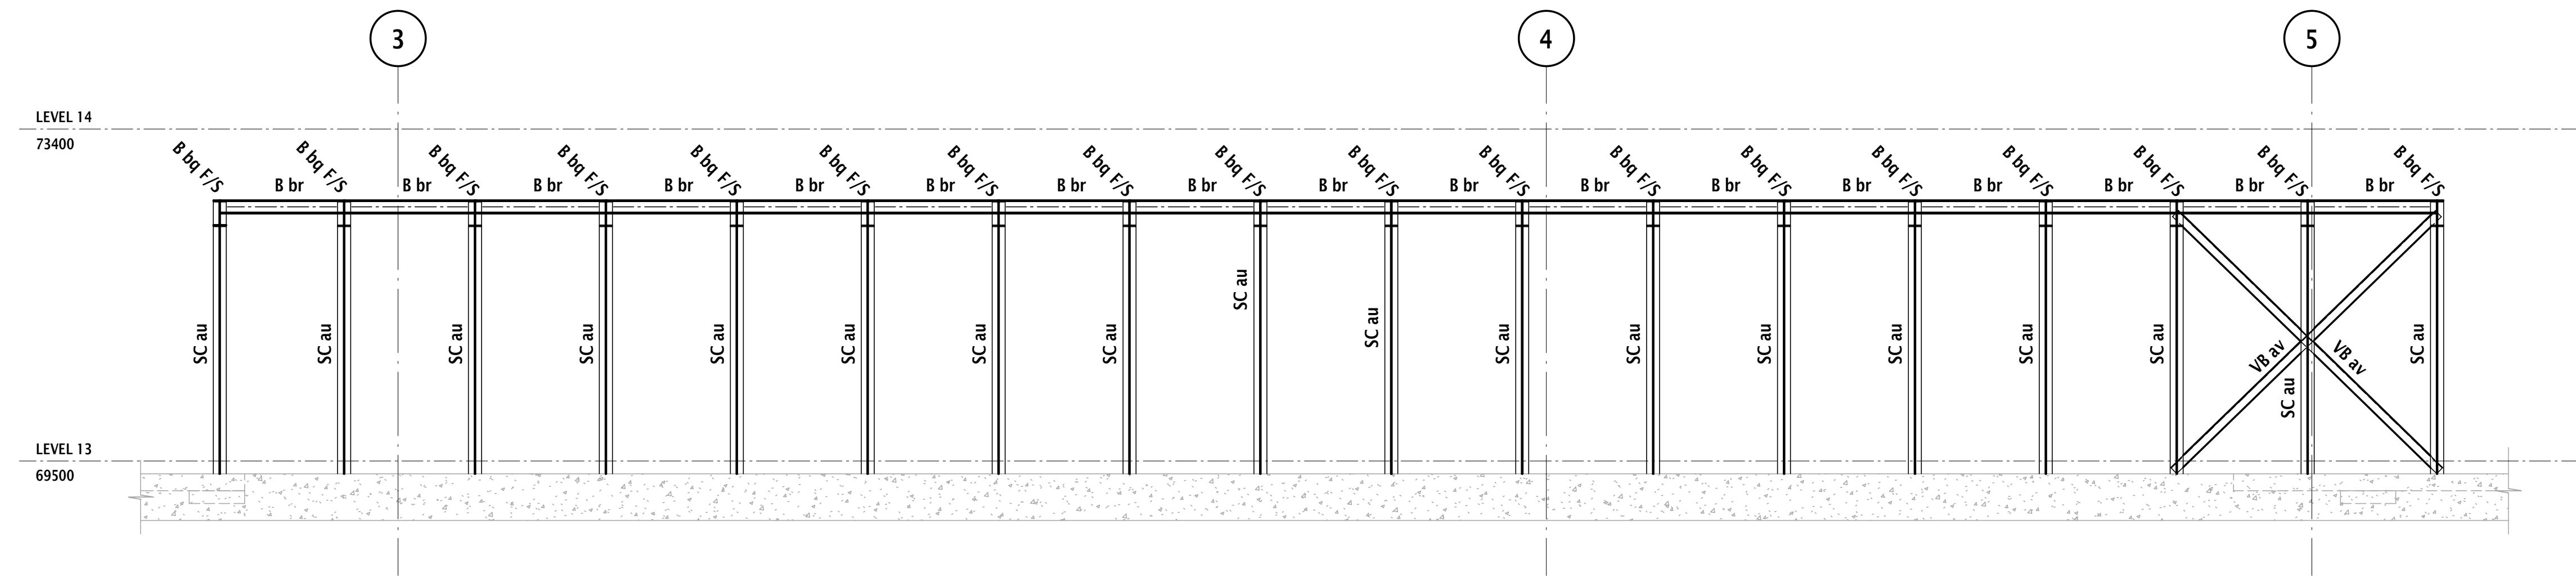


SECTION A
SCALE 1 : 50

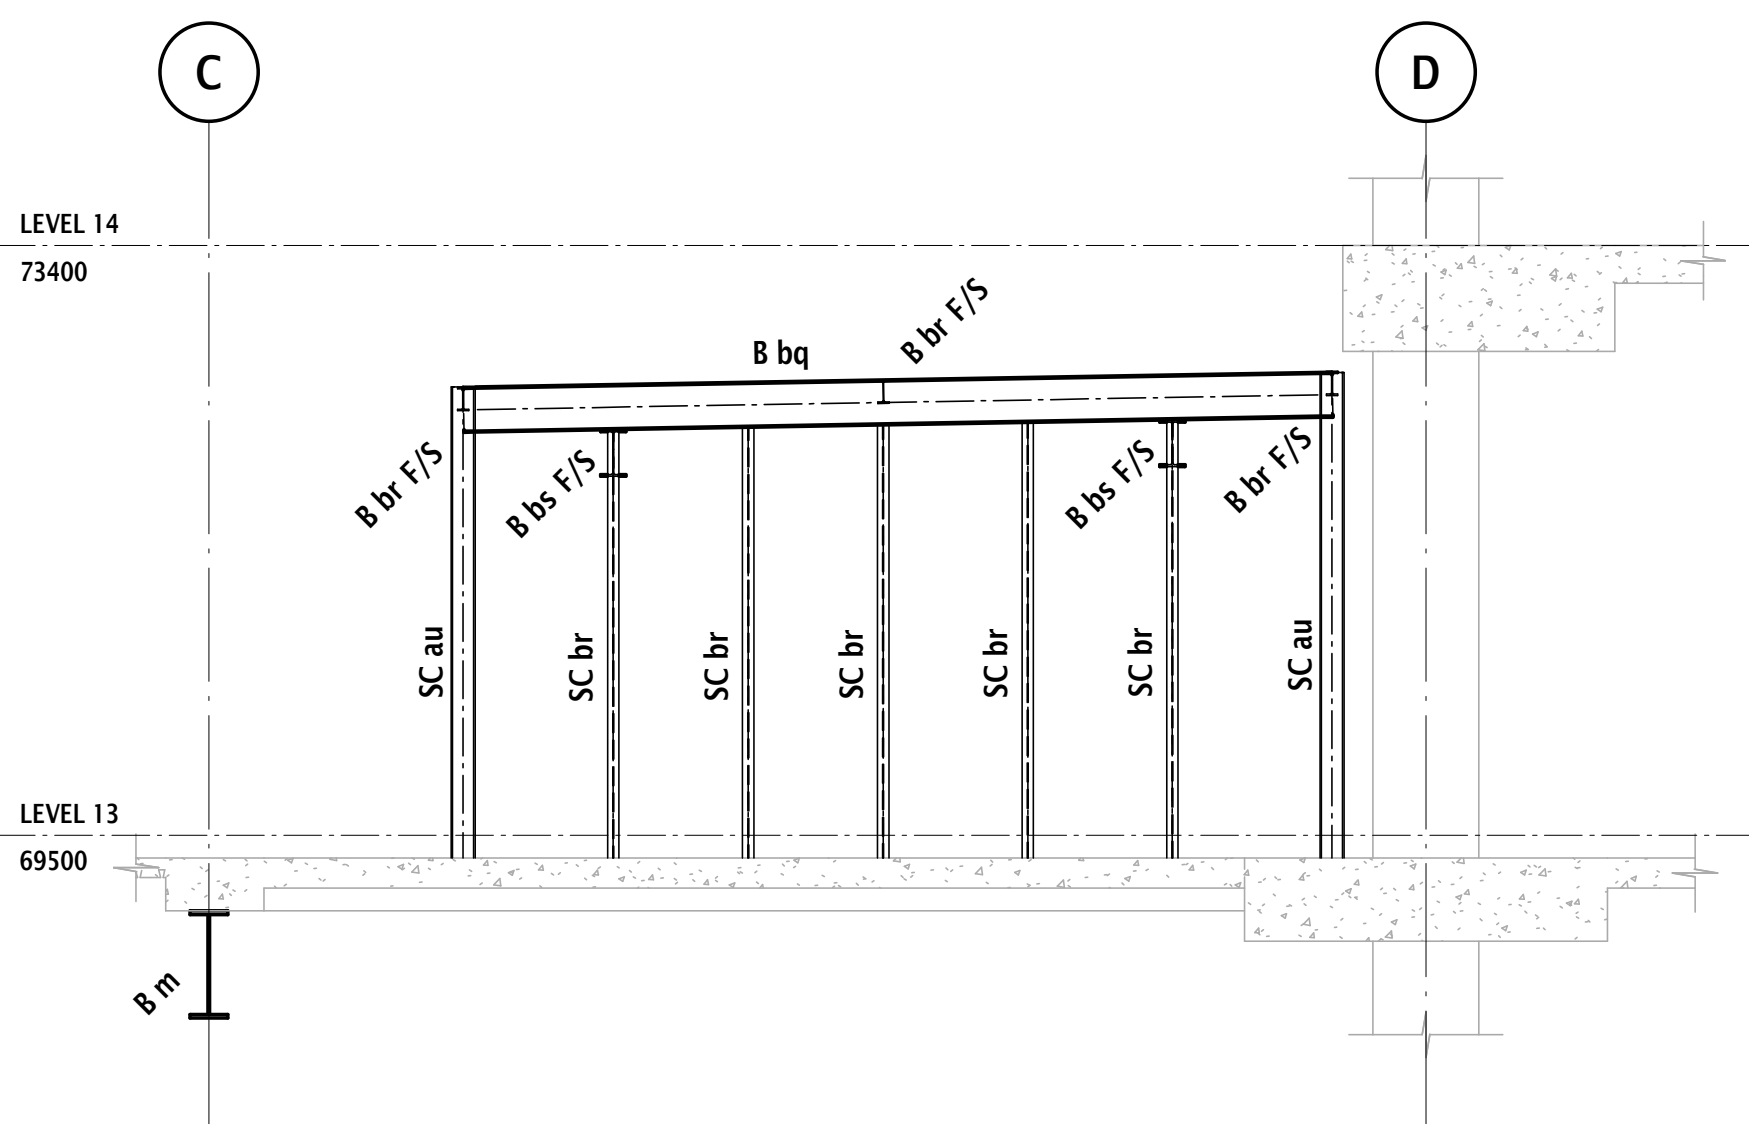

SECTION B
SCALE 1 : 50

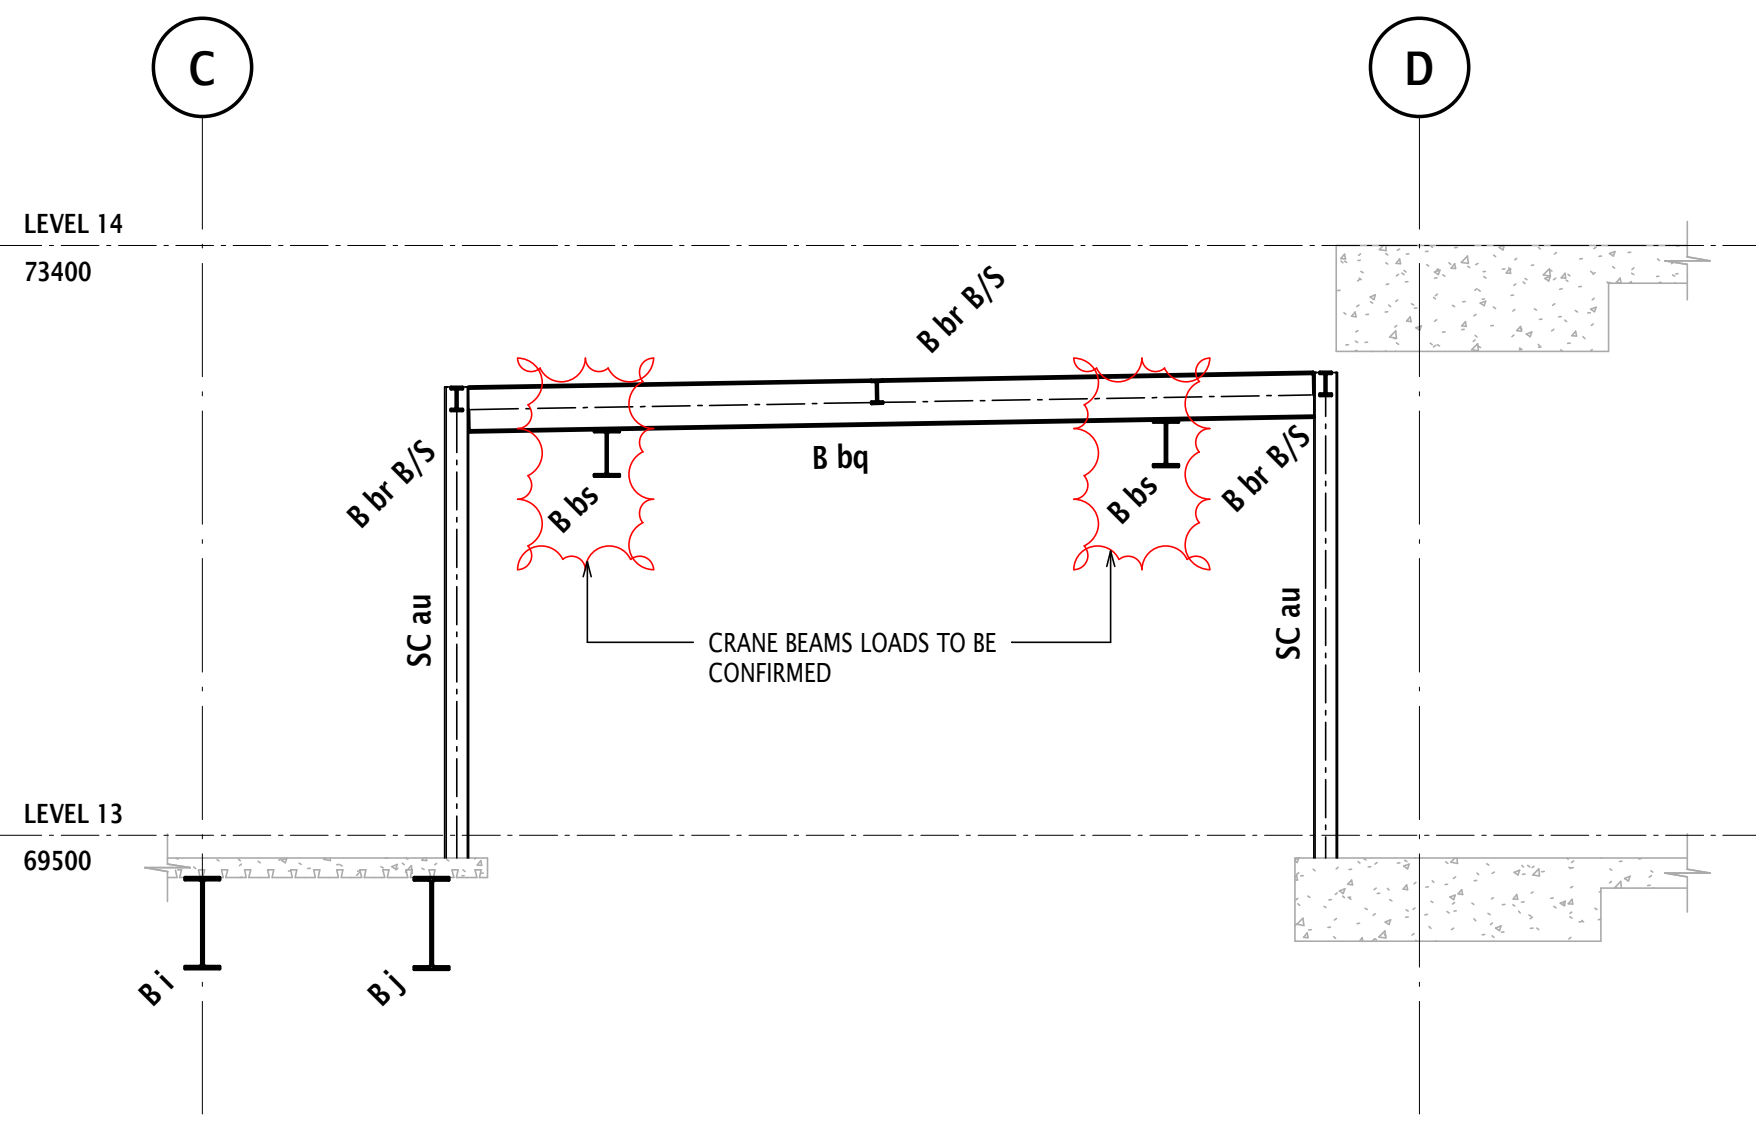

SECTION C
SCALE 1 : 50

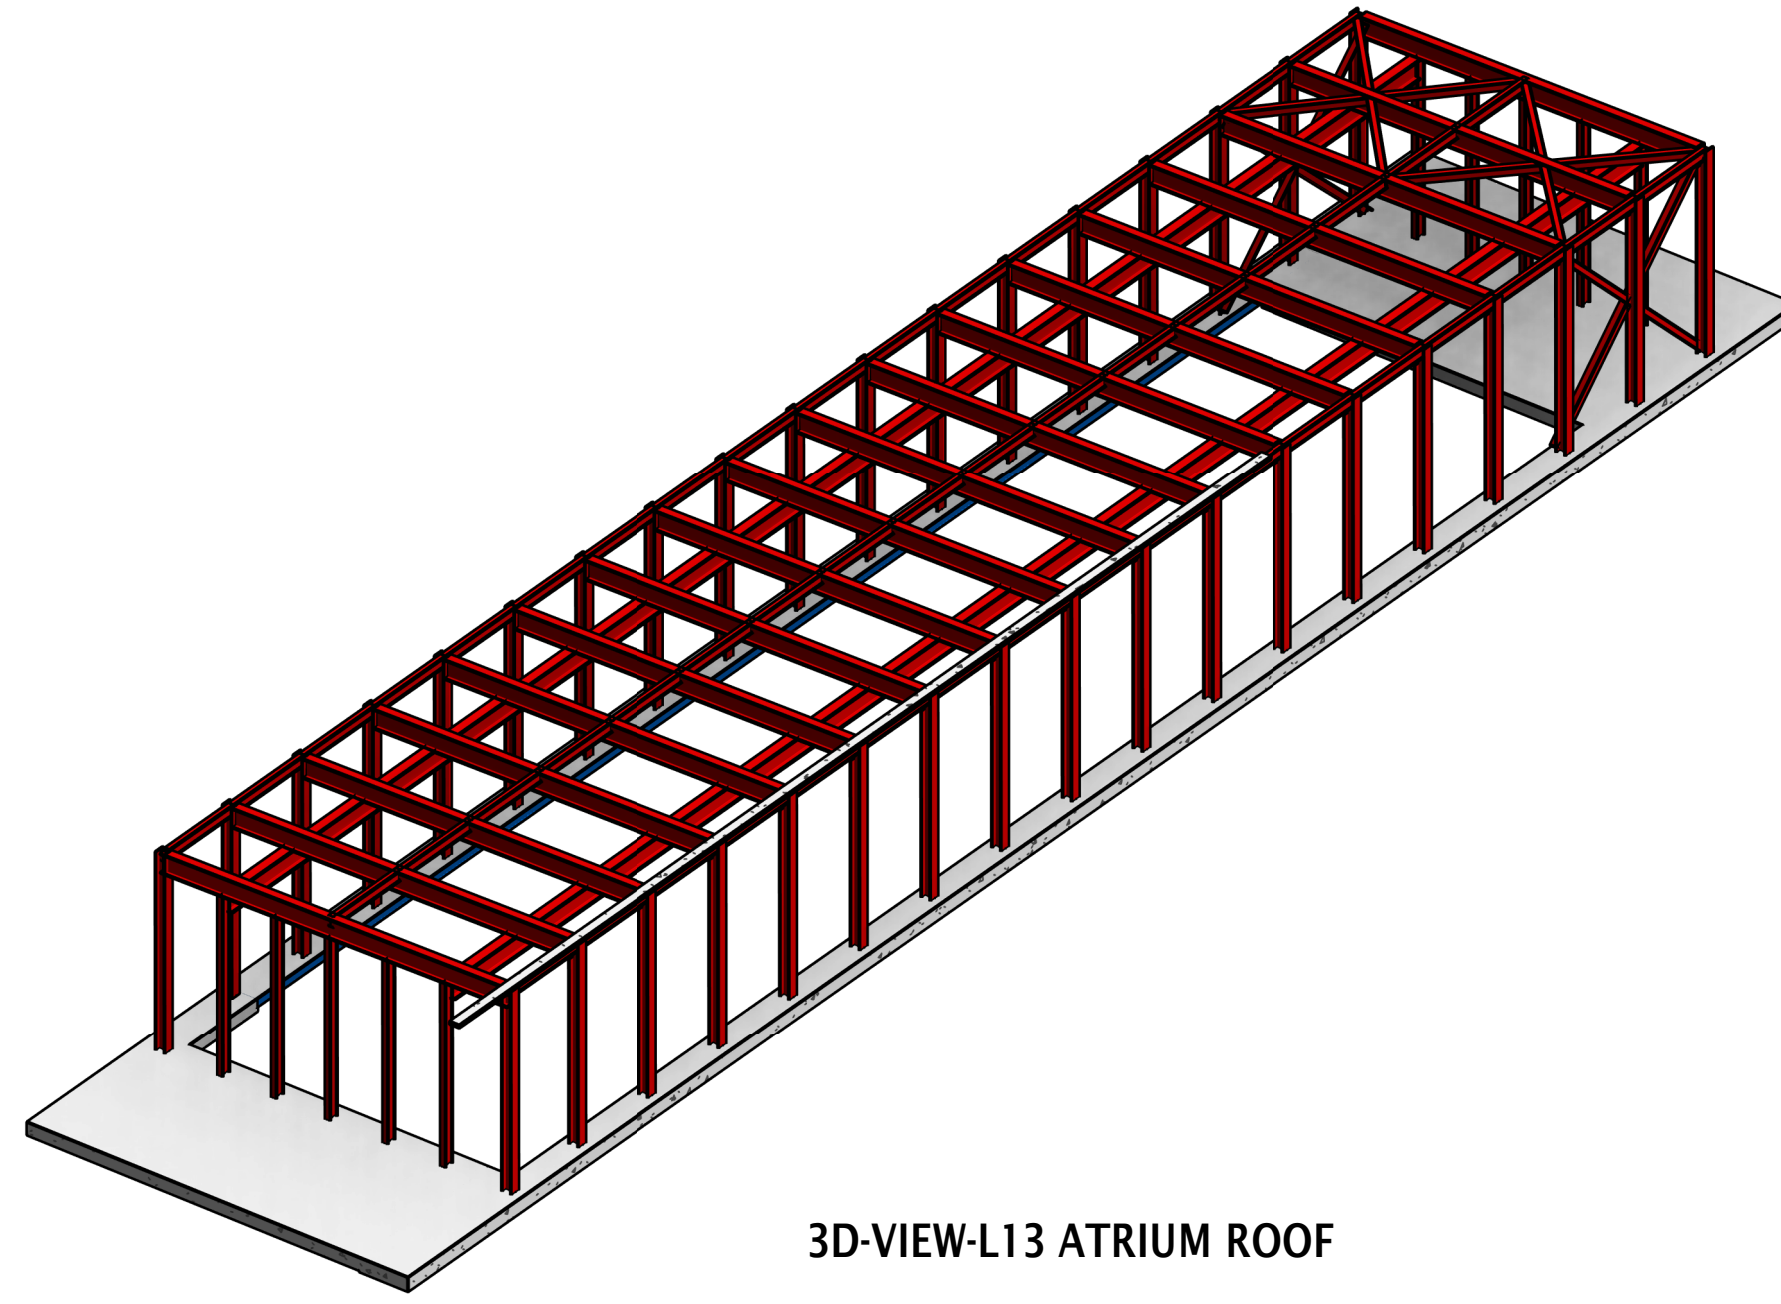

3D-VIEW-L13 ATRIUM ROOF

MEMBER

- B BEAM
- SC STEEL COLUMN
- HB HORIZ. CROSS BRACE
- VB VERT CROSS BRACE

ALL PURLIN AND GIRTS LAPPED WHERE SHOWN

STEELWORK NOTES

1. REFER COVERSHEET DRAWING FOR STEELWORK NOTES.
2. ABBREVIATIONS:-
 - B/S - BOTH SIDES
 - N/S - NEAR SIDE
 - F/S - FAR SIDE
3. ALL STEELWORK TO BE HOT DIPPED GALVANISED.
4. ALL SITE WELDING AREAS TO BE TREATED WITH COLD GALVANISING.

STEELWORK SCHEDULE

MARK	SIZE
a	360 UB 44.7
ab	FBS600x600x25x25
ac	250 UC 73
ad	310 UC 158
ae	310 UC 97
ag	FBS650x650x18x18
ai	FBS600x600x16x16
ak	75x6 EA
an	250x9 SHS
ao	273.1x6.4 CHS
ap	355.6x12.7 CHS
aq	457.0x12.7 CHS
ar	273.1x9.3 CHS
as	273.1x12.7 CHS
at	323.9x12.7 CHS
au	150 UC 30
av	100x8 EA
aw	323.9x9.5 CHS
ax	355.6x 9.5 CHS
ay	FIS900x400x50
b	360 UB 50.7
bc	200x6 SHS
bd	250x150x6.0 RHS
be	150x100x6.0 RHS
bf	150x100x4.0 RHS
bg	410 UB 59
bh	250 UB 26

STEELWORK SCHEDULE

MARK	SIZE
bj	300 PFC
bk	250 PFC
bm	200 PFC
bn	150x6 SHS
bp	250 UC 90
bq	310 UB 32
br	150 UB 18
bs	310 UB 46
bt	250x10 SHS
bu	200x10 SHS
c	410 UB 53.7
ca	250x150x10 RHS
cb	250x150x6.0 RHS
d	460 UB 67.1
e	460 UB 74.6
g	530 UB 82
h	530 UB 92.4
i	610 UB 101
j	610 UB 113
k	610 UB 125
l	700 WB 115
m	700 WB 150
n	700 WB 173
p	800 WB 122
r*	800 WB 192
t*	900 WB 282
u	700 WB 130
v	400 WC 361
w	400 WC 270
x	350 WC 197
z	FBS650x650x28x28


Recent revision history

#	Status	Description	Date
A	CK	DRAFT FOR REVIEW	16.06.21
B	CK	ISSUED FOR TENDER	25.06.21

Disclaimer: Robert Bird Group Pty Ltd ACN 919 380 240 and its related entities (RBG) do not warrant the accuracy, currency or completeness of any information or data they supply or transfer by electronic means. You are responsible for verifying that any information or data supplied or transferred by electronic means matches the information or data on the corresponding PDF or DWG version issued by RBG. RBG will not be liable for any loss or damage you or any other party incur as a result of acting in reliance on any information or data supplied or transferred by electronic means and you release RBG from any liability for any loss or damage however caused which you or any other party may directly or indirectly suffer in connection with your access to or use of that information or data.

RBG provides this information for the express purpose contemplated by the underlying terms of engagement for the project which must not be used for any other purpose. The information is not a contractual document. Unless otherwise agreed in writing by RBG, all intellectual property rights in any information supplied by RBG are owned by or licensed to RBG. RBG only provides you with a non-transferable, fully revocable licence to use the intellectual property rights for the express purpose.

DO NOT SCALE DRAWINGS, USE FIGURED DIMENSIONS
REFER TO GENERAL NOTES UNLESS NOTED OTHERWISE

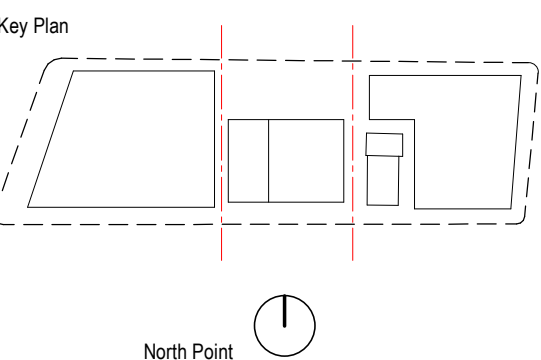

Client

Waterloo Integrated Station Development

A Joint Venture Project

JOHN HOLLAND mirvac

NSW GOVERNMENT | sydney METRO

Consultant

Robert Bird Group

Member of the Surbana Jurong Group

Project
WATERLOO METRO QUARTER DEVELOPMENT
BUILDING 1

Project number	18445B	Designer	RK	Size check	25mm
Checked	GA	Approved	GA	Sheet size	A1
				Scale	1:50, 1:100

Sheet title
L13 ATRIUM STEEL FRAMING PLAN

Status
NOT FOR CONSTRUCTION

Sheet number
WMQ-BLD1-RBG-ST-DRG-S2924 B

Revision