



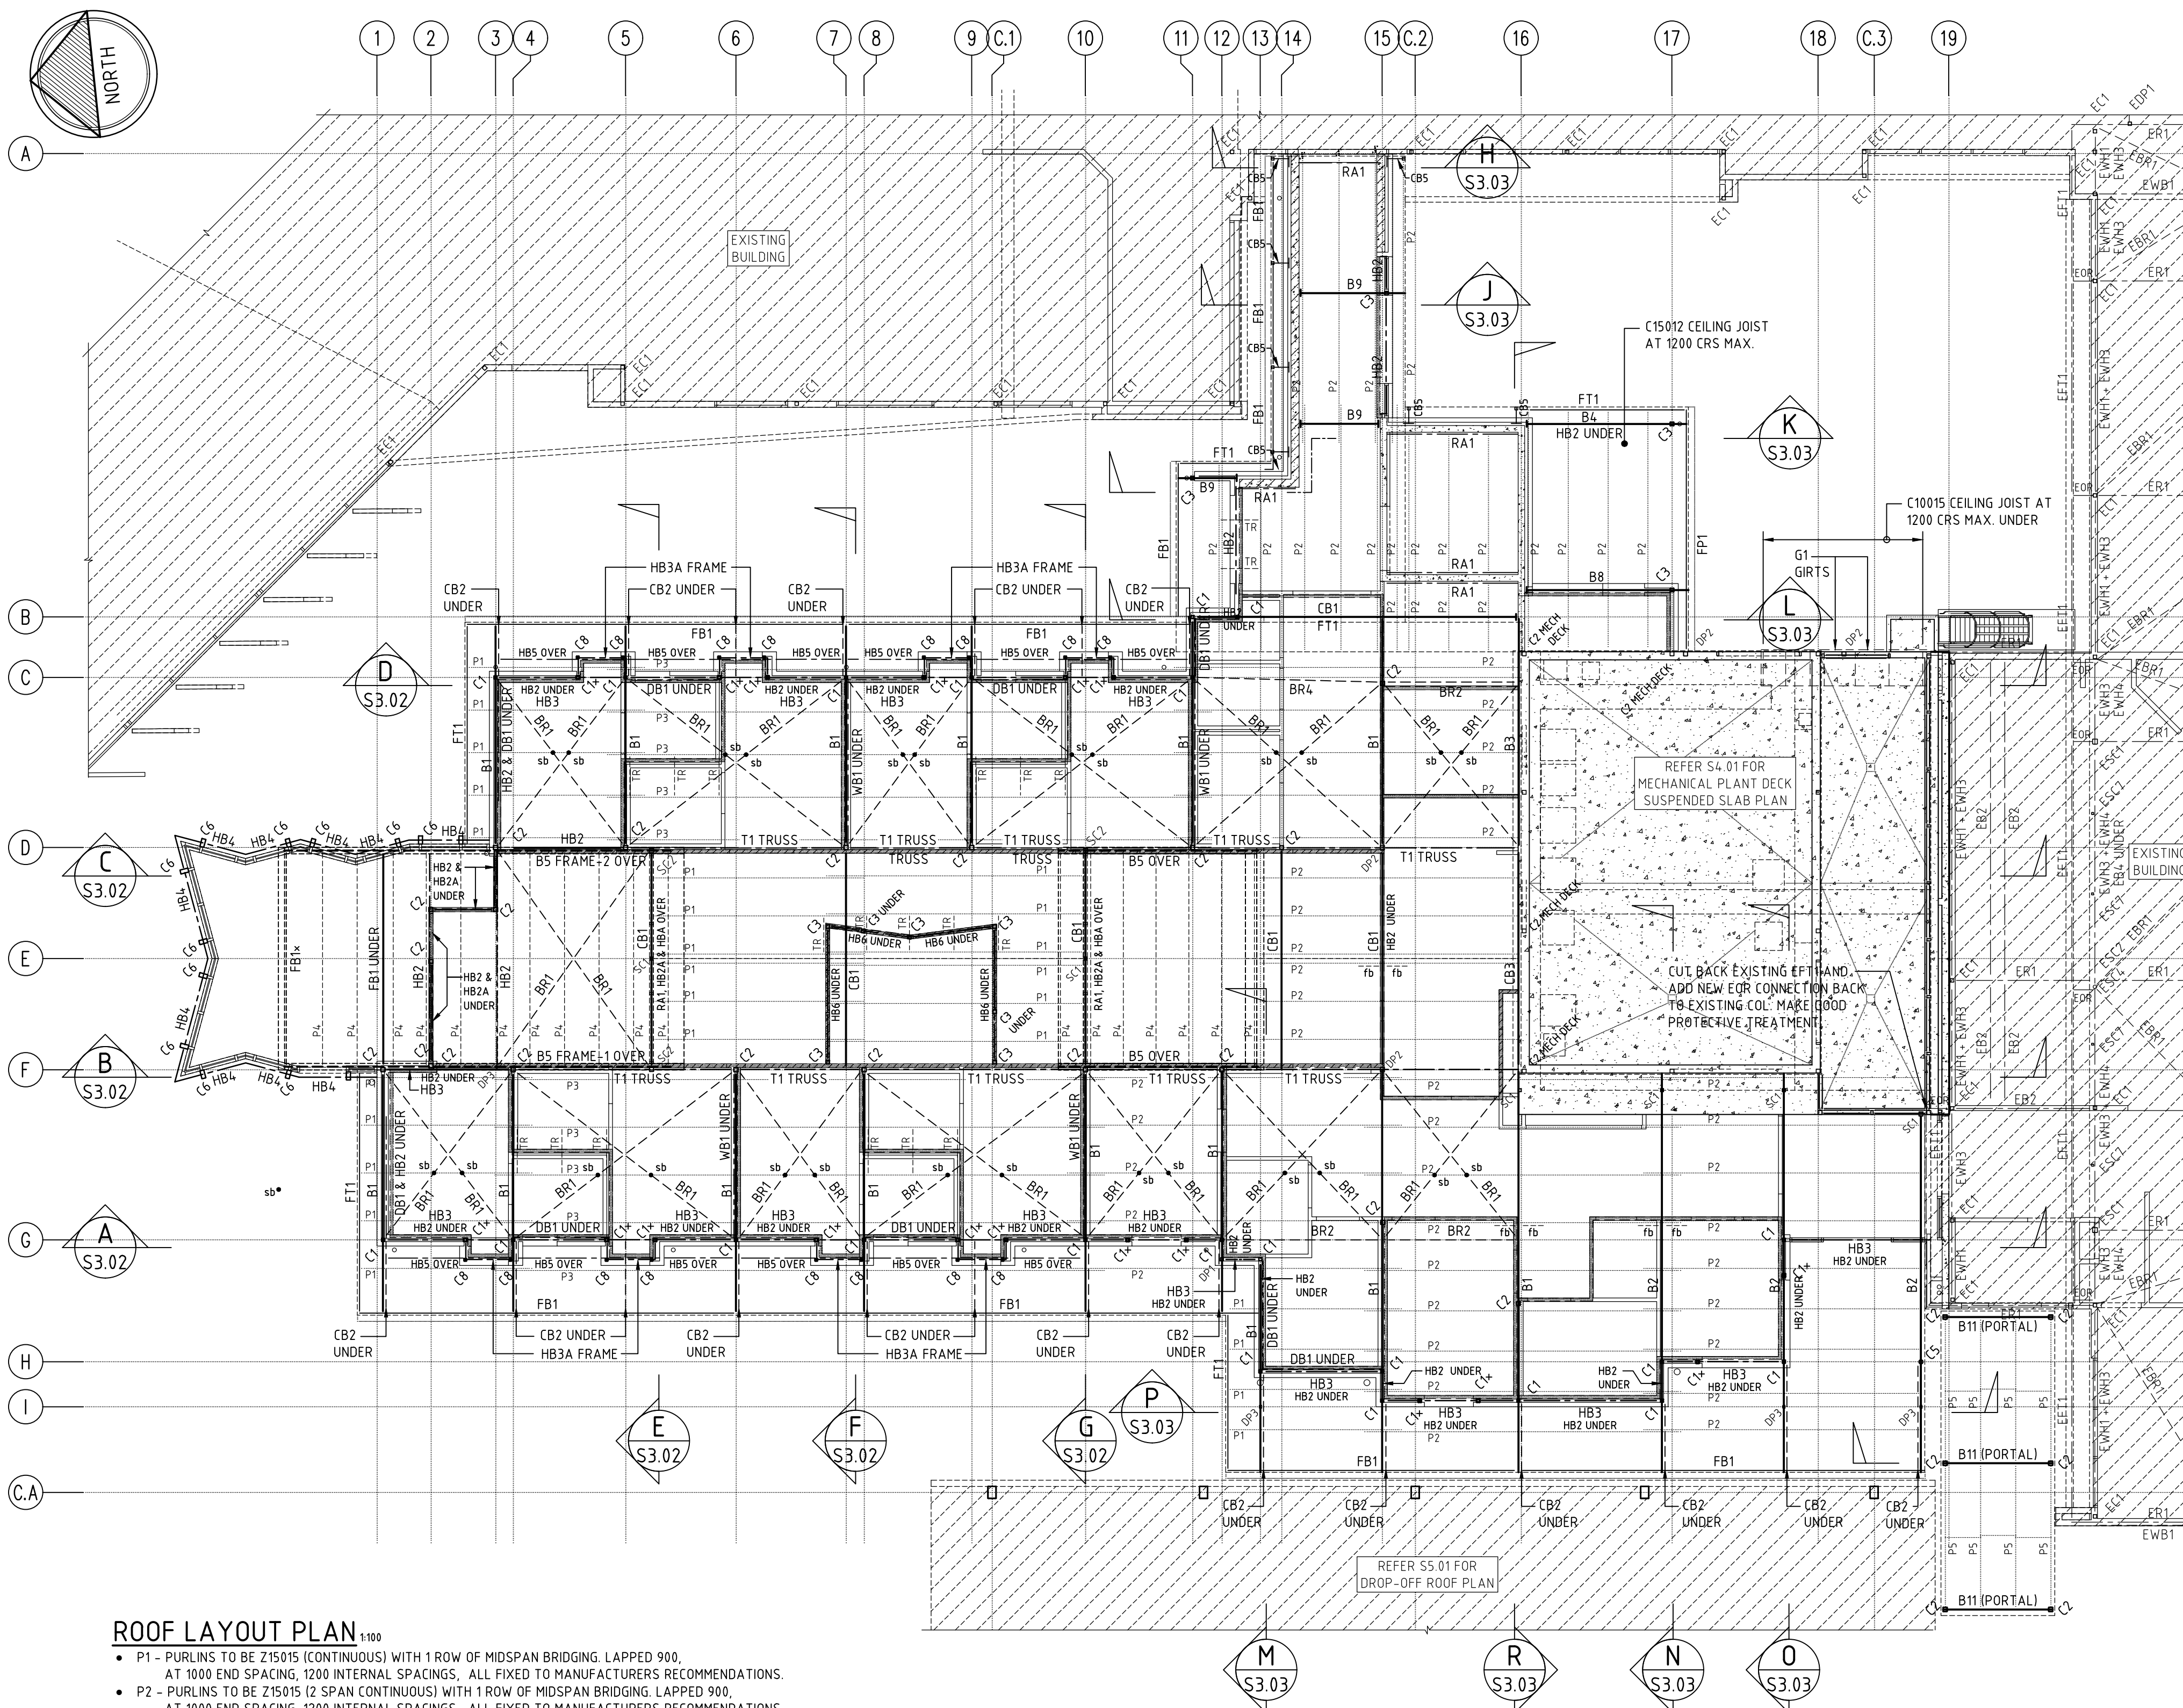


ROOF LAYOUT PLAN 1:100


- P1 - PURLINS TO BE Z15015 (CONTINUOUS) WITH 1 ROW OF MIDSPAN BRIDGING. LAPPED 900, AT 1000 END SPACING, 1200 INTERNAL SPACINGS, ALL FIXED TO MANUFACTURERS RECOMMENDATIONS.
- P2 - PURLINS TO BE Z15015 (2 SPAN CONTINUOUS) WITH 1 ROW OF MIDSPAN BRIDGING. LAPPED 900, AT 1000 END SPACING, 1200 INTERNAL SPACINGS, ALL FIXED TO MANUFACTURERS RECOMMENDATIONS.
- P3 - PURLINS TO BE Z15015 (3 SPAN CONTINUOUS) WITH 1 ROW OF MIDSPAN BRIDGING. LAPPED 900, AT 1000 END SPACING, 1200 INTERNAL SPACINGS, ALL FIXED TO MANUFACTURERS RECOMMENDATIONS.
- P4 - PURLINS TO BE C15024 SINGLE SPAN, SIMPLY SUPPORTED WITH 2 ROWS OF MIDSPAN BRIDGING AT 900 SPACING. ALL FIXED TO MANUFACTURERS RECOMMENDATIONS.
- P5 - PURLINS TO BE C10015 SINGLE SPAN, SIMPLY SUPPORTED WITH 1 ROW OF MIDSPAN BRIDGING AT 900 SPACING. ALL FIXED TO MANUFACTURERS RECOMMENDATIONS.
- G1 - GIRTS TO BE C10015 SINGLE SPAN, SIMPLY SUPPORTED AT 600 SPACING. ALL FIXED TO MANUFACTURERS RECOMMENDATIONS.
- TR - PURLIN TRIMMER C15019 FIXED TO PURLINS (1200 CRS MAX.) VIA GENERAL PURPOSE BRACKET ALL TO MANUFACTURERS RECOMMENDATIONS.
- sb - DENOTES ANTI-SAG HOOK BOLT (GALVANISED) AT MID-SPAN (OR NEAR) OF ALL ROOF BRACING MEMBERS. CONNECT TO THE WEB OF THE PURLIN OR BRIDGING MEMBER ABOVE AS APPROPRIATE.
- fb - DENOTES FLY BRACING - REFER THIS SHEET FOR DETAILS.

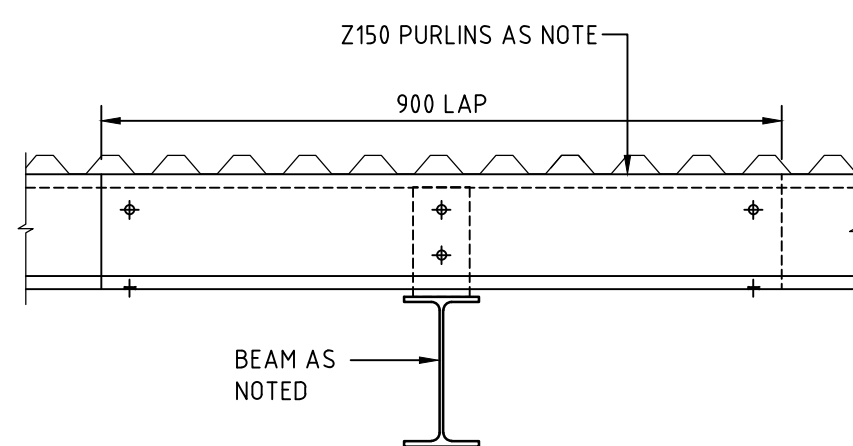


TYPICAL PURLIN LAP DETAIL 1:10

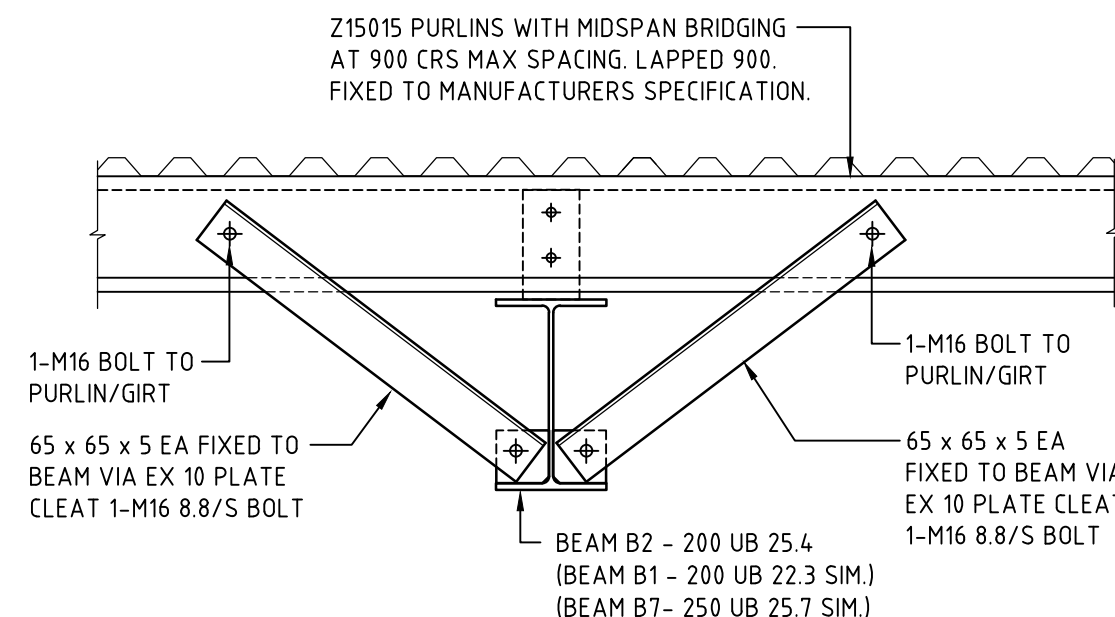

TYPICAL FLY BRACE DETAIL (fb) 1:10
PURLIN LAP FIXING OMITTED FOR CLARITY

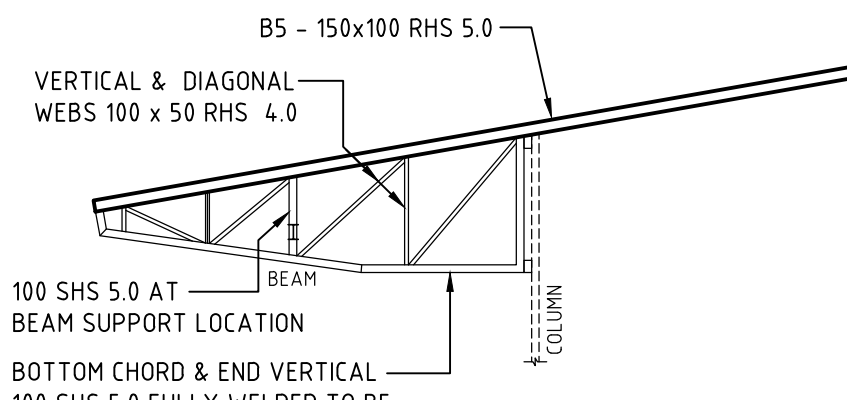

B5 FRAME-1 ELEVATION 1:50
FULLY WELDED FRAME

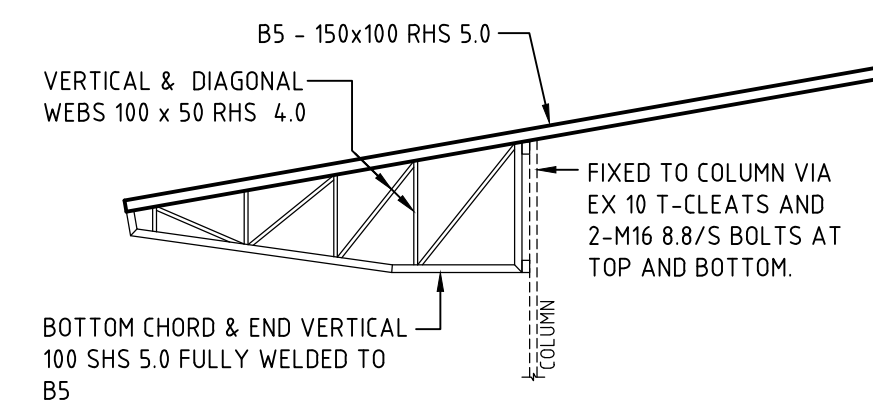


B5 FRAME-2 ELEVATION 1:50
FULLY WELDED FRAME

MEMBER SCHEDULE


ITEM	MEMBER
EC	EXISTING COLUMN
EC1	89 SHS 5.0 EXISTING COLUMN
EC2	5/ 102 CHS 4.0 EXISTING COLUMN
EC3	140 CHS 3.5/48 CHS 3.2 EXISTING COLUMN
ESC1	89 SHS 5.0 EXISTING STUB
ESC2	125 SHS 6.0 EXISTING STUB
ESC4	89 CHS 4.9 EXISTING STUB
ESC6	250 UB 26 EXISTING STUB
ESC7	50 SHS 3.0 EXISTING STUB
EDP1	89 SHS 5.0 EXISTING DROPPER
EDP2	140 CHS 3.5 / 48 CHS 3.2 EXISTING DROPPER
EB2	310 UB 40 EXISTING BEAM
EB4	440 UB 67 EXISTING BEAM
ER1	200 UB 18 EXISTING RAFTER
EBR1	150C24 EXISTING BRACE
EW1	125 PFC EXISTING WINDOW HEAD
EW3	150 PFC EXISTING WINDOW HEAD
EW4	150C6 EXISTING WINDOW HEAD
EOR	100 PFC EXISTING OUTRIGGER
EFT1	EXISTING FASCIA TRUSS

MEMBER SCHEDULE


ITEM	MEMBER
CC1	600 x 300 CONCRETE COLUMN
CC2	450 x 300 CONCRETE COLUMN
C1	75 SHS 5.0
C14	75 SHS 5.0 CAVITY COLUMN TO U/S OF BEAM
C2	100 SHS 5.0
C3	89 SHS 5.0
C4	250 x 200 RHS 6.0
C5	101.6 CHS
C6	200 x 100 RHS 6.0
C7	100 x 50 RHS 4.0
C8	50 SHS 5.0
SC1	75 SHS 5.0 STUB COLUMN
SC2	100 SHS 5.0
DP1	75 SHS 4.0 DROPPER
DP2	100 SHS 5.0
DP3	75 x 50 RHS 4.0 DROPPER
B1	200 UB 22.3
B2	200 UB 25.4
B3	200 PFC
B4	180 PFC
B5	150 x 100 RHS 4.0
B6	410 UB 59.7
B7	250 UB 25.7
B8	150 PFC
B9	89 SHS 5.0
B10	180 UB 18.1
B11	100 SHS 5.0
CB1	200 UB 22.3 CRANKED BEAM
CB2	100 x 50 RHS 4.0 CRANKED BEAM
CB3	180 PFC CRANKED BEAM
CB4	150 x 50 RHS 4.0 CRANK BEAM
CB5	75 SHS 3.0 CRANK BEAM
HB1	180 PFC HEAD BEAM
HB2	150 x 100 RHS 5.0 HEAD BEAM
HB2A	150 x 100 RHS 5.0 HEAD BEAM
HB3	125 x 75 RHS 4.0 HEAD BEAM
HB3A	125 x 75 RHS 4.0 HEAD BEAM
HB4	200 x 100 RHS 4.0 HEAD BEAM
HB5	150 x 100 RHS 4.0 HEAD BEAM
HB6	89 SHS 5.0 HEAD BEAM
FB1	150 x 100 RHS 5.0 FASCIA BEAM
VB1	180 UB 22 VALLEY BEAM
BR1	75 EA 6.0 BRACE
BR2	75 SHS 4.0 BRACE
BR3	125 SHS BRACE
BR4	100 SHS 4.0 BRACE
BR5	75 SHS 4.0 BRACE
OR1	125 x 75 RHS 4.0 OUTRIGGER
OR2	100 SHS 4.0 OUTRIGGER
DB1	125 x 75 RHS 4.0 DIAGONAL BRACE
WB1	2-16 RODS DIAGONAL BRACE
RA1	150 x 90 UA 10.0 RAKING ANGLE
TRUSS T2	REFER SECTION 3 REFER SECTION C

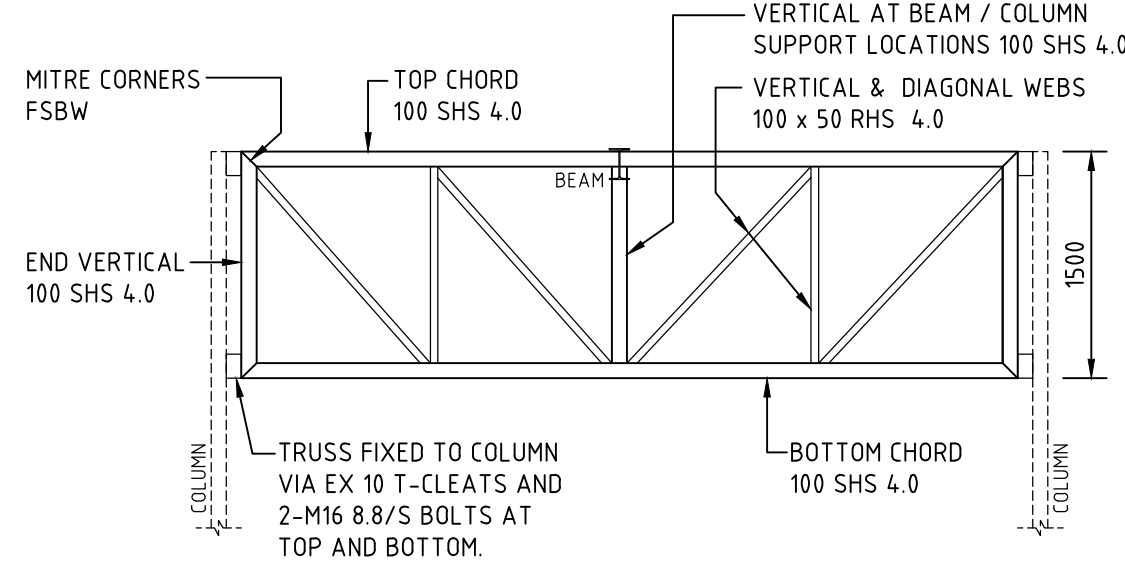

TYPICAL T1 TRUSS ELEVATION 1:50
FULLY WELDED FRAME

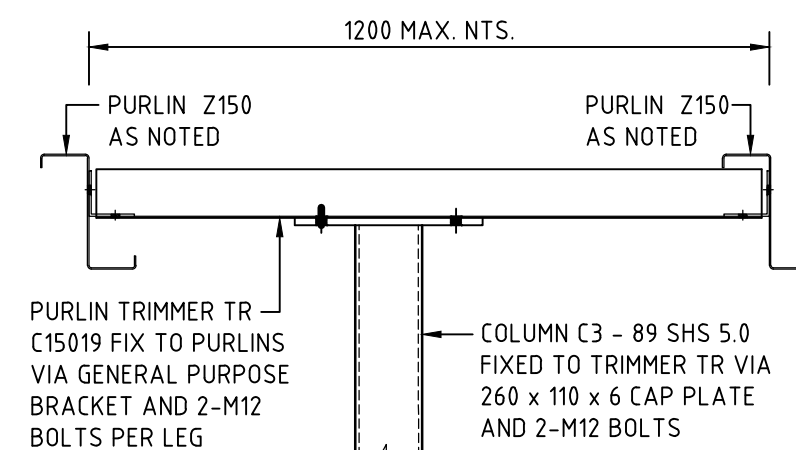


TYPICAL COLUMN TO PURLIN
TRIMMER (TR) FIXING DETAIL 1:10

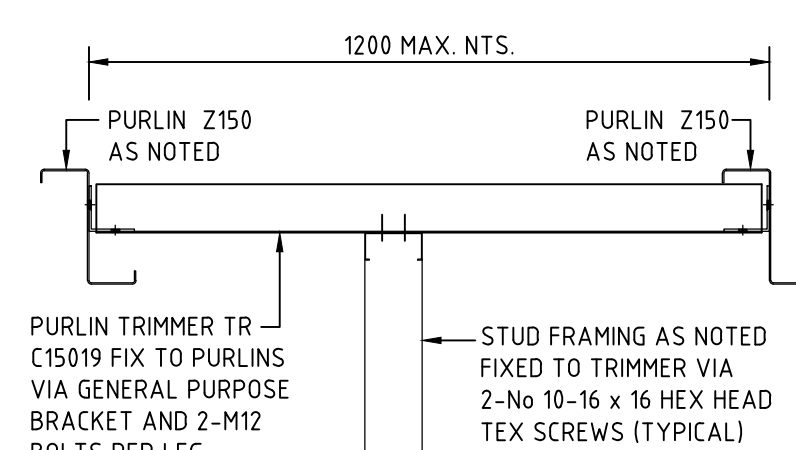

TYPICAL STUD TOP PLATE TO PURLIN
TRIMMER (TR) FIXING DETAIL 1:10

SHEET ROOF CONSTRUCTION

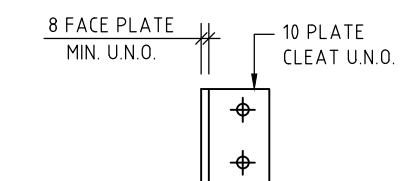

TYPICAL 10 PLATE
T-CLEAT DETAIL U.N.O. 1:10

NO.	AMENDMENT	DATE	INIT.
0	ISSUED FOR TENDER	12.03.26	J.V.
D	ISSUED FOR BOQ	13.02.26	J.V.
C	OUTDOOR AREA AMENDED	13.05.25	J.V.
B	ISSUED FOR DESIGN DEVELOPMENT COST REVIEW	12.05.25	J.S.
A	ISSUED FOR SCHEMATIC DESIGN REVIEW	12.12.23	J.V.

TENDER



STRUCTURAL ROCKINGHAM MHEC & BAC ROCKINGHAM GENERAL HOSPITAL 71 ELANORA DRIVE, COOLOONGUP ROOF LAYOUT PLAN AND DETAILS

DRAWN	J.V.	DESIGNED	P.T.	REDUCTION
CHECKED	P.T.	DHW TENDER No.	DHW0108123	
APPROVED	-			
SCALE	1:100 AT A1	DATE	NOV 2023	DRAWING No.
DHW PROJ No.	15365	DHW FILE No.	2023/01081	S3.01