



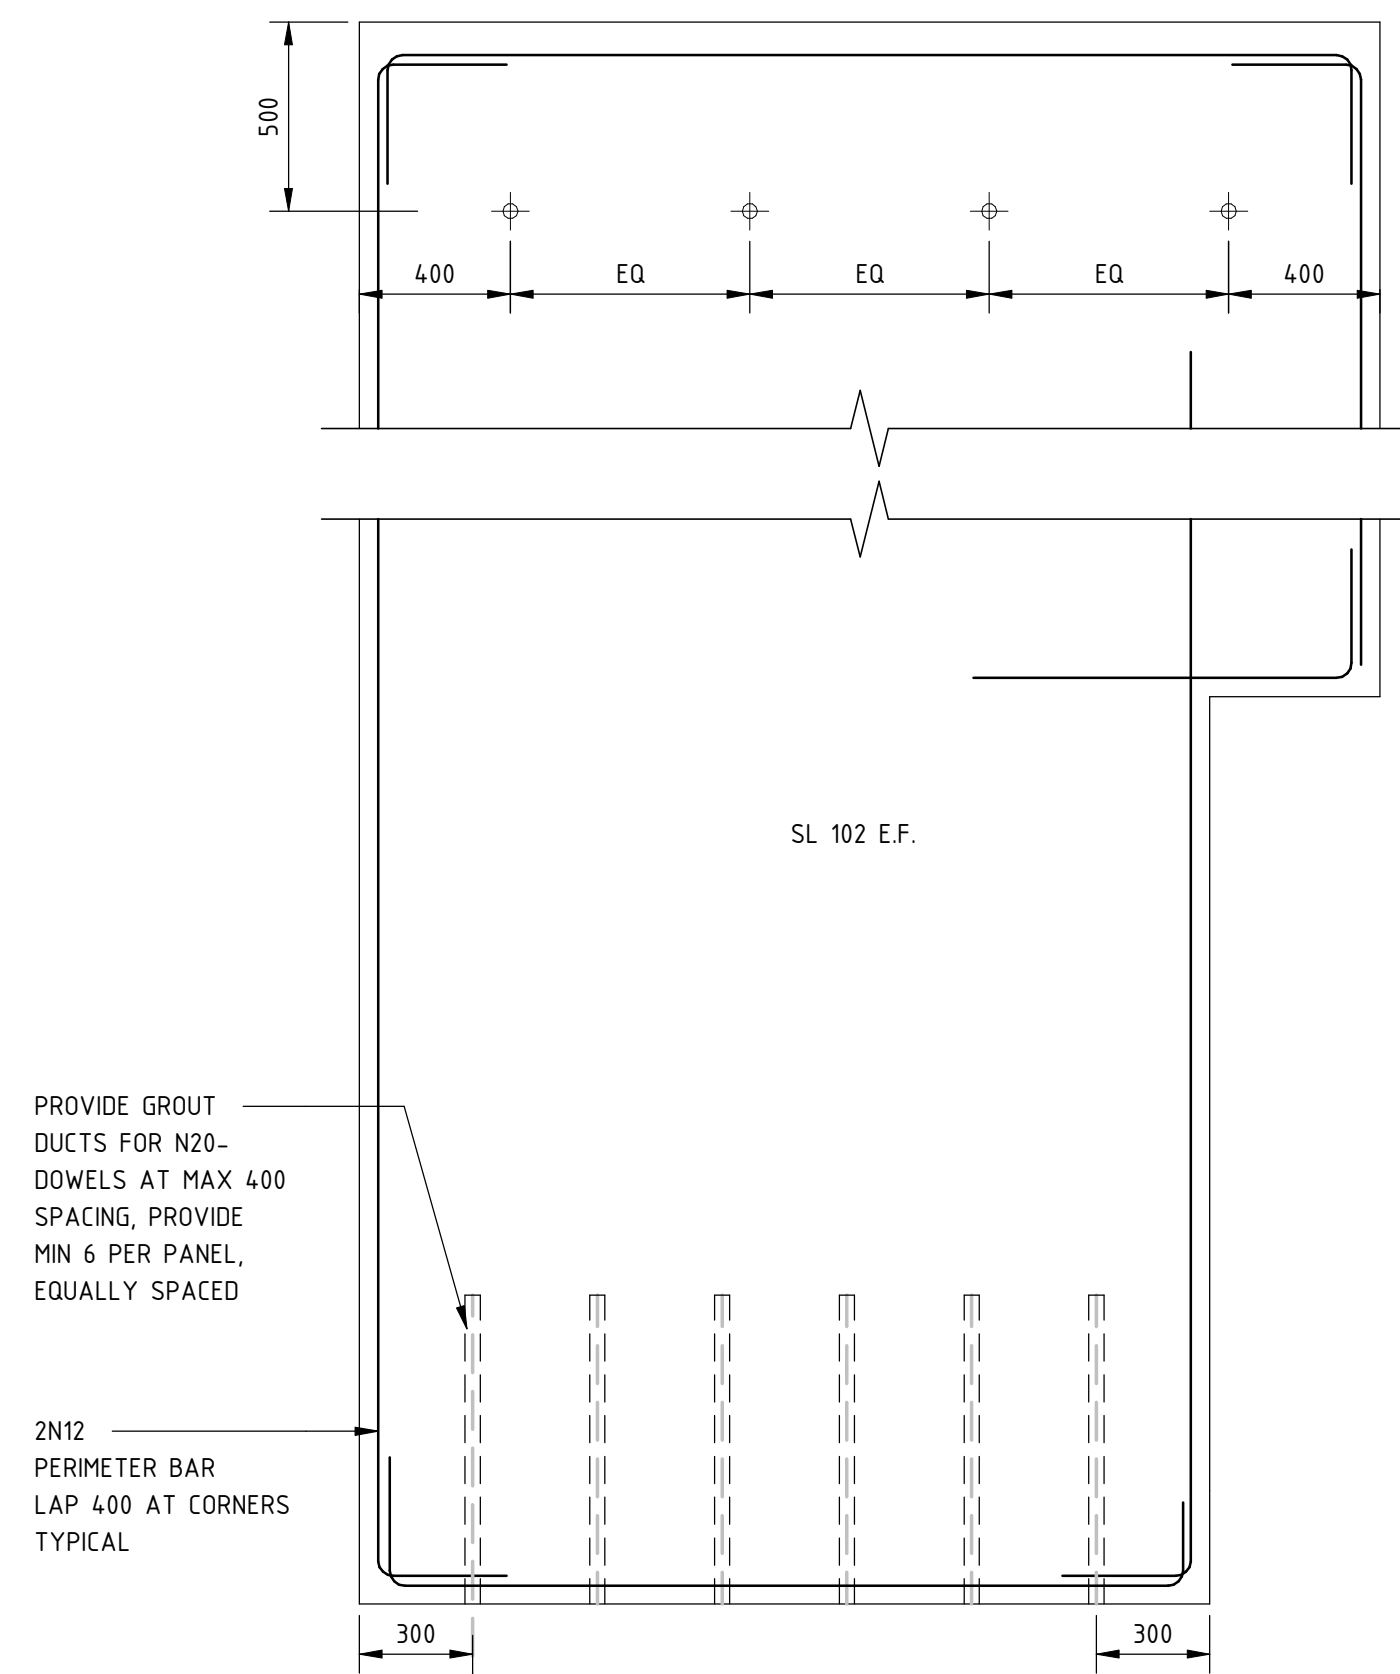

TYPICAL PANEL TYPE "PC-03"

PRECAST PANEL: 200 STRUCTURAL THICKNESS

- BASE CONNECTION: PCN03
- TOP CONNECTION: PCN04

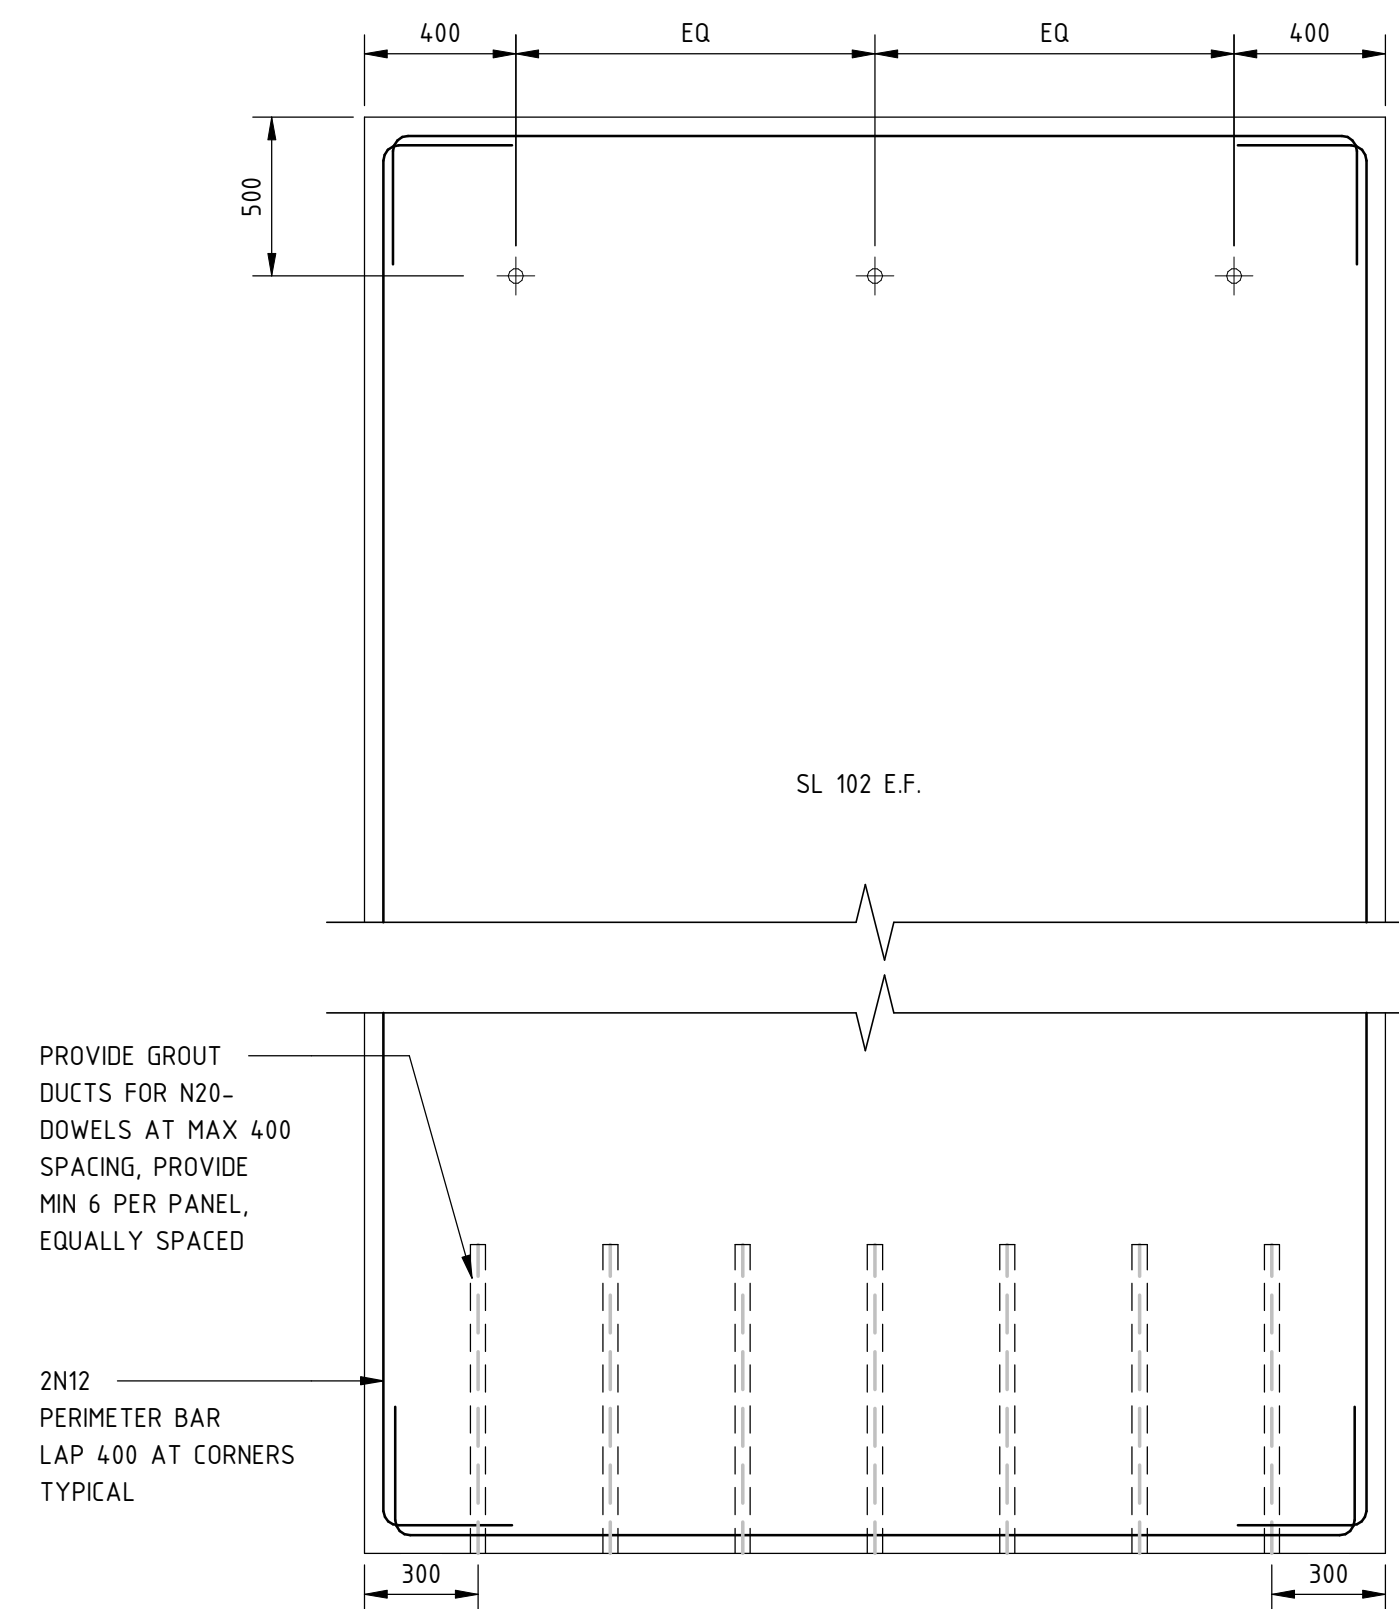


TYPICAL PANEL TYPE "PC-04"

- BASE CONNECTION: PCN0
- TOP CONNECTION: PCN04

NOTES:

1. LOCATION OF PENETRATIONS TO ENGINEERS APPROVAL.
2. USE ABOVE DETAIL UNLESS OTHERWISE NOTED ON WALL ELEVATIONS.

1. REFER ARCHITECTURAL DRAWINGS FOR DETAILS ON THE APPLIED FIRE PROTECTION TO STRUCTURAL STEELWORK
2. REFER DRAWING 12-A-152-ST0010 FOR STANDARD CONNECTION DETAILS
ALL DIMENSIONS TO PRECAST PANELS ARE NOMINAL ONLY AND SHOULD BE REFERENCED WITH THE ARCHITECTS DRAWINGS. THESE SHALL BE CONFIRMED WITH THE PRECAST CONTRACTOR
3. REFER TO THE ARCHITECTS DRAWINGS FOR REBATES, CHAMFERS, DRIPS, SEALS, BAFFLES, ETC. AND EXTENT OF FINISHES
4. REFER TO THE ARCHITECTS DRAWINGS FOR ALL JOINTING DETAILS
IT IS THE CONTRACTORS RESPONSIBILITY TO CO-ORDINATE ALL PENETRATIONS FOR SERVICES ETC. ALL PENETRATIONS SHALL BE SHOWN ON SHOP DRAWINGS FOR APPROVAL PRIOR TO FABRICATION OF ANY PANEL
5. REFER TO 12-A-152-ST0004 FOR GENERAL PRECAST NOTES, REFER TO 12-A-152-ST0169 FOR PRECAST PANEL TYPES
6. DOWEL TUBE AND FERRULE LOCATIONS ON PRECAST SHOP DRAWINGS SHALL INCORPORATE THE SURVEYED AS BUILT LOCATIONS OF DOWELS
7. PROVIDE ADDITIONAL FERRULES AND/OR WELD PLATES AS REQUIRED - REFER PLANS AND DETAILS

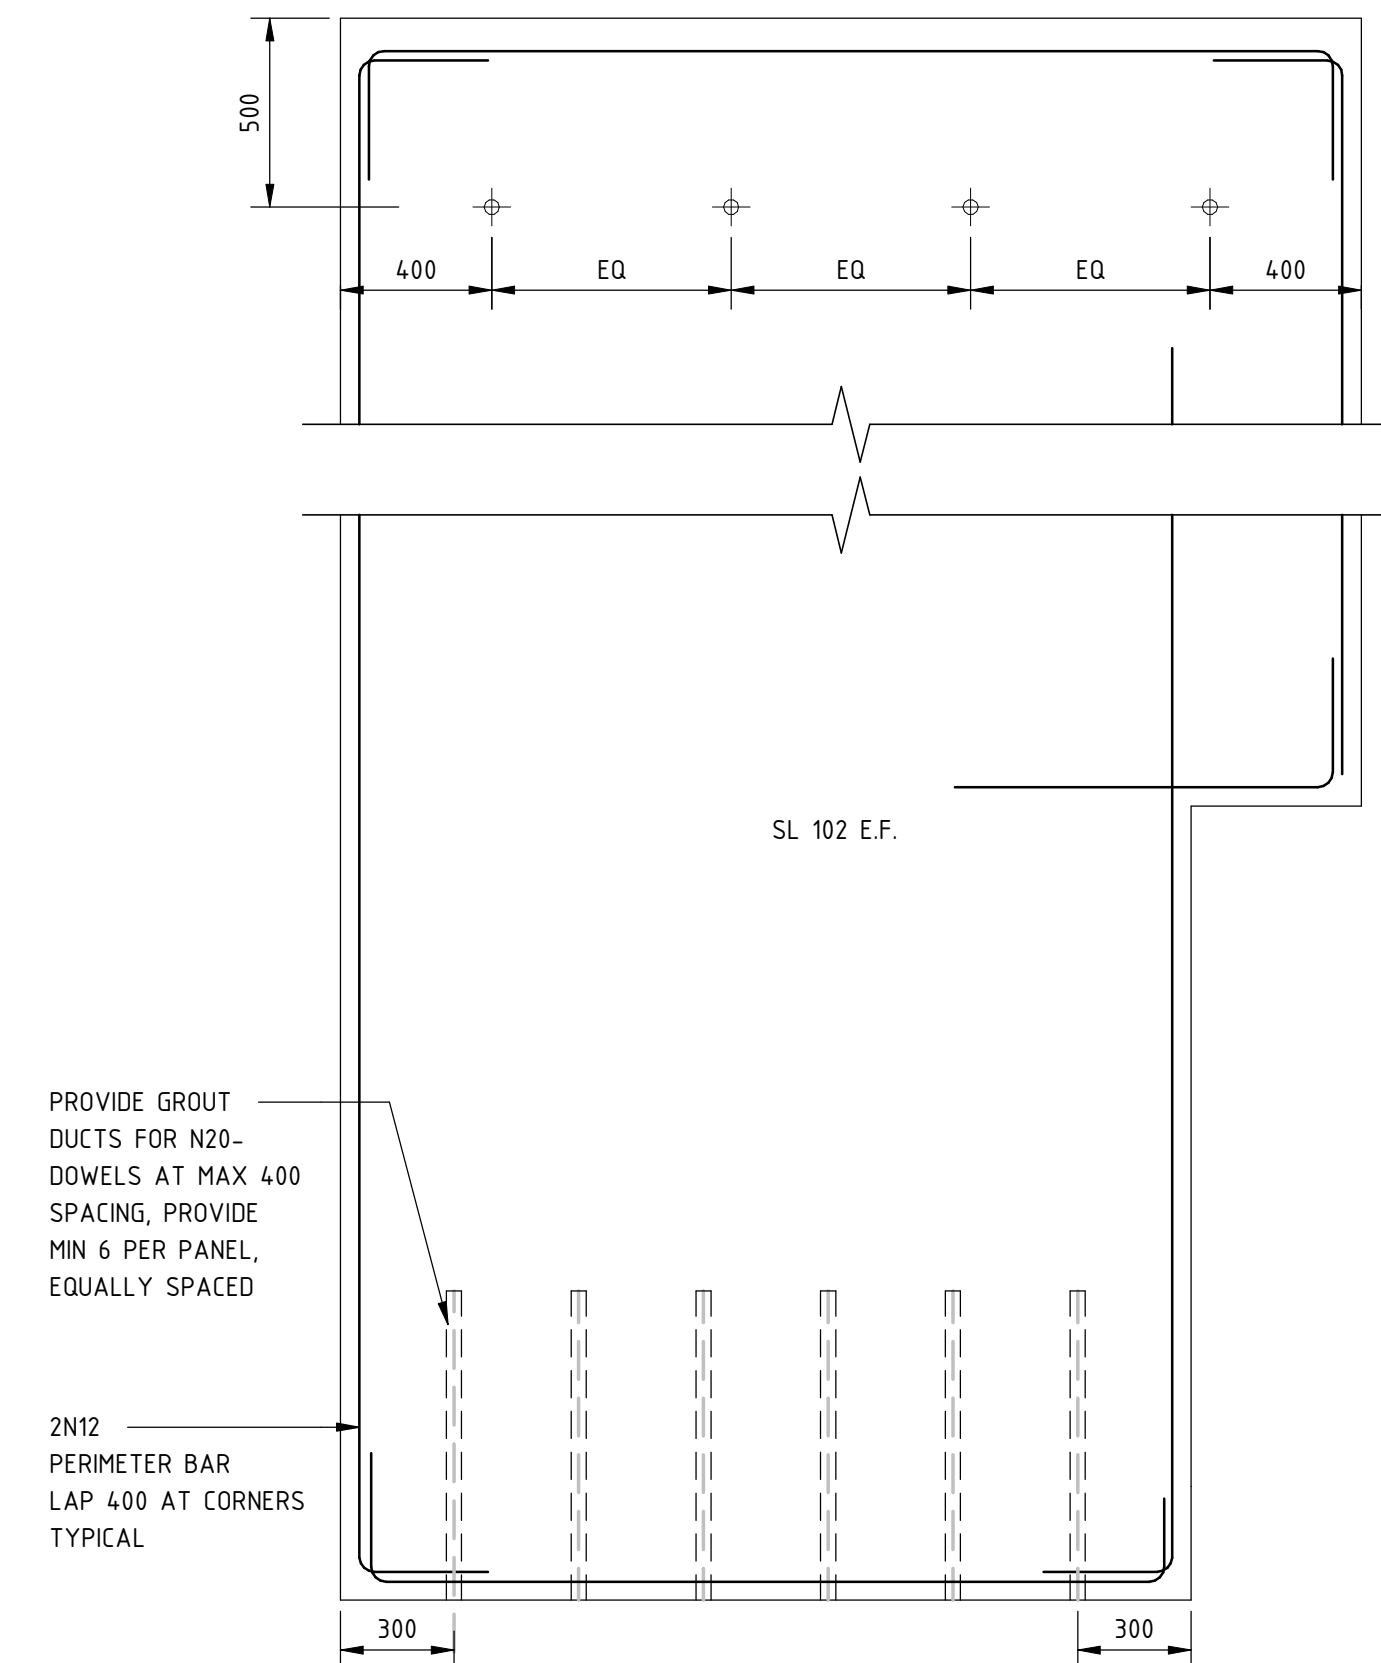

PRECAST PANEL: 200 STRUCTURAL THICKNESS

- BASE CONNECTION: PCN03
- TOP CONNECTION: PCN04

1. THIS DRAWING SHALL BE READ IN CONJUNCTION WITH THE DISCIPLINE CONTRACT SPECIFICATION AND OTHER PROJECT DOCUMENTS.
2. INFORMATION SHOWN ON THIS DRAWING SHALL NOT BE USED FOR CONSTRUCTION PURPOSES. THE DRAWINGS AND SPECIFICATIONS DO NOT PURPORT TO SHOW ALL MINOR ITEMS OF EQUIPMENT AND ACCESSORIES WHICH MAY BE NECESSARY. THESE MINOR ITEMS SHALL BE PROVIDED TO FORM COMPLETE AND FULLY OPERATIONAL SYSTEMS.
3. THE CONTRACTORS SHALL BE FULLY AWARE OF THE OTHER INTERFACING PACKAGES AND SHALL HAVE DEEMED TO HAVE INCLUDED INTER-TRADE INTERFACES. THE INTERFACES IDENTIFIED IN THE DOCUMENTATION ARE TO INDICATE AN INTENT AND ARE NOT INTENDED TO BE EXHAUSTIVE. MAKE ALLOWANCES AS REQUIRED.

ISSUED FOR CONSTRUCTION



ASSEMBLY FACILITY STRUCTURAL PRECAST PANEL ELEVATIONS

PTA Drawing No: 12-A-152-ST0041	REV : 1
---------------------------------	---------

[illegible]

aurecon
www.aurecongroup.com


505695-0000-DRG-ST-1654

REFERENCES

SCALE :	As indicated (@ A1)
DATUM :	HORIZONTAL: PCG94 VERTICAL: AHD71

PTA ACCEPTANCE STAMP

DESIGNED	J.BRUIJS
DRAWN	A.DAWSON
CHECKED	M.PEARCE
APPROVED FOR ISSUE	
G.BENTLEY	
DATE	

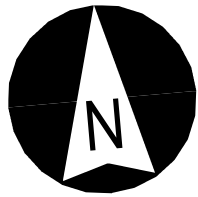

ZONE 01	ZONE 02	ZONE 03
---------	---------	---------

- NOTES:
1.


DO NO SCALE DRAWINGS. WRITTEN DIMENSIONS GOVERN.
2.

ALL DIMENSIONS ARE IN MILLIMETRES UNLESS NOTED OTHERWISE
3.


ALL DIMENSIONS SHALL BE VERIFIED ON SITE BEFORE PROCEEDING WITH THE WORK. RELEVANT PARTY SHALL BE NOTIFIED IN WRITING OF ANY DISCREPANCIES.
4.

THIS DRAWING MUST BE READ IN CONJUNCTION WITH ALL RELEVANT CONTRACTS, SPECIFICATIONS, REPORTS AND DRAWINGS.

ZONE PLAN

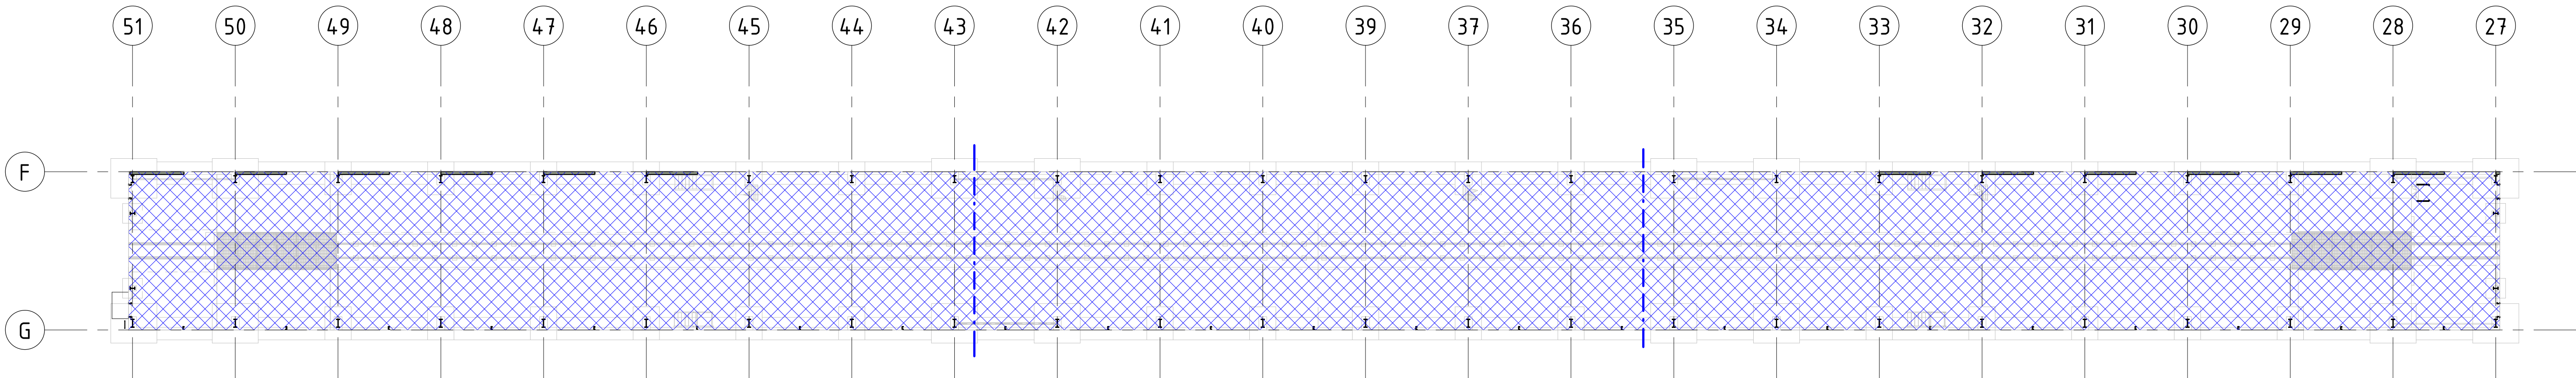


HV TEST FACILITY GROUND LD
1 : 250

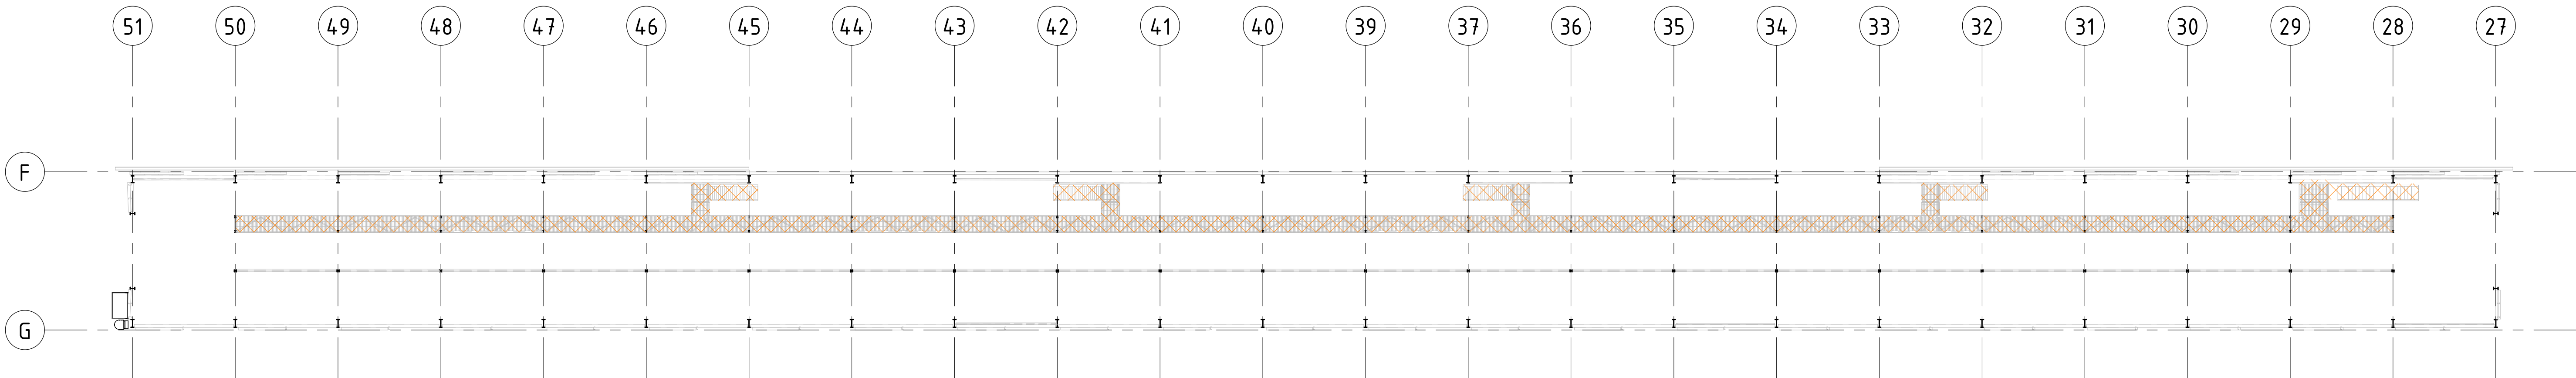


HV MEZZANINE LD
1 : 250

DESIGN LOAD ALLOWANCES - UNFACTORED LIVE LOADS

LEGEND

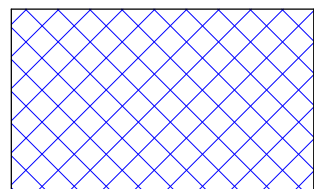

GENERAL
AREA LOAD - 10kPa
AXLE LOAD - 4250kg

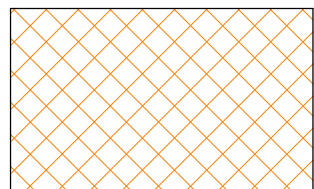

ELEVATED WALKING PLATFORM & STAIRS
AREA LOAD - 2.5kPa
AXLE LOAD - N/A

ROOF
AREA LOAD - 0.25kPa
SDL - 0.25kPa

- AXLE LOAD BASED ON 2000kg CAPACITY PNEUMATIC AND CUSHION FORKLIFT - REFERENCE TYPE CROWN CGC20SC-5
- SDL = 0.5 kPa TYPICAL
- ALLOWANCE FOR RAIL CAR LINE LOADS 22T

- USE OF THESE DRAWINGS
1.


THIS DRAWING SHALL BE READ IN CONJUNCTION WITH THE DISCIPLINE CONTRACT SPECIFICATION AND OTHER PROJECT DOCUMENTS.
2.

DRAWINGS AND DESIGNS UNDERTAKEN BY A SHOP DETAILER SHALL BE PRESENTED TO THE PTA FOR REVIEW AND CONCURRENCE THAT THE DESIGN INTENT HAS BEEN ACHIEVED.
3.

THE CONTRACTORS SHALL BE FULLY AWARE OF THE OTHER INTERFACING PACKAGES AND SHALL HAVE DEEMED TO HAVE INCLUDED INTER-TRADE INTERFACES. THE INTERFACES IDENTIFIED IN THE DOCUMENTATION ARE TO INDICATE AN INTENT AND ARE NOT INTENDED TO BE EXHAUSTIVE. MAKE ALLOWANCES AS REQUIRED.

ISSUED FOR CONSTRUCTION

</	

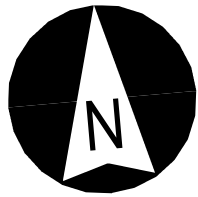


ZONE 01	ZONE 02	ZONE 03
---------	---------	---------

NOTES:

- DO NO SCALE DRAWINGS. WRITTEN DIMENSIONS GOVERN.
- ALL DIMENSIONS ARE IN MILLIMETRES UNLESS NOTED OTHERWISE
- ALL DIMENSIONS SHALL BE VERIFIED ON SITE BEFORE PROCEEDING WITH THE WORK. RELEVANT PARTY SHALL BE NOTIFIED IN WRITING OF ANY DISCREPANCIES.
- THIS DRAWING MUST BE READ IN CONJUNCTION WITH ALL RELEVANT CONTRACTS, SPECIFICATIONS, REPORTS AND DRAWINGS.

ZONE PLAN

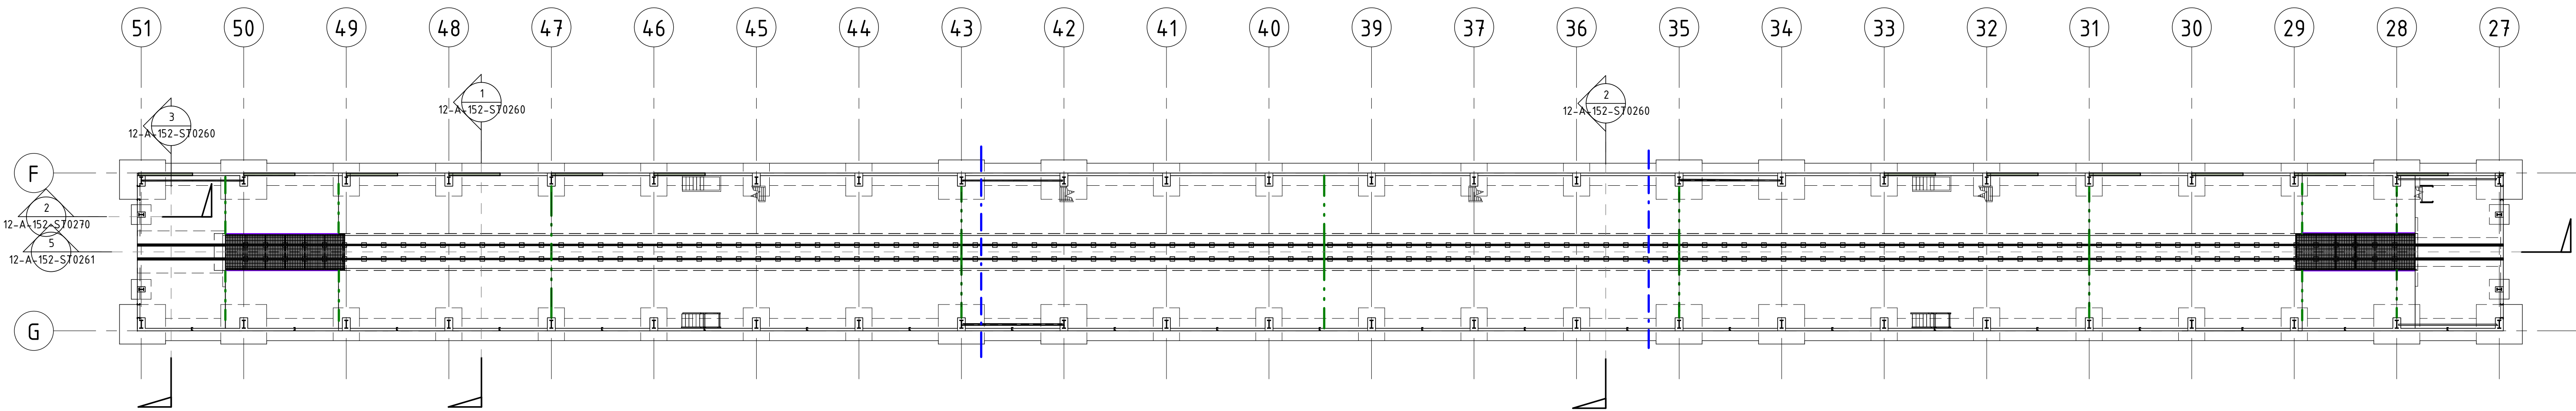

FOOTING AND GROUND SLAB PLAN
1 : 250

USE OF THESE DRAWINGS

- THIS DRAWING SHALL BE READ IN CONJUNCTION WITH THE DISCIPLINE CONTRACT SPECIFICATION AND OTHER PROJECT DOCUMENTS.
- DRAWINGS AND DESIGNS UNDERTAKEN BY A SHOP DETAILER SHALL BE PRESENTED TO THE PTA FOR REVIEW AND CONCURRENCE THAT THE DESIGN INTENT HAS BEEN ACHIEVED.
- THE CONTRACTORS SHALL BE FULLY AWARE OF THE OTHER INTERFACING PACKAGES AND SHALL HAVE DEEMED TO HAVE INCLUDED INTER-TRADE INTERFACES. THE INTERFACES IDENTIFIED IN THE DOCUMENTATION ARE TO INDICATE AN INTENT AND ARE NOT INTENDED TO BE EXHAUSTIVE. MAKE ALLOWANCES AS REQUIRED.

ISSUED FOR CONSTRUCTION

0	01.10.19	ISSUED FOR CONSTRUCTION	J.S.	A.C.D.	M.P.	G.B.
REV	DATE	AMENDMENT	DSN	DRN	CHKD	APP
ORIG SIZE	A1	SCALE 1:250 AT A1	This document must not be copied without PTA's written permission, and the contents thereof must not be imparted to a third party nor be used for any unauthorised purpose.			




505695-0000-DRG-ST-1250

REFERENCES

SCALE :	As indicated (@ A1)
DATUM :	
HORIZONTAL:	PCG94
VERTICAL:	AHD71
PTA ACCEPTANCE STAMP	


DESIGNED	J.SPANO
DRAWN	A.DAWSON
CHECKED	M.PEARCE
APPROVED FOR ISSUE	
DATE	G.BENTLEY

	DETAILED DESIGN FOR THE BELLEVUE DEPOT
HV TESTING FACILITY STRUCTURAL FOOTING AND GROUND FLOOR PLAN	
PTA Drawing No: 12-A-152-ST0210	REV : 0

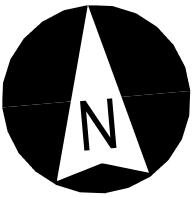

NOTES :


- FOR GENERAL NOTES AND DETAILS REFER TO 12-A-152-ST0003 TO 12-A-152-ST0031
- FOR SLAB DETAILS , REFER TO 12-A-152-0010
- FOR FOUNDATION DETAILS REFER TO 12-A-152-0271
- FOR CONCRETE PEDESTAL DETAILS, REFER TO 12-A-152-0272
- SLAB IN HV BUILDING TO BE 150MM THK.WITH STEEL FIBRE REINFORCEMENT + SUPPLEMENTARY MESH UNO.
FIBRE SUPPLIER : BOSFA PTY. LTD
FIBRE NAME : DRAMIX 4D
DOSAGE : 65/60 AT 30KG/M3
TYPICAL SUPPLEMENTARY MESH : SL81
OTHER SUPPLEMENTARY REINFORCEMENT : REFER TO CONCRETE DRAWINGS
- ISOLATION JOINTS TO ALL SLAB PERIMETERS UNO
- FOUNDING MATERIAL BELOW GROUND TO HAVE MINIMUM 250KPA BEARING CAPACITY
- PENETRATIONS FOR BELOW GROUND CONDUITS MUST BE COORDINATED WITH SERVICES DRAWINGS
- REFER TO EARTHING AND BONDING REPORT FOR EARTHING AND BONDING REQUIREMENTS
- REFER TO TRACK DRAWINGS FOR RAIL TYPE, GAUGE AND FIXING DETAILS
- REFER 12-A-152-ST0070 FOR TYPICAL SLAB TRIMMING DETAILS

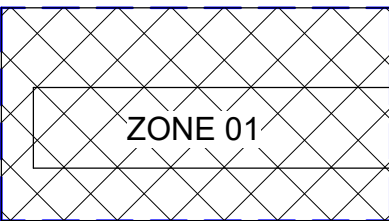

ZONE PLAN

NOTES:

- DO NO SCALE DRAWINGS. WRITTEN DIMENSIONS GOVERN.
- ALL DIMENSIONS ARE IN MILLIMETRES UNLESS NOTED OTHERWISE
- ALL DIMENSIONS SHALL BE VERIFIED ON SITE BEFORE PROCEEDING WITH THE WORK. RELEVANT PARTY SHALL BE NOTIFIED IN WRITING OF ANY DISCREPANCIES.
- THIS DRAWING MUST BE READ IN CONJUNCTION WITH ALL RELEVANT CONTRACTS, SPECIFICATIONS, REPORTS AND DRAWINGS.

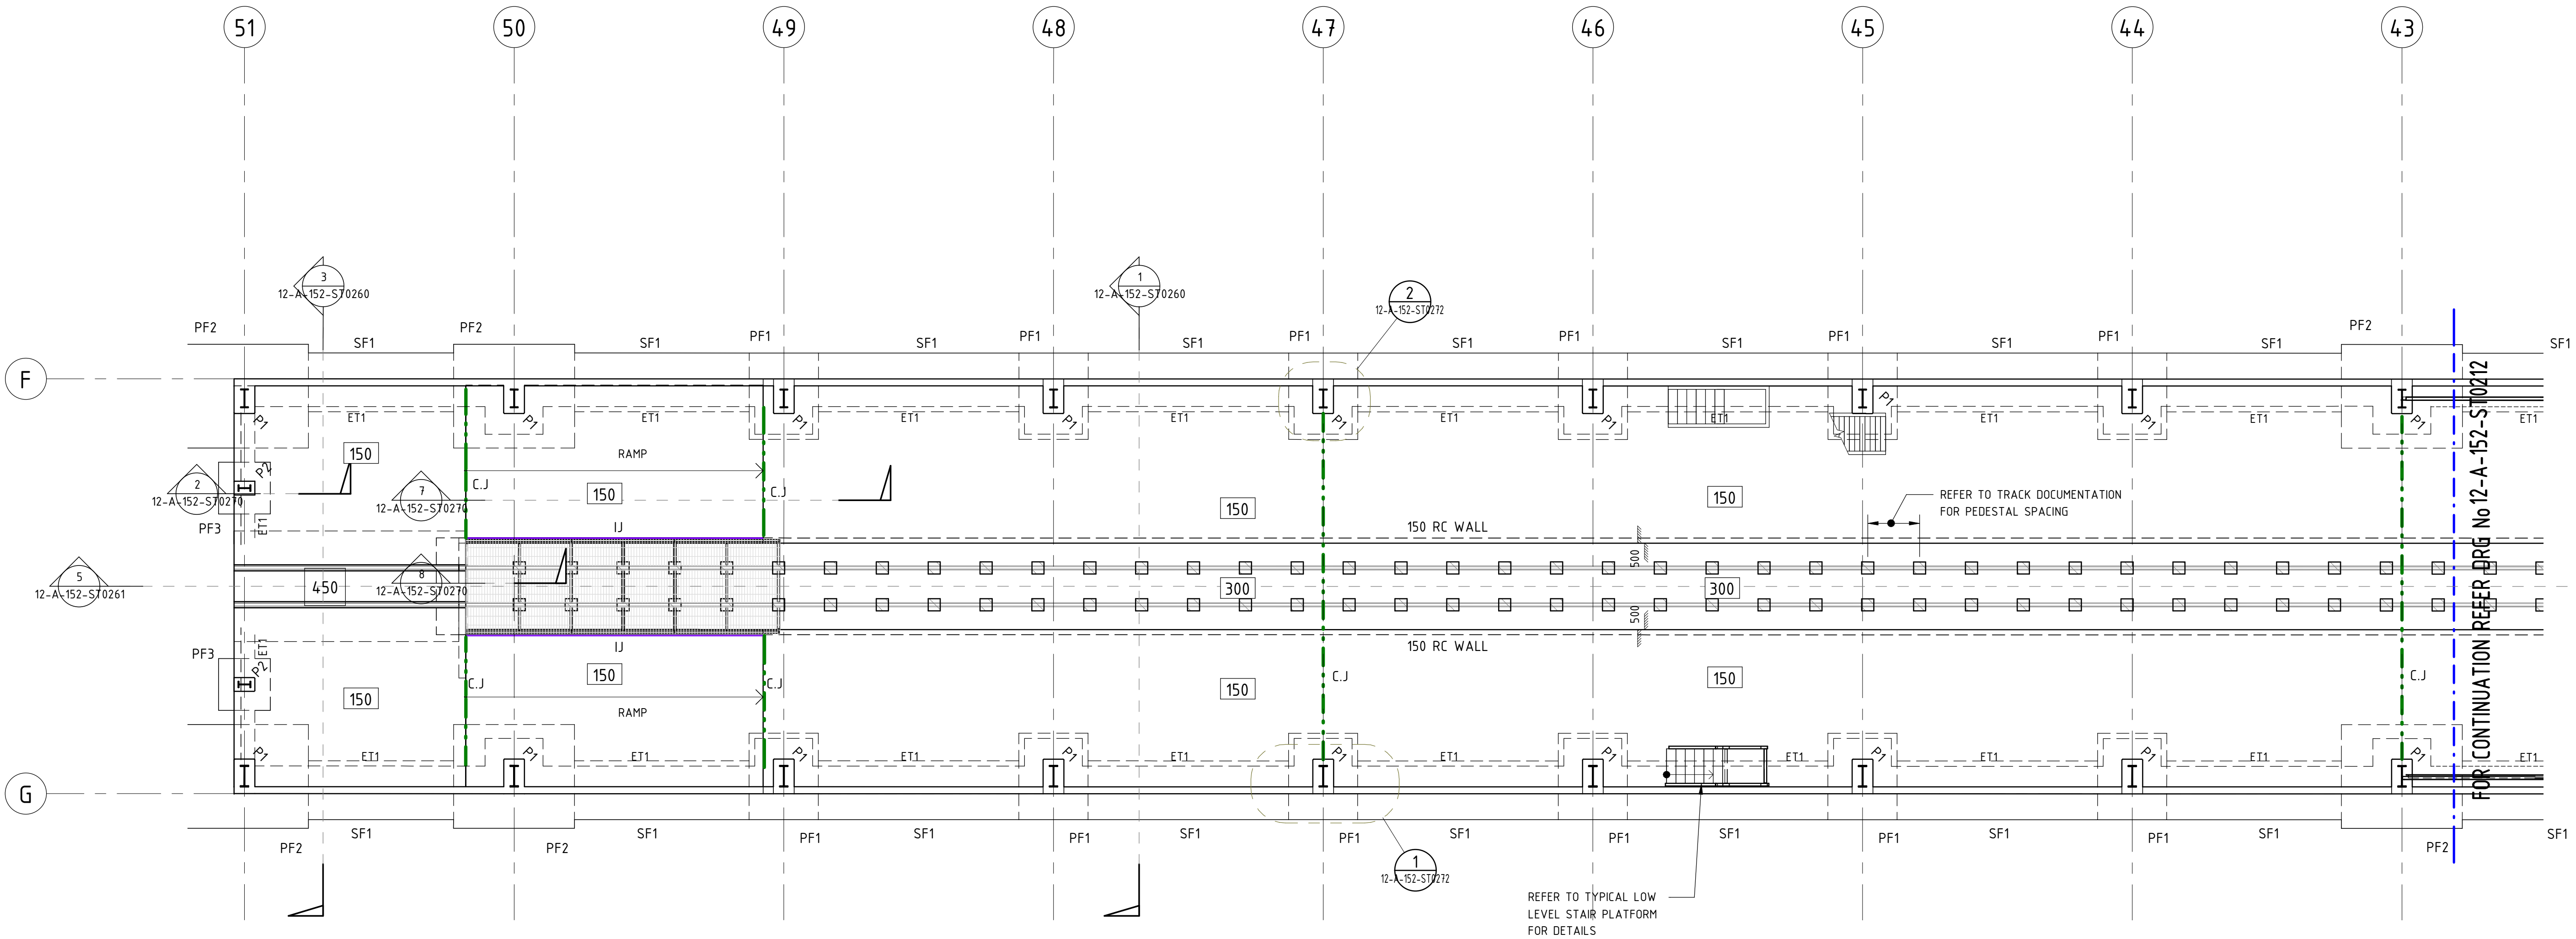

SLAB ON GRADE LEGEND

- 300 - DENOTES SLAB THICKNESS
- STEP - DENOTES SLAB STEP; REFER ARCHITECTURAL DRAWINGS FOR DETAILS
- I.J. - DENOTES ISOLATION JOINT (I.J.)
- C.J. - DENOTES CONSTRUCTION JOINT (C.J.)
- PF - DENOTES PEDESTAL, REFER ST-00176

FOOTING SCHEDULE

MARK	SIZE (W x L x D)	REMARKS
PF1	2500 x 2000 x 600	
PF2	3000 x 3500 x 600	
PF3	1500 x 1500 x 500	
SF1	1700 x 300	

USE OF THESE DRAWINGS

- THIS DRAWING SHALL BE READ IN CONJUNCTION WITH THE DISCIPLINE CONTRACT SPECIFICATION AND OTHER PROJECT DOCUMENTS.
- DRAWINGS AND DESIGNS UNDERTAKEN BY A SHOP DETAILER SHALL BE PRESENTED TO THE PTA FOR REVIEW AND CONCURRENCE THAT THE DESIGN INTENT HAS BEEN ACHIEVED.
- THE CONTRACTORS SHALL BE FULLY AWARE OF THE OTHER INTERFACING PACKAGES AND SHALL HAVE DEEMED TO HAVE INCLUDED INTER-TRADE INTERFACES. THE INTERFACES IDENTIFIED IN THE DOCUMENTATION ARE TO INDICATE AN INTENT AND ARE NOT INTENDED TO BE EXHAUSTIVE. MAKE ALLOWANCES AS REQUIRED.

ISSUED FOR CONSTRUCTION

REV	DATE	ISSUED FOR CONSTRUCTION	AMENDMENT	DSN	DRN	CHKD	APP
0	01.10.19			J.S.	A.C.D.	M.P.	G.B.
1	01.10.19						
2	01.10.19						
aurecon
www.aurecongroup.com

505695-0000-DRG-ST-1251

REFERENCES

SCALE :
As indicated (@ A1)
DATUM :
HORIZONTAL: PC694
VERTICAL: AHD71
PTA ACCEPTANCE STAMP

DESIGNED J.SPANO
DRAWN A.DAWSON
CHECKED M.PEARCE
APPROVED FOR ISSUE
G.BENTLEY
DATE



DETAILED DESIGN FOR THE BELLEVUE DEPOT

HV TESTING FACILITY
STRUCTURAL
FOOTING AND GROUND FLOOR PLAN - ZONE 01
PTA Drawing No: 12-A-152-ST0211
REV : 0



1. FOR GENERAL NOTES AND DETAILS REFER TO 12-A-152-ST0003 TO 12-A-152-ST0031
2. FOR SLAB DETAILS , REFER TO 12-A-152-0010
3. FOR FOUNDATION DETAILS REFER TO 12-A-152-0271
4. FOR CONCRETE PEDESTAL DETAILS, REFER TO 12-A-152-0272
5. SLAB IN HV BUILDING TO BE 150MM THK.WITH STEEL FIBRE REINFORCEMENT + SUPPLEMENTARY MESH UNO.
6. FIBRE SUPPLIER : BOSFA PTY. LTD
7. FIBRE NAME : DRAMIX 4D
8. DOSAGE : 65/60 AT 30KG/M3
9. TYPICAL SUPPLEMENTARY MESH : SL81
10. OTHER SUPPLEMENTARY REINFORCEMENT : REFER TO CONCRETE DRAWINGS
11. ISOLATION JOINTS TO ALL SLAB PERIMETERS UNO
12. FOUNDATION MATERIAL BELOW GROUND TO HAVE MINIMUM 250KPA BEARING CAPACITY
13. PENETRATIONS FOR BELOW GROUND CONDUITS MUST BE COORDINATED WITH SERVICES DRAWINGS
14. REFER TO EARTHING AND BONDING REPORT FOR EARTHING AND BONDING REQUIREMENTS
15. REFER TO TRACK DRAWINGS FOR RAIL TYPE, GAUGE AND FIXING DETAILS
16. REFER 12-A-152-ST0070 FOR TYPICAL SLAB TRIMMING DETAILS



NOTES:

1. DO NO SCALE DRAWINGS. WRITTEN DIMENSIONS GOVERN.
2. ALL DIMENSIONS ARE IN MILLIMETRES UNLESS NOTED OTHERWISE
3. ALL DIMENSIONS SHALL BE VERIFIED ON SITE BEFORE PROCEEDING WITH THE WORK. RELEVANT PARTY SHALL BE NOTIFIED IN WRITING OF ANY DISCREPANCIES.
4. THIS DRAWING MUST BE READ IN CONJUNCTION WITH ALL RELEVANT CONTRACTS, SPECIFICATIONS, REPORTS AND DRAWINGS.



1 : 100

SLAB ON GRADE LEGEND

	- DENOTES SLAB THICKNESS
	- DENOTES SLAB STEP, REFER ARCHITECTURAL DRAWINGS FOR DETAILS
	- DENOTES ISOLATION JOINT (IJ)
	- DENOTES CONSTRUCTION JOINT (C.J.)
	- DENOTES PEDESTAL, REFER ST-00176

[illegible]

aurecon
www.aurecongroup.com

505695-0000-DRG-ST-1252

REFERENCES

SCALE :
As indicated (@ A1)

DATUM :
HORIZONTAL: PCG94
VERTICAL: AHD71

DESIGNED	J.SPANO
DRAWN	A.DAWSON
CHECKED	M.PEARCE
APPROVED FOR ISSUE	
G.BENTLEY	
DATE	

USE OF THESE DRAWINGS

1. THIS DRAWING SHALL BE READ IN CONJUNCTION WITH THE DISCIPLINE CONTRACT SPECIFICATION AND OTHER PROJECT DOCUMENTS.
2. DRAWINGS AND DESIGNS UNDERTAKEN BY A SHOP DETAILER SHALL BE PRESENTED TO THE PTA FOR REVIEW AND CONCURRENCE THAT THE DESIGN INTENT HAS BEEN ACHIEVED.
3. THE CONTRACTORS SHALL BE FULLY AWARE OF THE OTHER INTERFACING PACKAGES AND SHALL HAVE DEEMED TO HAVE INCLUDED INTER-TRADE INTERFACES. THE INTERFACES IDENTIFIED IN THE DOCUMENTATION ARE TO INDICATE AN INTENT AND ARE NOT INTENDED TO BE EXHAUSTIVE. MAKE ALLOWANCES AS REQUIRED.

ISSUED FOR CONSTRUCTION



DETAILED DESIGN FOR THE BELLEVUE DEPOT

HV TESTING FACILITY
STRUCTURAL
FOOTING AND GROUND FLOOR PLAN - ZONE 02

PTA Drawing No: 12-A-152-ST0212	REV : 0
---------------------------------	---------




1. FOR GENERAL NOTES AND DETAILS REFER TO 12-A-152-ST0003 TO 12-A-152-ST0031
2. FOR SLAB DETAILS , REFER TO 12-A-152-0010
3. FOR FOUNDATION DETAILS REFER TO 12-A-152-0271
4. FOR CONCRETE PEDESTAL DETAILS, REFER TO 12-A-152-0272
5. SLAB IN HV BUILDING TO BE 150MM THK.WITH STEEL FIBRE REINFORCEMENT + SUPPLEMENTARY MESH UNO.
FIBRE SUPPLIER : BOSFA PTY. LTD
FIBRE NAME : DRAMIX 4D
DOSAGE : 65/60 AT 30KG/M3
TYPICAL SUPPLEMENTARY MESH : SL81
OTHER SUPPLEMENTARY REINFORCEMENT : REFER TO CONCRETE DRAWINGS
6. ISOLATION JOINTS TO ALL SLAB PERIMETERS UNO
7. FOUNDING MATERIAL BELOW GROUND TO HAVE MINIMUM 250KPA BEARING CAPACITY
8. PENETRATIONS FOR BELOW GROUND CONDUITS MUST BE COORDINATED WITH SERVICES DRAWINGS
9. REFER TO EARTHING AND BONDING REPORT FOR EARTHING AND BONDING REQUIREMENTS
10. REFER TO TRAC DRAWINGS FOR RAIL TYPE, GAUGE AND FIXING DETAILS
11. REFER 12-A-152-ST0070 FOR TYPICAL SLAB TRIMMING DETAILS

ZONE PLAN

NOTES:

1. DO NO SCALE DRAWINGS. WRITTEN DIMENSIONS GOVERN.
2. ALL DIMENSIONS ARE IN MILLIMETRES UNLESS NOTED OTHERWISE
3. ALL DIMENSIONS SHALL BE VERIFIED ON SITE BEFORE PROCEEDING WITH THE WORK. RELEVANT PARTY SHALL BE NOTIFIED IN WRITING OF ANY DISCREPANCIES.
4. THIS DRAWING MUST BE READ IN CONJUNCTION WITH ALL RELEVANT CONTRACTS, SPECIFICATIONS, REPORTS AND DRAWINGS.

ONE 03

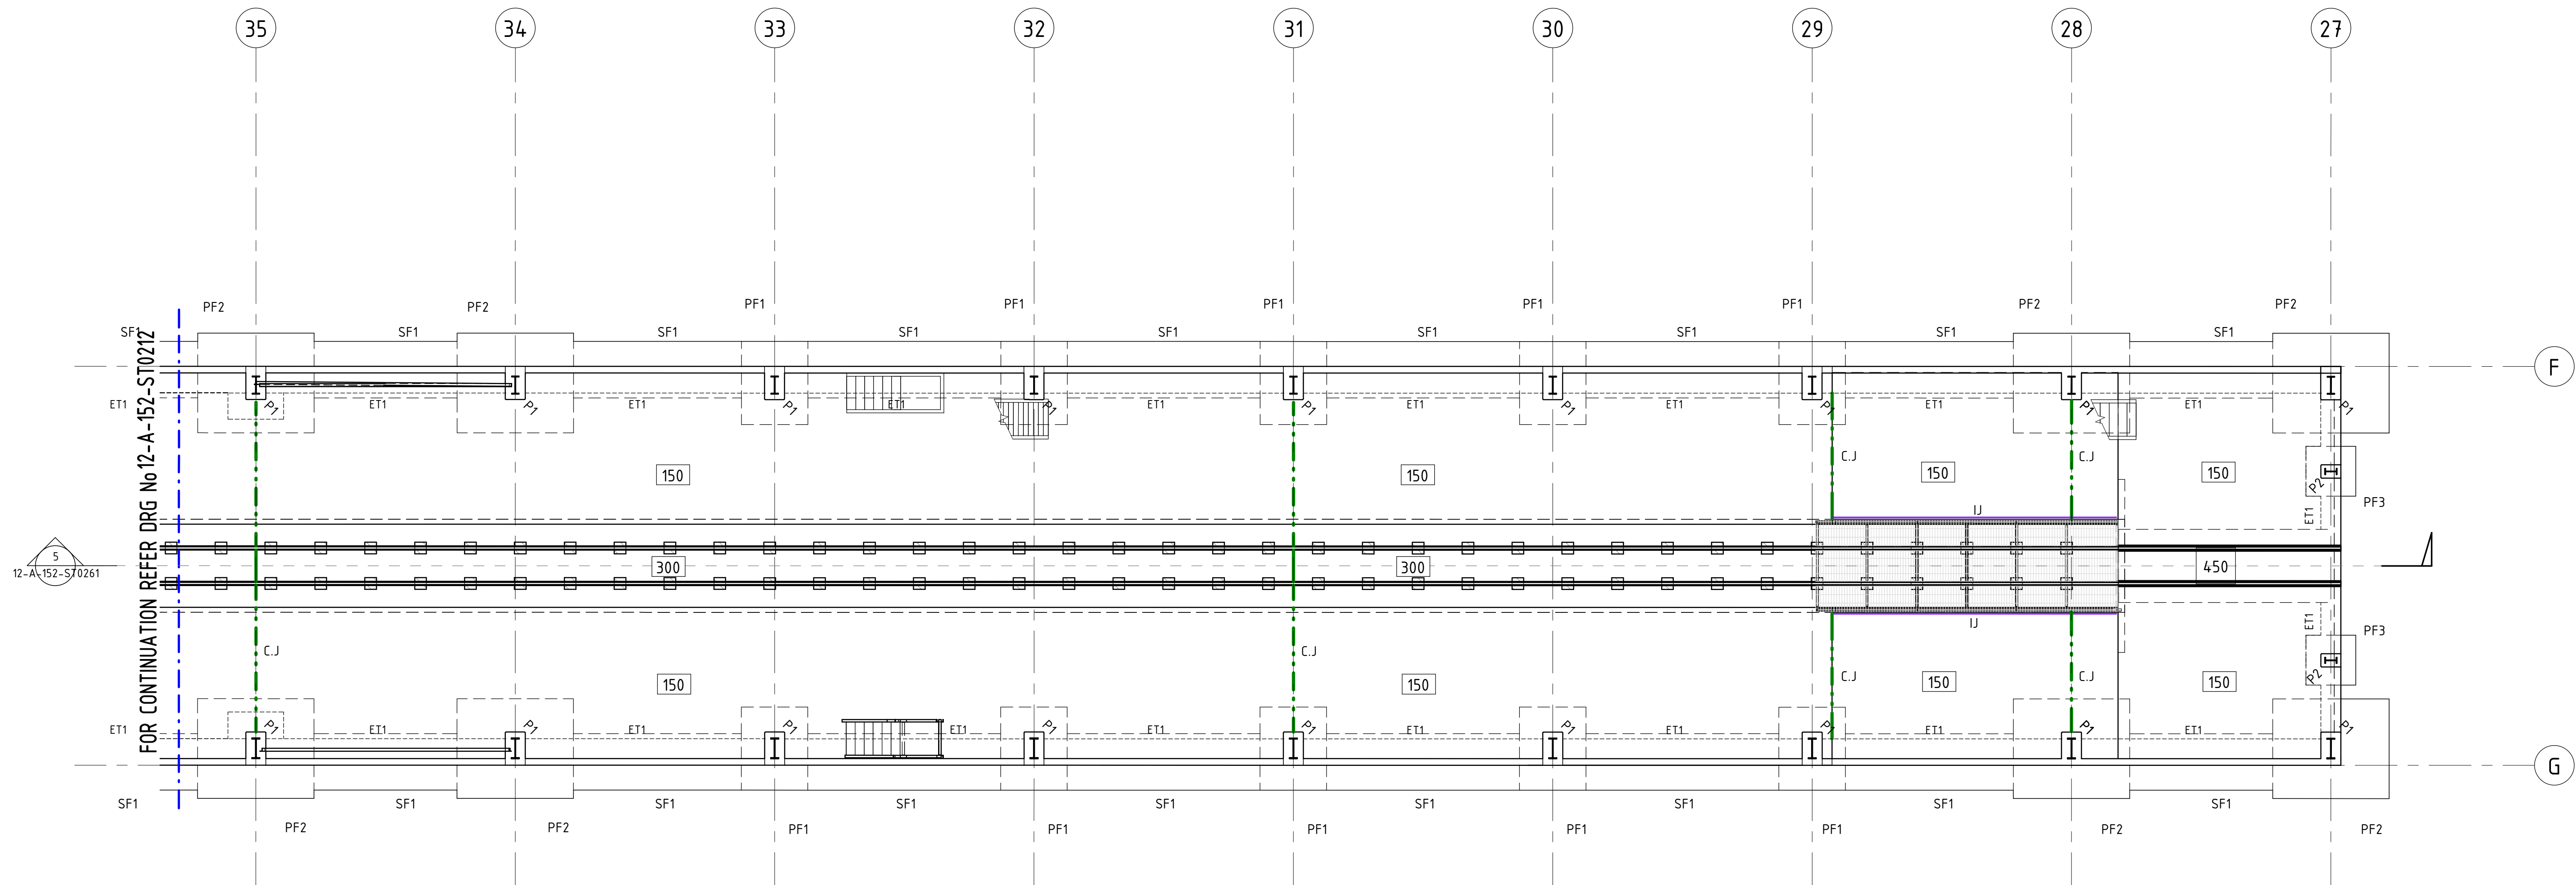

FOOTING AND GROUND SLAB PLAN (ZONE 3)

1 : 100

SLAB ON GRADE LEGEND

-  - DENOTES SLAB THICKNESS
-  STEP - DENOTES SLAB STEP; REFER ARCHITECTURAL DRAWINGS FOR DETAILS
-  - DENOTES ISOLATION JOINT (I.J.)
-  - DENOTES CONSTRUCTION JOINT (C.J.)
-  - DENOTES PEDESTAL, REFER ST-00176

[illegible]

aurecon
www.aurecongroup.com

505695-0000-DRG-ST-1253

REFERENCES

SCALE :
As indicated (@ A1)

DATUM :
HORIZONTAL: PCG94
VERTICAL: AHD71

PTA ACCEPTANCE STAMP

DESIGNED	J.SPANO
DRAWN	A.DAWSON
CHECKED	M.PEARCE
APPROVED FOR ISSUE	
G.BENTLEY	
DATE	

USE OF THESE DRAWINGS

1. THIS DRAWING SHALL BE READ IN CONJUNCTION WITH THE DISCIPLINE CONTRACT SPECIFICATION AND OTHER PROJECT DOCUMENTS.
2. DRAWINGS AND DESIGNS UNDERTAKEN BY A SHOP DETAILER SHALL BE PRESENTED TO THE PTA FOR REVIEW AND CONCURRENCE THAT THE DESIGN INTENT HAS BEEN ACHIEVED.
3. THE CONTRACTORS SHALL BE FULLY AWARE OF THE OTHER INTERFACING PACKAGES AND SHALL HAVE DEEMED TO HAVE INCLUDED INTER-TRADE INTERFACES. THE INTERFACES IDENTIFIED IN THE DOCUMENTATION ARE TO INDICATE AN INTENT AND ARE NOT INTENDED TO BE EXHAUSTIVE. MAKE ALLOWANCES AS REQUIRED.



ISSUED FOR CONSTRUCTION



DETAILED DESIGN FOR THE BELLEVUE DEPOT


HV TESTING FACILITY
STRUCTURAL
FOOTING AND GROUND FLOOR PLAN - ZONE 03

PTA Drawing No: 12-A-152-ST0213	REV : 0
---------------------------------	---------

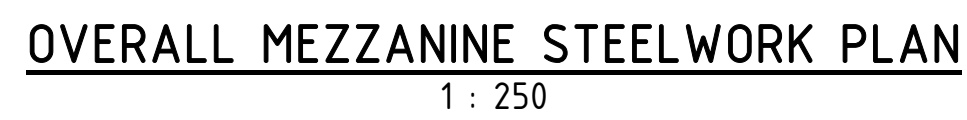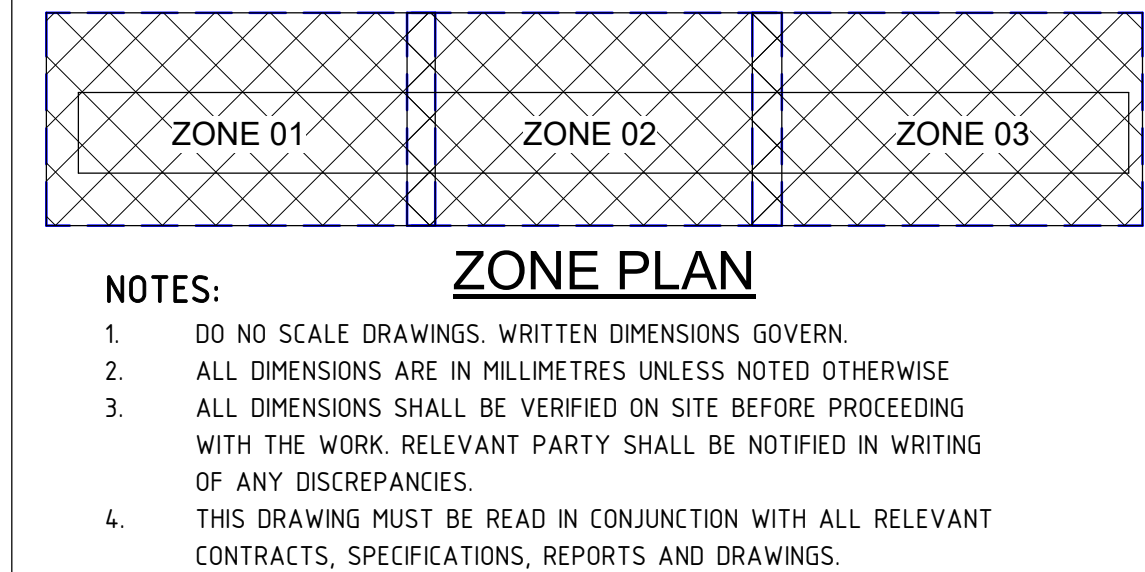


ISSUED FOR CONSTRUCTION


Plot Date: 10/1/2019 9:25:25 AM Office: Filename: BIM 360://505695 - Bellevue Depot/505695-ST-BELLEVUE DEPOT-02B.rvt

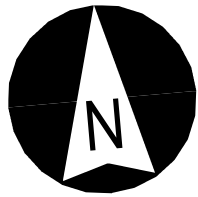

- NOTES:
1. REFER TO ARCHITECTS DRAWINGS FOR DIMENSIONS AND LEVELS
 2. REFER TO THE STRUCTURAL SPECIFICATION FOR H.D. GALVANISING REQUIREMENTS
 3. REFER TO SERVICES SUBCONTRACTOR DETAILS FOR SECONDARY STEELWORK TO SUPPORT SERVICES EQUIPMENT AND FOR ISOLATION DETAILS
 4. PROVIDE EDGE PROTECTION TO ARCHITECTS DETAILS
 5. DESIGN OF FLOOR GRATING TO BE UNDERTAKEN BY D&C CONTRACTOR
 6. REFER TO ARCHITECTURAL DRAWINGS FOR TYP. SYSTEM WIDE PROPRIETARY HANDRAIL DETAILS

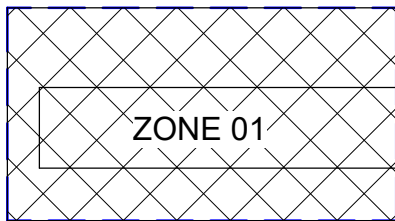

- ZONE PLAN**
- NOTES:
1. DO NO SCALE DRAWINGS. WRITTEN DIMENSIONS GOVERN.
 2. ALL DIMENSIONS ARE IN MILLIMETRES UNLESS NOTED OTHERWISE
 3. ALL DIMENSIONS SHALL BE VERIFIED ON SITE BEFORE PROCEEDING WITH THE WORK. RELEVANT PARTY SHALL BE NOTIFIED IN WRITING OF ANY DISCREPANCIES.
 4. THIS DRAWING MUST BE READ IN CONJUNCTION WITH ALL RELEVANT CONTRACTS, SPECIFICATIONS, REPORTS AND DRAWINGS.

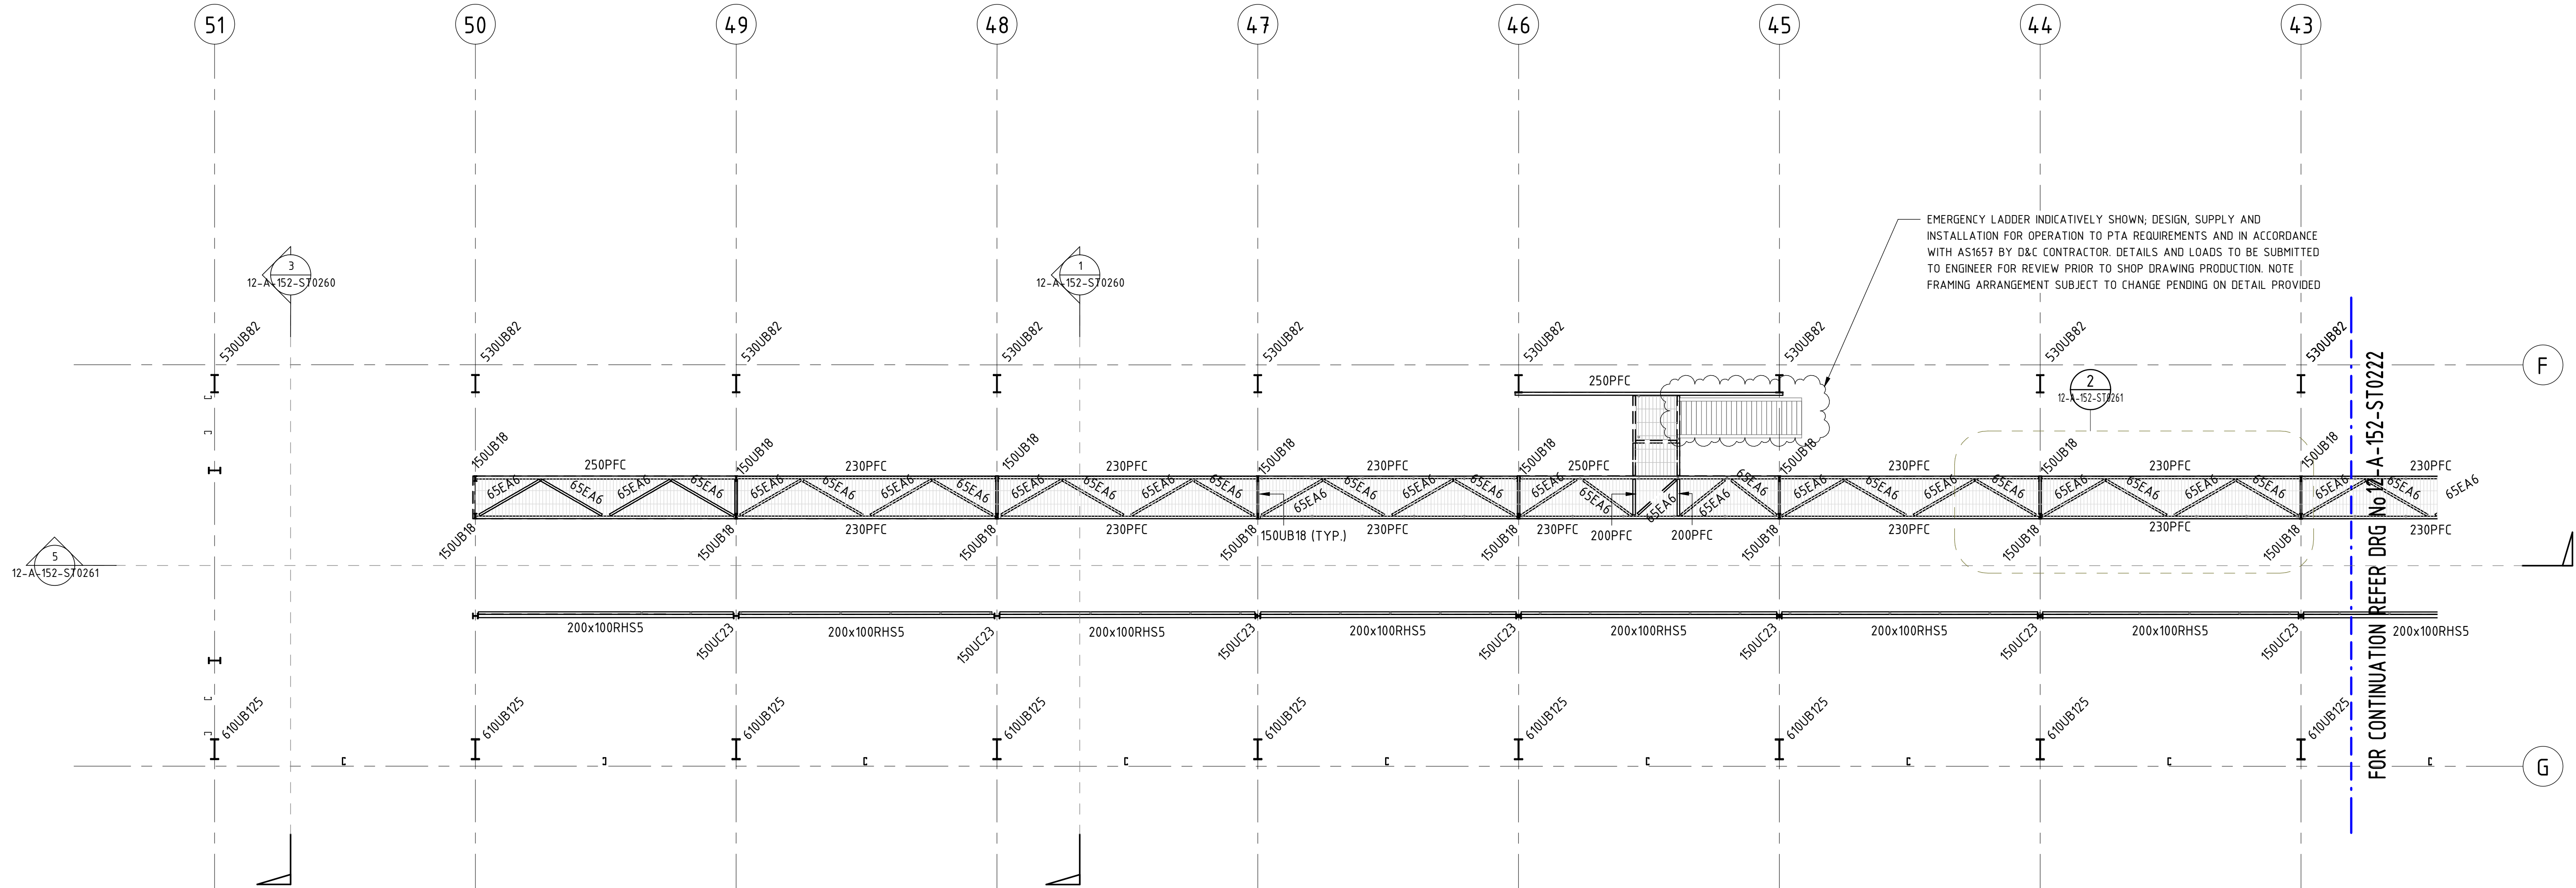


MEZZANINE STEELWORK PLAN (ZONE 1)
1 : 100

- USE OF THESE DRAWINGS**
1. THIS DRAWING SHALL BE READ IN CONJUNCTION WITH THE DISCIPLINE CONTRACT SPECIFICATION AND OTHER PROJECT DOCUMENTS.
 2. DRAWINGS AND DESIGNS UNDERTAKEN BY A SHOP DETAILER SHALL BE PRESENTED TO THE PTA FOR REVIEW AND CONCURRENCE THAT THE DESIGN INTENT HAS BEEN ACHIEVED.
 3. THE CONTRACTORS SHALL BE FULLY AWARE OF THE OTHER INTERFACING PACKAGES AND SHALL HAVE DEEMED TO HAVE INCLUDED INTER-TRADE INTERFACES. THE INTERFACES IDENTIFIED IN THE DOCUMENTATION ARE TO INDICATE AN INTENT AND ARE NOT INTENDED TO BE EXHAUSTIVE. MAKE ALLOWANCES AS REQUIRED.

ISSUED FOR CONSTRUCTION

								 www.aurecongroup.com 505695-0000-DRG-ST-1451				REFERENCES		SCALE : As indicated (@ A1) DATUM : HORIZONTAL: PCG94 VERTICAL: AHD71 PTA ACCEPTANCE STAMP		DESIGNED J.SPANO		 Government of Western Australia Public Transport Authority DETAILED DESIGN FOR THE BELLEVUE DEPOT HV TESTING FACILITY STRUCTURAL ELEVATED PLATFORM PLAN - ZONE 01 PTA Drawing No: 12-A-152-ST0221 REV : 0			
DRAWN A.DAWSON																					
CHECKED M.PEARCE																					
APPROVED FOR ISSUE																					
G.BENTLEY																					
DATE																					

--	--	

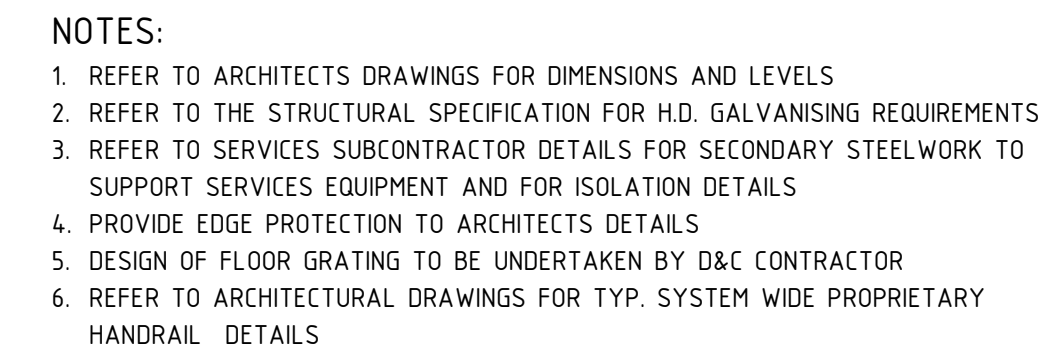

ZONE PLAN

1. DO NO SCALE DRAWINGS. WRITTEN DIMENSIONS GOVERN.
2. ALL DIMENSIONS ARE IN MILLIMETRES UNLESS NOTED OTHERWISE
3. ALL DIMENSIONS SHALL BE VERIFIED ON SITE BEFORE PROCEEDING WITH THE WORK. RELEVANT PARTY SHALL BE NOTIFIED IN WRITING OF ANY DISCREPANCIES.
4. THIS DRAWING MUST BE READ IN CONJUNCTION WITH ALL RELEVANT CONTRACTS, SPECIFICATIONS, REPORTS AND DRAWINGS.



1 : 100

1. THIS DRAWING SHALL BE READ IN CONJUNCTION WITH THE DISCIPLINE CONTRACT SPECIFICATION AND OTHER PROJECT DOCUMENTS.
2. DRAWINGS AND DESIGNS UNDERTAKEN BY A SHOP DETAILER SHALL BE PRESENTED TO THE PTA FOR REVIEW AND CONCURRENCE THAT THE DESIGN INTENT HAS BEEN ACHIEVED.
3. THE CONTRACTORS SHALL BE FULLY AWARE OF THE OTHER INTERFACING PACKAGES AND SHALL HAVE DEEMED TO HAVE INCLUDED INTER-TRADE INTERFACES. THE INTERFACES IDENTIFIED IN THE DOCUMENTATION ARE TO INDICATE AN INTENT AND ARE NOT INTENDED TO BE EXHAUSTIVE. MAKE ALLOWANCES AS REQUIRED.

ISSUED FOR CONSTRUCTION



HV TESTING FACILITY
STRUCTURAL
ELEVATED PLATFORM PLAN - ZONE 02

PTA Drawing No: 12-A-152-ST0222	REV : 0
---------------------------------	---------

[illegible]


505695-0000-DRG-ST-1452

REFERENCES


SCALE :	As indicated (@ A1)
DATUM :	HORIZONTAL: PCG94 VERTICAL: AHD71

PTA ACCEPTANCE STAMP


DESIGNED	J.SPANO
DRAWN	A.DAWSON
CHECKED	M.PEARCE
APPROVED FOR ISSUE	
G.BENTLEY	
DATE	

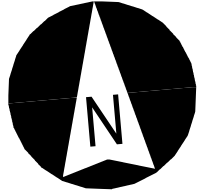

- NOTES:
1. REFER TO ARCHITECTS DRAWINGS FOR DIMENSIONS AND LEVELS
 2. REFER TO THE STRUCTURAL SPECIFICATION FOR H.D. GALVANISING REQUIREMENTS
 3. REFER TO SERVICES SUBCONTRACTOR DETAILS FOR SECONDARY STEELWORK TO SUPPORT SERVICES EQUIPMENT AND FOR ISOLATION DETAILS
 4. PROVIDE EDGE PROTECTION TO ARCHITECTS DETAILS
 5. DESIGN OF FLOOR GRATING TO BE UNDERTAKEN BY D&C CONTRACTOR
 6. REFER TO ARCHITECTURAL DRAWINGS FOR TYP. SYSTEM WIDE PROPRIETARY HANDRAIL DETAILS

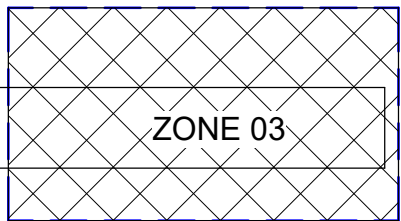

- ZONE PLAN**
- NOTES:
1. DO NO SCALE DRAWINGS. WRITTEN DIMENSIONS GOVERN.
 2. ALL DIMENSIONS ARE IN MILLIMETRES UNLESS NOTED OTHERWISE
 3. ALL DIMENSIONS SHALL BE VERIFIED ON SITE BEFORE PROCEEDING WITH THE WORK. RELEVANT PARTY SHALL BE NOTIFIED IN WRITING OF ANY DISCREPANCIES.
 4. THIS DRAWING MUST BE READ IN CONJUNCTION WITH ALL RELEVANT CONTRACTS, SPECIFICATIONS, REPORTS AND DRAWINGS.

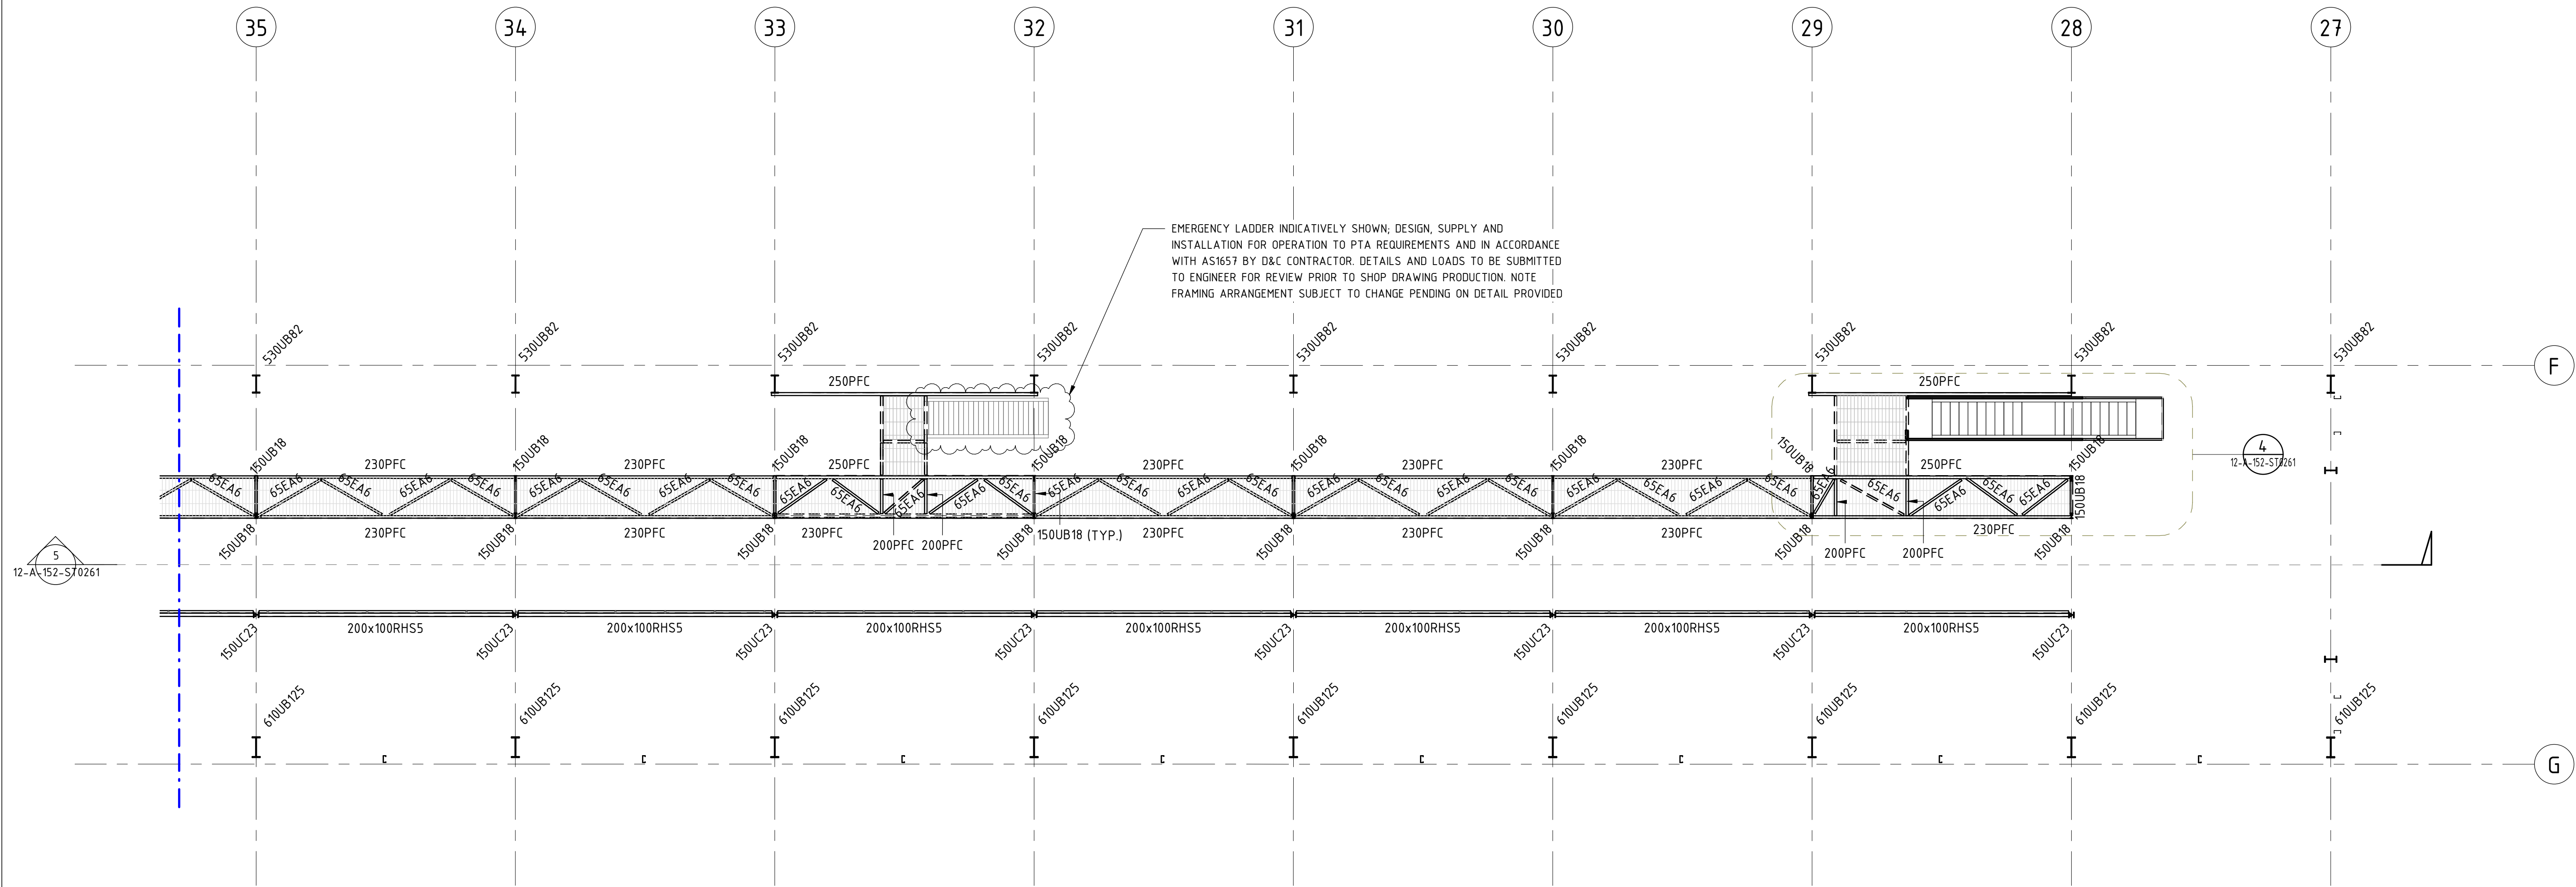


MEZZANINE STEELWORK PLAN (ZONE 3)
1 : 100

- USE OF THESE DRAWINGS**
1. THIS DRAWING SHALL BE READ IN CONJUNCTION WITH THE DISCIPLINE CONTRACT SPECIFICATION AND OTHER PROJECT DOCUMENTS
 2. DRAWINGS AND DESIGNS UNDERTAKEN BY A SHOP DETAILER SHALL BE PRESENTED TO THE PTA FOR REVIEW AND CONCURRENCE THAT THE DESIGN INTENT HAS BEEN ACHIEVED.
 3. THE CONTRACTORS SHALL BE FULLY AWARE OF THE OTHER INTERFACING PACKAGES AND SHALL HAVE DEEMED TO HAVE INCLUDED INTER-TRADE INTERFACES. THE INTERFACES IDENTIFIED IN THE DOCUMENTATION ARE TO INDICATE AN INTENT AND ARE NOT INTENDED TO BE EXHAUSTIVE. MAKE ALLOWANCES AS REQUIRED.

ISSUED FOR CONSTRUCTION

										 www.aurecongroup.com 505695-0000-DRG-ST-1453				REFERENCES		SCALE :		DESIGNED J.SPANO		 Government of Western Australia Public Transport Authority DETAILED DESIGN FOR THE BELLEVUE DEPOT HV TESTING FACILITY STRUCTURAL ELEVATED PLATFORM PLAN - ZONE 03 PTA Drawing No: 12-A-152-ST0223 REV : 0	
As indicated (@ A1)		DRAWN A.DAWSON	
DATUM :		CHECKED M.PEARCE	
HORIZONTAL: PCG94		APPROVED FOR ISSUE	
VERTICAL: AHD71	
PTA ACCEPTANCE STAMP		G.BENTLEY	
DATE	

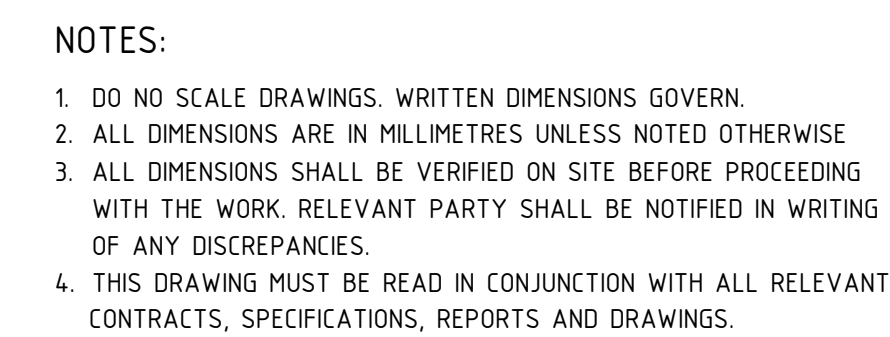

NOTES:

ZONE PLAN

1. DO NO SCALE DRAWINGS. WRITTEN DIMENSIONS GOVERN.
2. ALL DIMENSIONS ARE IN MILLIMETRES UNLESS NOTED OTHERWISE.
3. ALL DIMENSIONS SHALL BE VERIFIED ON SITE BEFORE PROCEEDING WITH THE WORK. RELEVANT PARTY SHALL BE NOTIFIED IN WRITING OF ANY DISCREPANCIES.
4. THIS DRAWING MUST BE READ IN CONJUNCTION WITH ALL RELEVANT CONTRACTS, SPECIFICATIONS, REPORTS AND DRAWINGS.




USE OF THESE DRAWINGS

1. THIS DRAWING SHALL BE READ IN CONJUNCTION WITH THE DISCIPLINE CONTRACT SPECIFICATION AND OTHER PROJECT DOCUMENTS.
2. DRAWINGS AND DESIGNS UNDERTAKEN BY A SHOP DETAILER SHALL BE PRESENTED TO THE PTA FOR REVIEW AND CONCURRENCE THAT THE DESIGN INTENT HAS BEEN ACHIEVED.
3. THE CONTRACTORS SHALL BE FULLY AWARE OF THE OTHER INTERFACING PACKAGES AND SHALL HAVE DEMAED TO HAVE INCLUDED INTER-TRADE INTERFACES. THE INTERFACES IDENTIFIED IN THE DOCUMENTATION ARE TO INDICATE AN INTENT AND ARE NOT INTENDED TO BE EXHAUSTIVE. MAKE ALLOWANCES AS REQUIRED.


ISSUED FOR CONSTRUCTION

Plot Date: 10/1/2019 9:25:34 AM Office: PERTH Filename: BIM 360://505695 - Bellevue Depot/505695-ST-BELLEVUE DEPOT-028.rvt

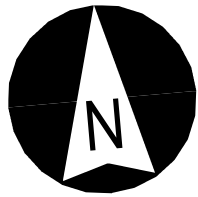

NOTES :


1. REFER TO ARCHITECT'S DRAWINGS FOR DIMENSIONS AND LEVELS
2. REFER TO 12-A-152-ST0022 TO ST0031 FOR STANDARD CONNECTIONS DETAILS
3. REFER TO THE STRUCTURAL SPECIFICATION FOR H.D. GALVANISING REQUIREMENTS
4. CONTRACTOR TO NOTE THAT THE MAIN WAREHOUSE FRAME ROOF BRACING IS DESIGNED TO FUNCTION IN THE PERMANENT WORKS CASE AS TENSION ONLY BRACES AND TO MAKE DUE ALLOWANCE WHEN CONSIDERING TEMPORARY WORKS REQUIREMENTS FOR SAFE ERECTION
5. BRIDGING REQUIREMENTS AS NOTED ON PLANS, REFER TO MANUFACTURES SPECIFICATION
6. GIRTS AND PURLINS TO BE PROVIDED WITH A MINIMUM ZINC COATING CLASS OF Z450
8. PROVIDE A 50x50x3 COLD FORMED ANGLE TRIMMER BETWEEN ALL PURLINS AT ROO HIP, VALLEY AND PENETRATION LOCATIONS TO SUPPORT CUT EDGES OF ROOF SHEETING
9. REFER TO SERVICES SUBCONTRACTOR DETAILS FOR SECONDARY STEELWORK TO SUPPORT SERVICES EQUIPMENT AND ISOLATION DETAILS
10. PROVIDE EDGE PROTECTION TO ARCHITECTS DETAILS

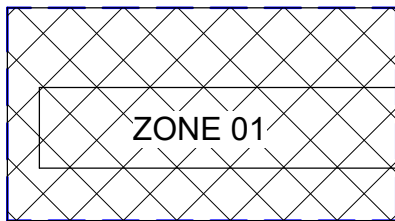

ZONE PLAN

NOTES:

1. DO NO SCALE DRAWINGS. WRITTEN DIMENSIONS GOVERN.
2. ALL DIMENSIONS ARE IN MILLIMETRES UNLESS NOTED OTHERWISE
3. ALL DIMENSIONS SHALL BE VERIFIED ON SITE BEFORE PROCEEDING WITH THE WORK. RELEVANT PARTY SHALL BE NOTIFIED IN WRITING OF ANY DISCREPANCIES.
4. THIS DRAWING MUST BE READ IN CONJUNCTION WITH ALL RELEVANT CONTRACTS, SPECIFICATIONS, REPORTS AND DRAWINGS.

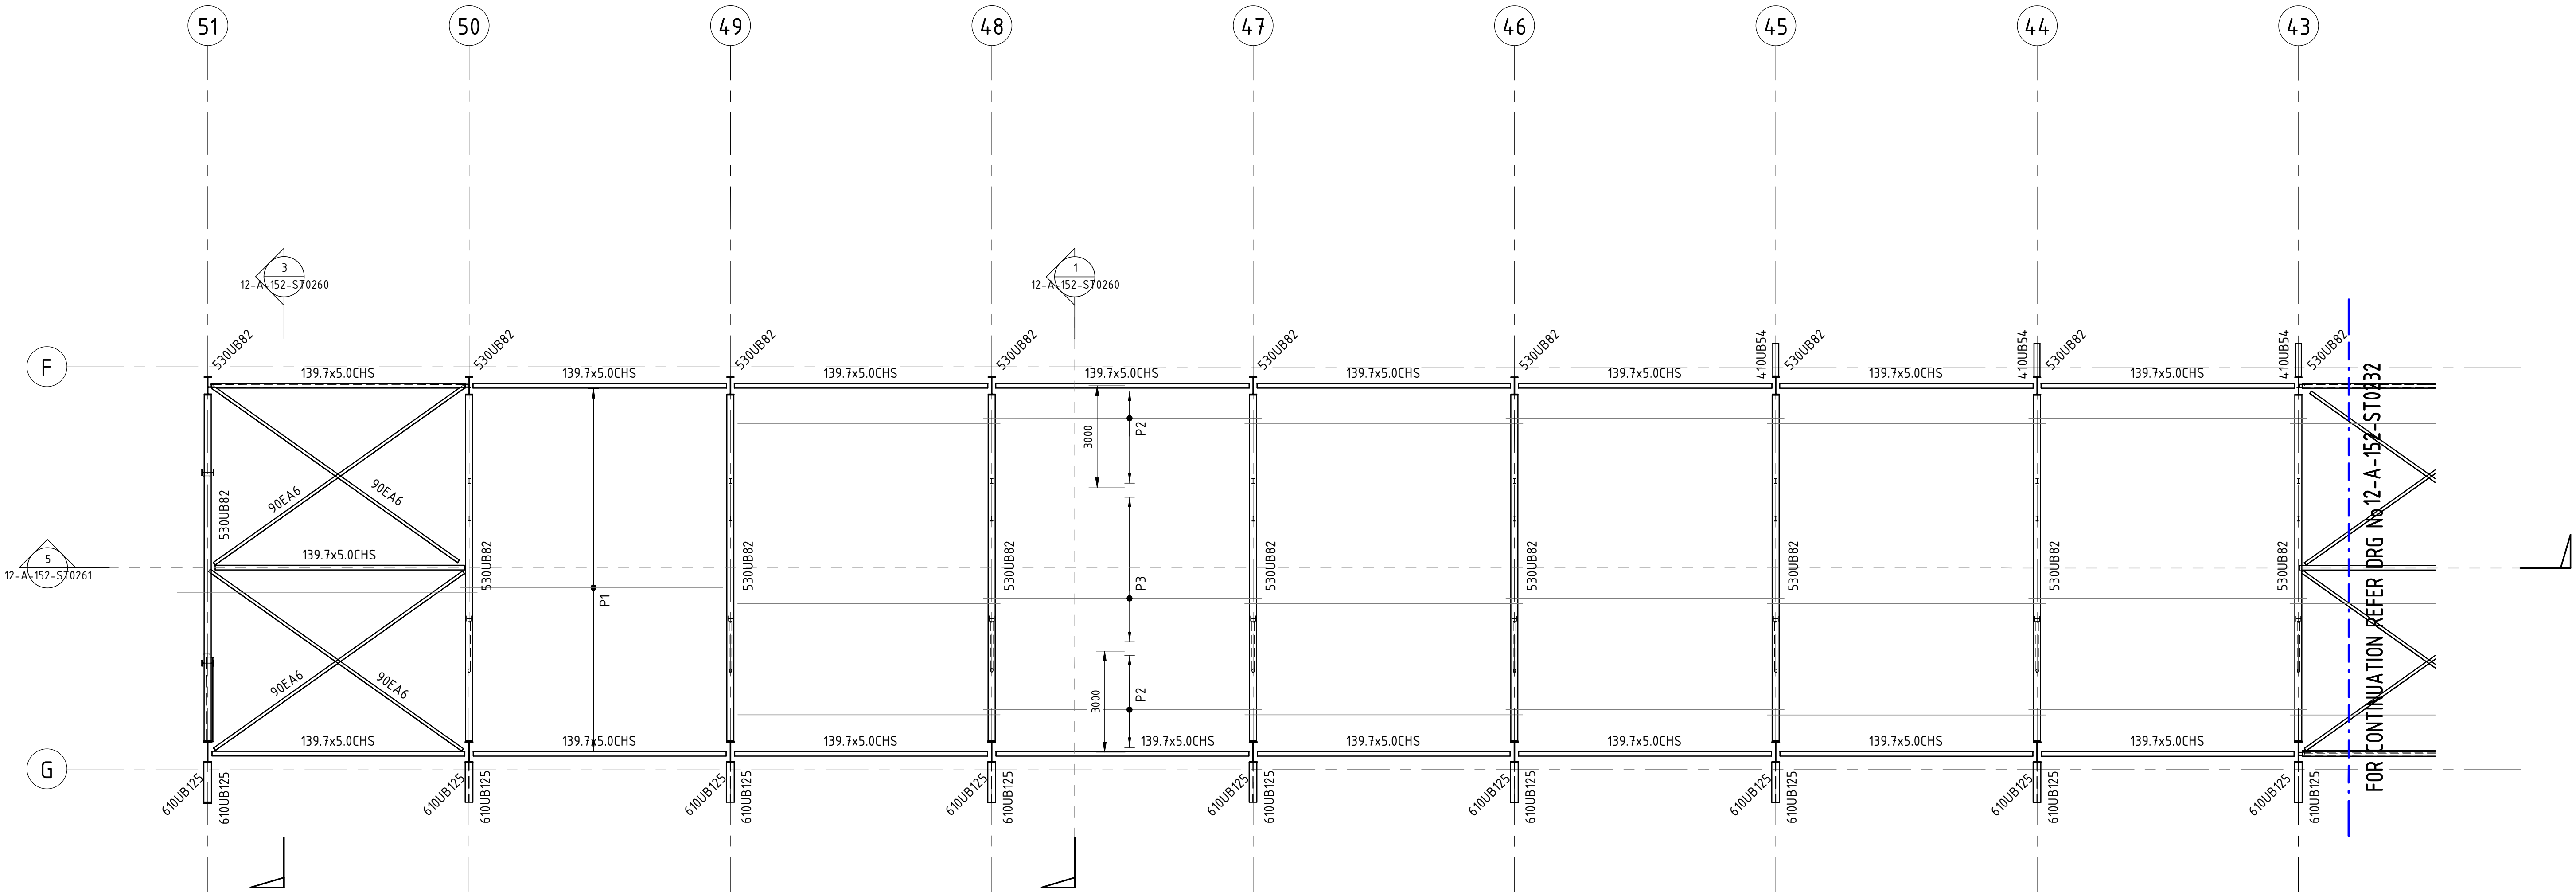

PURLIN SCHEDULE

TAG	MEMBER	COMMENTS
P1	Z20024 AT 600 CTS	1 ROW OF BRIDGING (MIN 2 LAPPED SPANS)
P2	Z20024 AT 1200 CTS	1 ROW OF BRIDGING (MIN 4 LAPPED SPANS)
P3	Z20024 AT 1500 CTS	1 ROW OF BRIDGING (MIN 4 LAPPED SPANS)

NOTES:

1. PURLINS/GIRTS TO BE LAPPED WHERE SHOWN. LAP LENGTH TO BE AS PER MANUFACTURER'S RECOMMENDATIONS (MIN 15% OF SPAN).
2. PURLINS/GIRTS TO BE PROVIDED WITH MIN 1 MIDSPAN BRIDGING FOR ALL SPANS ABOVE 4m (U.N.O).

OVERALL ROOF PLAN (ZONE 1)

1 : 100

USE OF THESE DRAWINGS

1. THIS DRAWING SHALL BE READ IN CONJUNCTION WITH THE DISCIPLINE CONTRACT SPECIFICATION AND OTHER PROJECT DOCUMENTS.
2. DRAWINGS AND DESIGNS UNDERTAKEN BY A SHOP DETAILER SHALL BE PRESENTED TO THE PTA FOR REVIEW AND CONCURRENCE THAT THE DESIGN INTENT HAS BEEN ACHIEVED.
3. THE CONTRACTORS SHALL BE FULLY AWARE OF THE OTHER INTERFACING PACKAGES AND SHALL HAVE DEEMED TO HAVE INCLUDED INTER-TRADE INTERFACES. THE INTERFACES IDENTIFIED IN THE DOCUMENTATION ARE TO INDICATE AN INTENT AND ARE NOT INTENDED TO BE EXHAUSTIVE. MAKE ALLOWANCES AS REQUIRED.

ISSUED FOR CONSTRUCTION

REV	DATE	ISSUED FOR CONSTRUCTION	AMENDMENT	DSN	DRN	CHKD	APP
0	01.10.19	ISSUED FOR CONSTRUCTION		J.S.	A.C.D.	M.P.	G.B.
1	01.10.19	ISSUED FOR CONSTRUCTION		J.S.	A.C.D.	M.P.	G.B.
aurecon
www.aurecongroup.com

505695-0000-DRG-ST-1555

REFERENCES

SCALE :
As indicated (@ A1)
DATUM :
HORIZONTAL: PC694
VERTICAL: AHD71
PTA ACCEPTANCE STAMP

DESIGNED J.SPANO
DRAWN A.DAWSON
CHECKED M.PEARCE
APPROVED FOR ISSUE
G.BENTLEY
DATE

Government of Western Australia
Public Transport Authority
DETAILED DESIGN FOR THE BELLEVUE DEPOT
HV TESTING FACILITY
STRUCTURAL
ROOF FRAMING PLAN - ZONE 01
PTA Drawing No: 12-A-152-ST0231
REV : 0



- NOTES:

- ## ZONE PLAN



1 : 100

PURLIN SCHEDULE

NOTES:

- ### USE OF THESE DRAWINGS

- ## ISSUED FOR CONSTRUCTION



Government of Western Australia
Public Transport Authority

DETAILED DESIGN FOR THE BELLEVUE DEPOT

HV TESTING FACILITY

STRUCTURAL

ROOF FRAMING PLAN - ZONE 02

PTA Drawing No: 12-A-152-ST0232

REV : 0



www.aurecongroup.com

505695-0000-DRG-ST-1556

REFERENCES

SCALE :

As indicated (@ A1)

DATUM :

HORIZONTAL: PCG94

VERTICAL: AHD71

PTA ACCEPTANCE STAMP

DESIGNED | SPANO


DRAWN A.DAWSON

CHECKED M.PEARCE

APPROVED FOR ISSUE


G BENTLEY

DATE _____

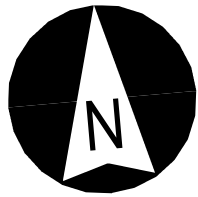

NOTES :


1. REFER TO ARCHITECT'S DRAWINGS FOR DIMENSIONS AND LEVELS
2. REFER TO 12-A-152-ST0022 TO ST0031 FOR STANDARD CONNECTIONS DETAILS
3. REFER TO THE STRUCTURAL SPECIFICATION FOR H.D. GALVANISING REQUIREMENTS
4. CONTRACTOR TO NOTE THAT THE MAIN WAREHOUSE FRAME ROOF BRACING IS DESIGNED TO FUNCTION IN THE PERMANENT WORKS CASE AS TENSION ONLY BRACES AND TO MAKE DUE ALLOWANCE WHEN CONSIDERING TEMPORARY WORKS REQUIREMENTS FOR SAFE ERECTION
5. BRIDGING REQUIREMENTS AS NOTED ON PLANS, REFER TO MANUFACTURES SPECIFICATION
6. GIRTS AND PURLINS TO BE PROVIDED WITH A MINIMUM ZINC COATING CLASS OF Z450
8. PROVIDE A 50x50x3 COLD FORMED ANGLE TRIMMER BETWEEN ALL PURLINS AT ROO HIP, VALLEY AND PENETRATION LOCATIONS TO SUPPORT CUT EDGES OF ROOF SHEETING
9. REFER TO SERVICES SUBCONTRACTOR DETAILS FOR SECONDARY STEELWORK TO SUPPORT SERVICES EQUIPMENT AND ISOLATION DETAILS
10. PROVIDE EDGE PROTECTION TO ARCHITECTS DETAILS

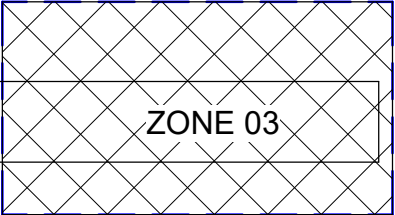

ZONE PLAN

NOTES:

1. DO NO SCALE DRAWINGS. WRITTEN DIMENSIONS GOVERN.
2. ALL DIMENSIONS ARE IN MILLIMETRES UNLESS NOTED OTHERWISE
3. ALL DIMENSIONS SHALL BE VERIFIED ON SITE BEFORE PROCEEDING WITH THE WORK. RELEVANT PARTY SHALL BE NOTIFIED IN WRITING OF ANY DISCREPANCIES.
4. THIS DRAWING MUST BE READ IN CONJUNCTION WITH ALL RELEVANT CONTRACTS, SPECIFICATIONS, REPORTS AND DRAWINGS.

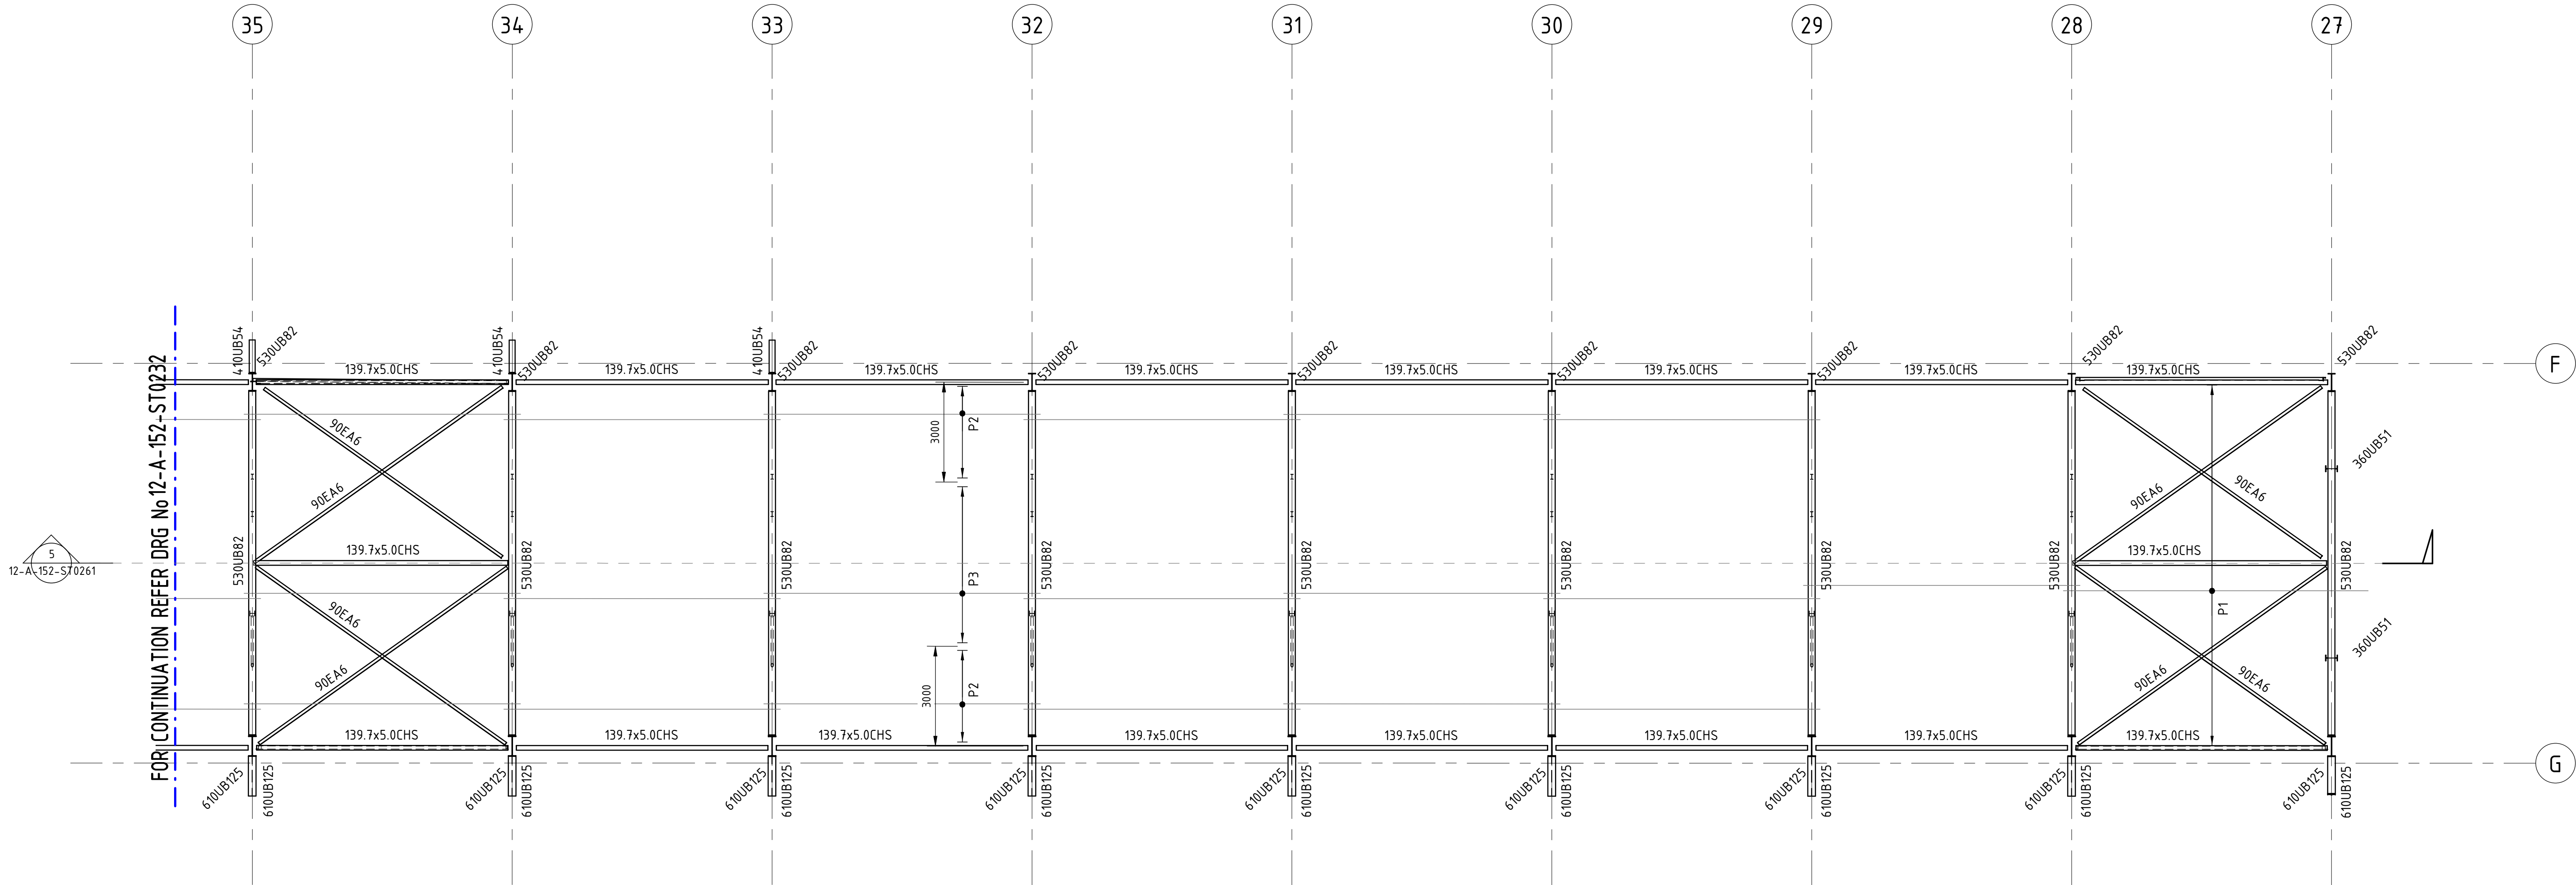

OVERALL ROOF PLAN (ZONE 3)

1 : 100

PURLIN SCHEDULE

TAG	MEMBER	COMMENTS
P1	Z20024 AT 600 CTS	1 ROW OF BRIDGING (MIN 2 LAPPED SPANS)
P2	Z20024 AT 1200 CTS	1 ROW OF BRIDGING (MIN 4 LAPPED SPANS)
P3	Z20024 AT 1500 CTS	1 ROW OF BRIDGING (MIN 4 LAPPED SPANS)

NOTES:

1. PURLINS/GIRTS TO BE LAPPED WHERE SHOWN LAP LENGTH TO BE AS PER MANUFACTURER'S RECOMMENDATIONS (MIN 15% OF SPAN).
2. PURLINS/GIRTS TO BE PROVIDED WITH MIN 1 MIDSPAN BRIDGING FOR ALL SPANS ABOVE 4m (U.N.O).

USE OF THESE DRAWINGS

1. THIS DRAWING SHALL BE READ IN CONJUNCTION WITH THE DISCIPLINE CONTRACT SPECIFICATION AND OTHER PROJECT DOCUMENTS.
2. DRAWINGS AND DESIGNS UNDERTAKEN BY A SHOP DETAILER SHALL BE PRESENTED TO THE PTA FOR REVIEW AND CONCURRENCE THAT THE DESIGN INTENT HAS BEEN ACHIEVED.
3. THE CONTRACTORS SHALL BE FULLY AWARE OF THE OTHER INTERFACING PACKAGES AND SHALL HAVE DEEMED TO HAVE INCLUDED INTER-TRADE INTERFACES. THE INTERFACES IDENTIFIED IN THE DOCUMENTATION ARE TO INDICATE AN INTENT AND ARE NOT INTENDED TO BE EXHAUSTIVE. MAKE ALLOWANCES AS REQUIRED.

ISSUED FOR CONSTRUCTION

REV	DATE	AMENDMENT	DSN	DRN	CHKD	APP
0	01.10.19	ISSUED FOR CONSTRUCTION	J.S.	A.C.D.	M.P.	G.B.
1	01.10.19	ISSUED FOR CONSTRUCTION	J.S.	A.C.D.	M.P.	G.B.
As indicated (@ A1)

DATUM :
HORIZONTAL: PCG94
VERTICAL: AHD71

PTA ACCEPTANCE STAMP

DESIGNED J.SPANO

DRAWN A.DAWSON

CHECKED M.PEARCE

APPROVED FOR ISSUE

G.BENTLEY

DATE



DETAILED DESIGN FOR THE BELLEVUE DEPOT

HV TESTING FACILITY

STRUCTURAL

ROOF FRAMING PLAN - ZONE 03

PTA Drawing No: 12-A-152-ST0233

REV : 0

ZONE 01	ZONE 02	ZONE 03
---------	---------	---------

- NOTES:
1.


DO NO SCALE DRAWINGS. WRITTEN DIMENSIONS GOVERN.
2.

ALL DIMENSIONS ARE IN MILLIMETRES UNLESS NOTED OTHERWISE
3.

ALL DIMENSIONS SHALL BE VERIFIED ON SITE BEFORE PROCEEDING WITH THE WORK. RELEVANT PARTY SHALL BE NOTIFIED IN WRITING OF ANY DISCREPANCIES.
4.

THIS DRAWING MUST BE READ IN CONJUNCTION WITH ALL RELEVANT CONTRACTS, SPECIFICATIONS, REPORTS AND DRAWINGS.

ZONE PLAN

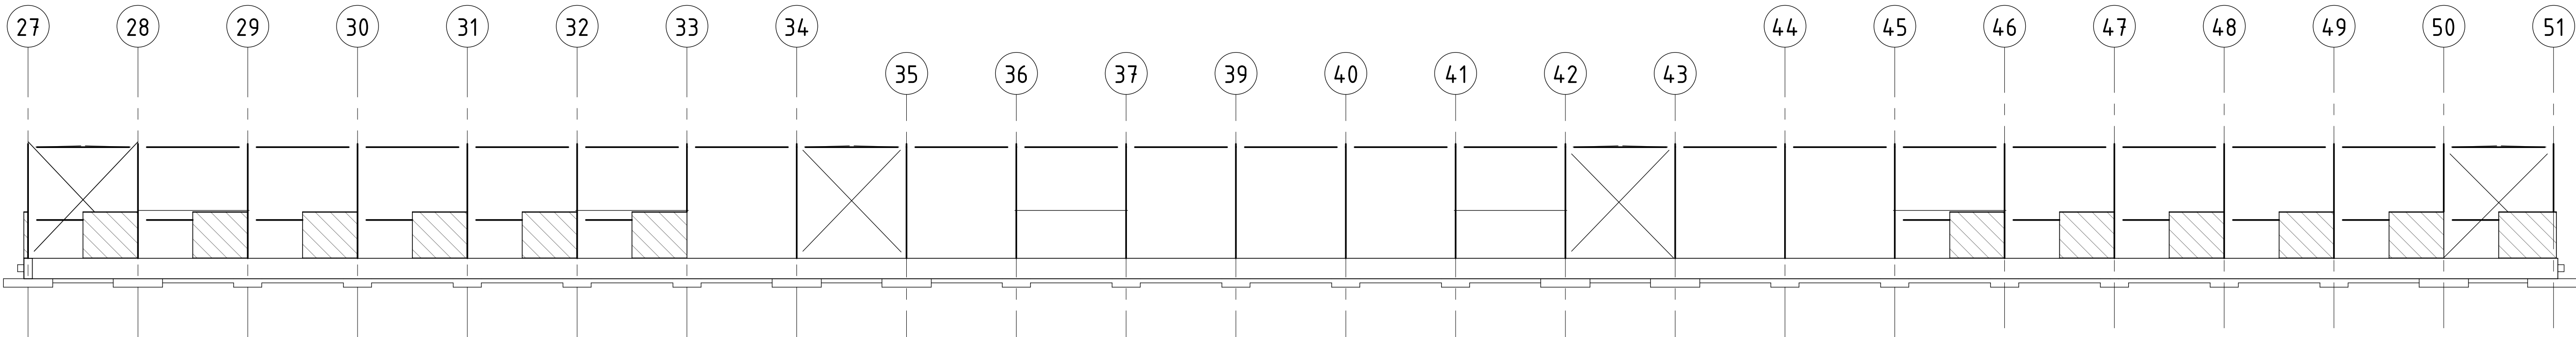

NORTH ELEVATION
1 : 250

- USE OF THESE DRAWINGS
1.


THIS DRAWING SHALL BE READ IN CONJUNCTION WITH THE DISCIPLINE CONTRACT SPECIFICATION AND OTHER PROJECT DOCUMENTS.
2.

DRAWINGS AND DESIGNS UNDERTAKEN BY A SHOP DETAILER SHALL BE PRESENTED TO THE PTA FOR REVIEW AND CONCURRENCE THAT THE DESIGN INTENT HAS BEEN ACHIEVED.
3.

THE CONTRACTORS SHALL BE FULLY AWARE OF THE OTHER INTERFACING PACKAGES AND SHALL HAVE DEEMED TO HAVE INCLUDED INTER-TRADE INTERFACES. THE INTERFACES IDENTIFIED IN THE DOCUMENTATION ARE TO INDICATE AN INTENT AND ARE NOT INTENDED TO BE EXHAUSTIVE. MAKE ALLOWANCES AS REQUIRED.

ISSUED FOR CONSTRUCTION

	</
--	--	----

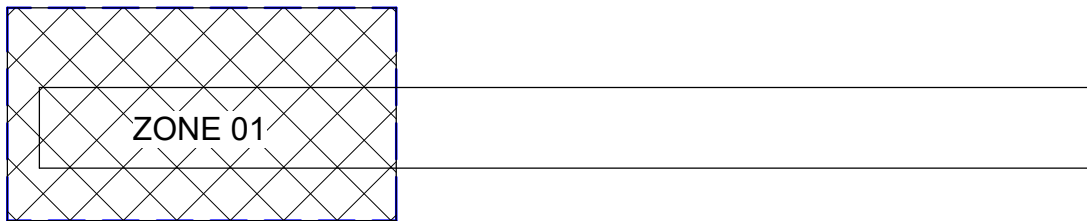

ZONE PLAN


NOTES:

- DO NO SCALE DRAWINGS. WRITTEN DIMENSIONS GOVERN.
- ALL DIMENSIONS ARE IN MILLIMETRES UNLESS NOTED OTHERWISE
- ALL DIMENSIONS SHALL BE VERIFIED ON SITE BEFORE PROCEEDING WITH THE WORK. RELEVANT PARTY SHALL BE NOTIFIED IN WRITING OF ANY DISCREPANCIES.
- THIS DRAWING MUST BE READ IN CONJUNCTION WITH ALL RELEVANT CONTRACTS, SPECIFICATIONS, REPORTS AND DRAWINGS.

NOTES:

- REFER TO ARCHITECTS DRAWINGS FOR DIMENSIONS AND LEVELS
- REFER TO 12-A-152-ST0022 TO ST0031 FOR STANDARD CONNECTIONS DETAILS
- REFER TO 12-A-152-ST0003 & ST0004 FOR STANDARD NOTES
- REFER TO THE STRUCTURAL SPECIFICATION FOR H.D. GALVANISING REQUIREMENTS
- CONTRACTOR TO NOTE THAT THE MAIN WAREHOUSE FRAME ROOF BRACING ARE DESIGNED TO FUNCTION IN THE PERMANENT WORKS CASE AS TENSION ONLY BRACES AND TO MAKE DUE ALLOWANCE WHEN CONSIDERING TEMPORARY WORKS REQUIREMENTS FOR SAFE ERECTION
- BRIDGING REQUIREMENTS AS NOTED ON PLANS, REFER TO MANUFACTURES' SPECIFICATIONS.
- GIRTS AND PURLINS TO BE PROVIDED WITH A MINIMUM ZINC COATING CLASS OF Z450
- PROVIDE A 50X50X3 COLD FORMED ANGLE TRIMMER BETWEEN ALL PURLINS AT ROOF HIP, VALLEY AND PENETRATION LOCATIONS TO SUPPORT CUT EDGES OF ROOF SHEETING
- REFER TO SERVICES SUBCONTRACTOR DETAILS FOR SECONDARY STEELWORK TO SUPPORT SERVICES EQUIPMENT AND FOR ISOLATION DETAILS
- PROVIDE EDGE PROTECTION TO ARCHITECTS DETAILS
- ALL DIMENSIONS TO PRECAST PANELS ARE NOMINAL ONLY AND SHOULD BE REFERENCED WITH THE ARCHITECTS DRAWINGS. THESE SHALL BE CONFIRMED WITH THE PRECAST CONTRACTOR
- REFER TO THE ARCHITECTS DRAWINGS FOR REBATES, CHAMFERS, DRIPS, SEALS, BAFFLES, ETC. AND EXTENT OF FINISHES
- DOWEL TUBE SPACING ON PRECAST SHOP DRAWINGS SHALL INCORPORATE THE SURVEYED AS BUILT SETOUT OF DOWELS
- IT IS THE CONTRACTORS RESPONSIBILITY TO CO-ORDINATE ALL PENETRATIONS FOR SERVICES ETC. ALL PENETRATIONS SHALL BE SHOWN ON SHOP DRAWINGS FOR APPROVAL PRIOR TO FABRICATION OF ANY PANEL
- REFER TO THE ARCHITECTS DRAWINGS FOR ALL JOINTING DETAILS

REFER TO 12-A-152-ST0274 FOR PRECAST DETAILS

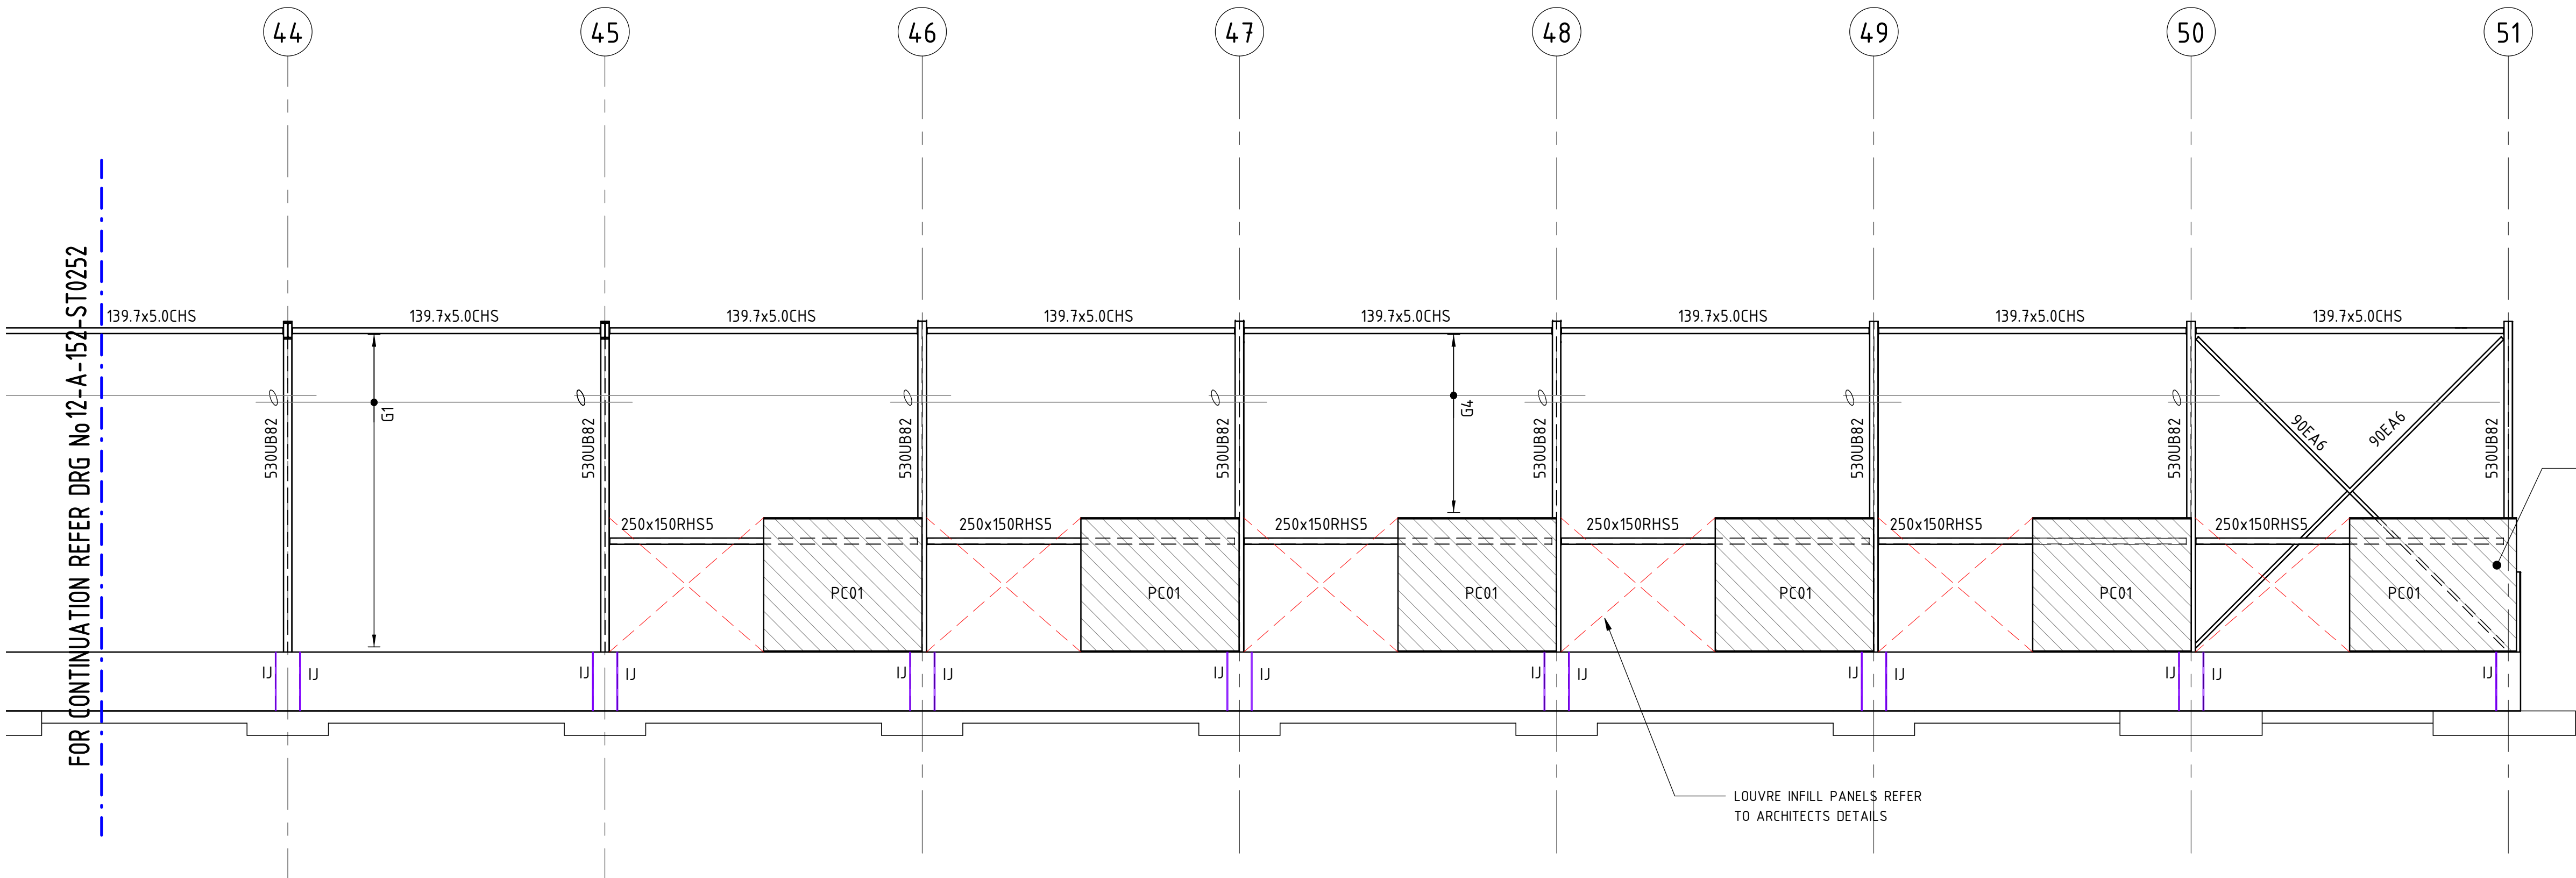

NORTH ELEVATION (ZONE 1)

1 : 100

GIRT SCHEDULE

TAG	MEMBER	COMMENTS
G1	Z20024 AT 1200 CTS	1 ROW OF BRIDGING (MIN 4 LAPPED SPANS)
G2	Z20019 AT 1200CTS	(SINGLE SPAN)
G3	Z20019 AT 600CTS	(SINGLE SPAN)
G4	Z20019 AT 600CTS	MIN 4 LAPPED SPANS

NOTES:

- PURLINS/GIRTS TO BE LAPPED WHERE SHOWN. LAP LENGTH TO BE AS PER MANUFACTURER'S RECOMMENDATIONS (MIN 15% OF SPAN).
- PURLINS/GIRTS TO BE PROVIDED WITH MIN 1 MIDSPAN BRIDGING FOR ALL SPANS ABOVE 4m (U.N.O).
- PROVIDE GIRT HANGERS/SAG RODS/BRIDGING TO MANUFACTURERS DETAILS

USE OF THESE DRAWINGS

- THIS DRAWING SHALL BE READ IN CONJUNCTION WITH THE DISCIPLINE CONTRACT SPECIFICATION AND OTHER PROJECT DOCUMENTS.
- DRAWINGS AND DESIGNS UNDERTAKEN BY A SHOP DETAILER SHALL BE PRESENTED TO THE PTA FOR REVIEW AND CONCURRENCE THAT THE DESIGN INTENT HAS BEEN ACHIEVED.
- THE CONTRACTORS SHALL BE FULLY AWARE OF THE OTHER INTERFACING PACKAGES AND SHALL HAVE DEEMED TO HAVE INCLUDED INTER-TRADE INTERFACES. THE INTERFACES IDENTIFIED IN THE DOCUMENTATION ARE TO INDICATE AN INTENT AND ARE NOT INTENDED TO BE EXHAUSTIVE. MAKE ALLOWANCES AS REQUIRED.

ISSUED FOR CONSTRUCTION

REV	DATE	AMENDMENT	DSN	DRN	CHKD	APP
0	01.10.19	ISSUED FOR CONSTRUCTION	J.S.	A.C.D.	M.P.	G.B.
1	01.10.19	ISSUED FOR CONSTRUCTION	J.S.	A.C.D.	M.P.	G.B.
505695-0000-DRG-ST-1634

REFERENCES

SCALE :
As indicated (@ A1)
DATUM :
HORIZONTAL: PCG94
VERTICAL: AHD71
PTA ACCEPTANCE STAMP

DESIGNED J.SPANO
DRAWN A.DAWSON
CHECKED M.PEARCE
APPROVED FOR ISSUE
G.BENTLEY
DATE



DETAILED DESIGN FOR THE BELLEVUE DEPOT


HV TESTING FACILITY

STRUCTURAL

NORTH ELEVATION - ZONE 01

PTA Drawing No: 12-A-152-ST0251

REV : 0

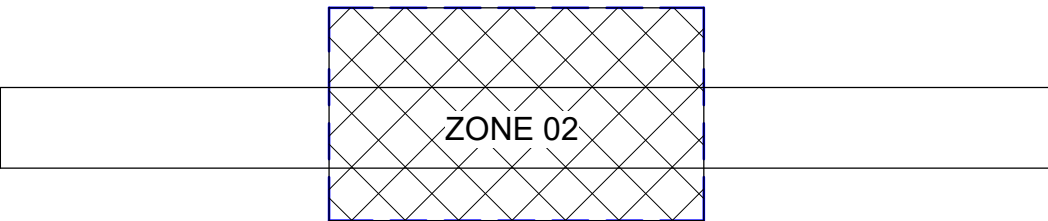


ZONE PLAN

NOTES:

- 1. DO NO SCALE DRAWINGS. WRITTEN DIMENSIONS GOVERN.
- 2. ALL DIMENSIONS ARE IN MILLIMETRES UNLESS NOTED OTHERWISE
- 3. ALL DIMENSIONS SHALL BE VERIFIED ON SITE BEFORE PROCEEDING WITH THE WORK. RELEVANT PARTY SHALL BE NOTIFIED IN WRITING OF ANY DISCREPANCIES.
- 4. THIS DRAWING MUST BE READ IN CONJUNCTION WITH ALL RELEVANT CONTRACTS, SPECIFICATIONS, REPORTS AND DRAWINGS.

NOTES:

- 1. REFER TO ARCHITECTS DRAWINGS FOR DIMENSIONS AND LEVELS
- 2. REFER TO 12-A-152-ST0022 TO ST0031 FOR STANDARD CONNECTIONS DETAILS
- 3. REFER TO 12-A-152-ST0003 & ST0004 FOR STANDARD NOTES
- 4. REFER TO THE STRUCTURAL SPECIFICATION FOR H.D. GALVANISING REQUIREMENTS
- 5. CONTRACTOR TO NOTE THAT THE MAIN WAREHOUSE FRAME ROOF BRACING ARE DESIGNED TO FUNCTION IN THE PERMANENT WORKS CASE AS TENSION ONLY BRACES AND TO MAKE DUE ALLOWANCE WHEN CONSIDERING TEMPORARY WORKS REQUIREMENTS FOR SAFE ERECTION
- 6. BRIDGING REQUIREMENTS AS NOTED ON PLANS, REFER TO MANUFACTURES' SPECIFICATIONS.
- 7. GIRTS AND PURLINS TO BE PROVIDED WITH A MINIMUM ZINC COATING CLASS OF Z450
- 8. PROVIDE A 50X50X3 COLD FORMED ANGLE TRIMMER BETWEEN ALL PURLINS AT ROOF HIP, VALLEY AND PENETRATION LOCATIONS TO SUPPORT CUT EDGES OF ROOF SHEETING
- 9. REFER TO SERVICES SUBCONTRACTOR DETAILS FOR SECONDARY STEELWORK TO SUPPORT SERVICES EQUIPMENT AND FOR ISOLATION DETAILS
- 10. PROVIDE EDGE PROTECTION TO ARCHITECTS DETAILS
- 11. ALL DIMENSIONS TO PRECAST PANELS ARE NOMINAL ONLY AND SHOULD BE REFERENCED WITH THE ARCHITECTS DRAWINGS. THESE SHALL BE CONFIRMED WITH THE PRECAST CONTRACTOR
- 12. REFER TO THE ARCHITECTS DRAWINGS FOR REBATES, CHAMFERS, DRIPS, SEALS, BAFFLES, ETC. AND EXTENT OF FINISHES
- 13. DOWEL TUBE SPACING ON PRECAST SHOP DRAWINGS SHALL INCORPORATE THE SURVEYED AS BUILT SETOUT OF DOWELS
- 14. IT IS THE CONTRACTORS RESPONSIBILITY TO CO-ORDINATE ALL PENETRATIONS FOR SERVICES ETC. ALL PENETRATIONS SHALL BE SHOWN ON SHOP DRAWINGS FOR APPROVAL PRIOR TO FABRICATION OF ANY PANEL
- 15. REFER TO THE ARCHITECTS DRAWINGS FOR ALL JOINTING DETAILS

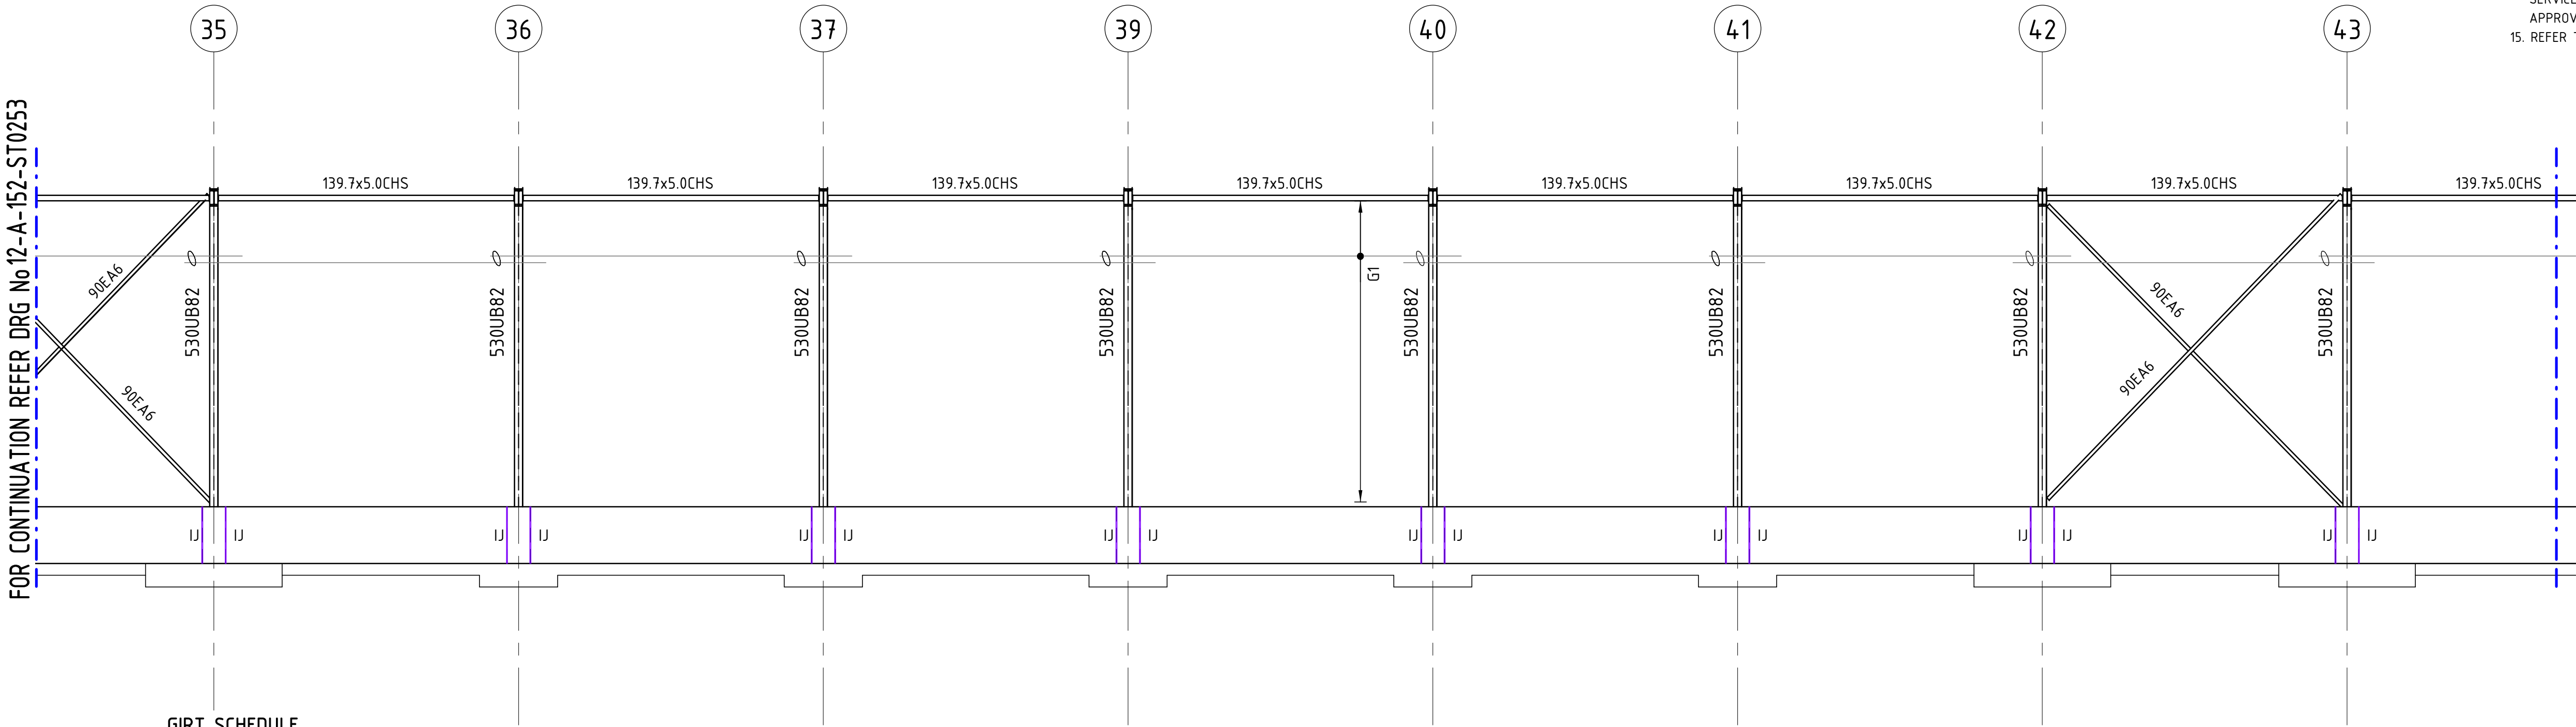

GIRT SCHEDULE

TAG	MEMBER	COMMENTS
G1	Z20024 AT 1200 CTS	1 ROW OF BRIDGING (MIN 4 LAPPED SPANS)
G2	Z20019 AT 1200CTS	(SINGLE SPAN)
G3	Z20019 AT 600CTS	(SINGLE SPAN)
G4	Z20019 AT 600CTS	MIN 4 LAPPED SPANS

NOTES:

- 1. PURLINS/GIRTS TO BE LAPPED WHERE SHOWN. LAP LENGTH TO BE AS PER MANUFACTURER'S RECOMMENDATIONS (MIN 15% OF SPAN).
- 2. PURLINS/GIRTS TO BE PROVIDED WITH MIN 1 MIDSPAN BRIDGING FOR ALL SPANS ABOVE 4m (U.N.O).
- 3. PROVIDE GIRT HANGERS/SAG RODS/BRIDGING TO MANUFACTURERS DETAILS

USE OF THESE DRAWINGS

- 1. THIS DRAWING SHALL BE READ IN CONJUNCTION WITH THE DISCIPLINE CONTRACT SPECIFICATION AND OTHER PROJECT DOCUMENTS.
- 2. DRAWINGS AND DESIGNS UNDERTAKEN BY A SHOP DETAILER SHALL BE PRESENTED TO THE PTA FOR REVIEW AND CONCURRENCE THAT THE DESIGN INTENT HAS BEEN ACHIEVED.
- 3. THE CONTRACTORS SHALL BE FULLY AWARE OF THE OTHER INTERFACING PACKAGES AND SHALL HAVE DEEMED TO HAVE INCLUDED INTER-TRADE INTERFACES. THE INTERFACES IDENTIFIED IN THE DOCUMENTATION ARE TO INDICATE AN INTENT AND ARE NOT INTENDED TO BE EXHAUSTIVE. MAKE ALLOWANCES AS REQUIRED.

ISSUED FOR CONSTRUCTION

REV	DATE	AMENDMENT	DSN	DRN	CHKD	APP
0	01.10.19	ISSUED FOR CONSTRUCTION	J.S.	A.C.D.	M.P.	G.B.
1	01.10.19	ISSUED FOR CONSTRUCTION	J.S.	A.C.D.	M.P.	G.B.
505695-0000-DRG-ST-1635

REFERENCES

SCALE :
As indicated (@ A1)
DATUM :
HORIZONTAL: PCG94
VERTICAL: AHD71
PTA ACCEPTANCE STAMP

DESIGNED J.SPANO
DRAWN A.DAWSON
CHECKED M.PEARCE
APPROVED FOR ISSUE
G.BENTLEY
DATE



DETAILED DESIGN FOR THE BELLEVUE DEPOT

HV TESTING FACILITY

STRUCTURAL

NORTH ELEVATION - ZONE 02

PTA Drawing No: 12-A-152-ST0252

REV : 0

ZONE 03

NOTES:

- NOTES:

- GIRT SCHEDULE

NORTH ELEVATION (ZONE 3)
1 : 100

NOTES:

- ### USE OF THESE DRAWINGS

- ISSUED FOR CONSTRUCTION

DETAILED DESIGN FOR THE BELLEVUE DEPOT

STRUCTURAL

PTA Drawing No: 12-A-152-ST0253

REV : 0



aurecon
www.aurecongroup.com

www.aurecongroup.com

505695-0000-DRG-ST-1636

REFERENCES

SCALE :

As indicated (@ A1)

DATUM :

HORIZONTAL : PCG94

VERTICAL: AHD71

PTA ACCEPTANCE STAMP

DESIGNED | SPANO

DRAWN A.DAWSUN

CHECKED M.PEARCE

APPROVED FOR ISSUE

G BENTLEY

DATE _____

ZONE 01	ZONE 02	ZONE 03
---------	---------	---------

- NOTES:
1.


DO NO SCALE DRAWINGS. WRITTEN DIMENSIONS GOVERN.
2.

ALL DIMENSIONS ARE IN MILLIMETRES UNLESS NOTED OTHERWISE
3.

ALL DIMENSIONS SHALL BE VERIFIED ON SITE BEFORE PROCEEDING WITH THE WORK. RELEVANT PARTY SHALL BE NOTIFIED IN WRITING OF ANY DISCREPANCIES.
4.

THIS DRAWING MUST BE READ IN CONJUNCTION WITH ALL RELEVANT CONTRACTS, SPECIFICATIONS, REPORTS AND DRAWINGS.

ZONE PLAN

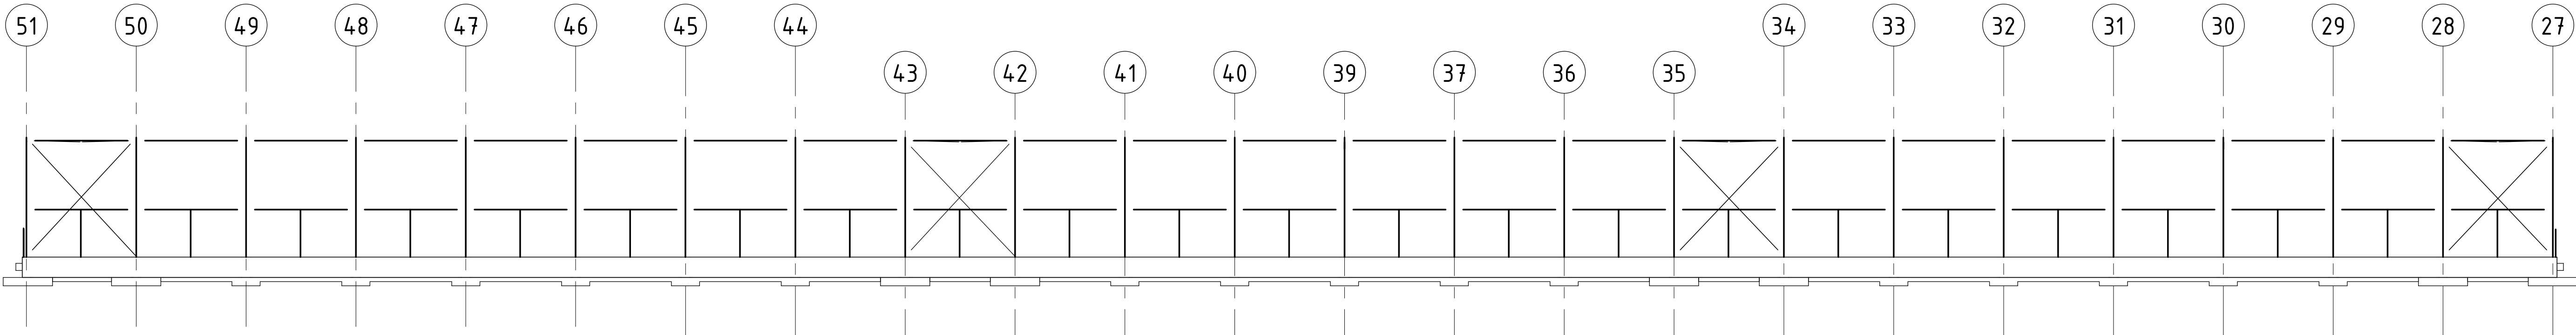

SOUTH ELEVATION
1 : 250

- USE OF THESE DRAWINGS
1.

THIS DRAWING SHALL BE READ IN CONJUNCTION WITH THE DISCIPLINE CONTRACT SPECIFICATION AND OTHER PROJECT DOCUMENTS.
2.

DRAWINGS AND DESIGNS UNDERTAKEN BY A SHOP DETAILER SHALL BE PRESENTED TO THE PTA FOR REVIEW AND CONCURRENCE THAT THE DESIGN INTENT HAS BEEN ACHIEVED.
3.

THE CONTRACTORS SHALL BE FULLY AWARE OF THE OTHER INTERFACING PACKAGES AND SHALL HAVE DEEMED TO HAVE INCLUDED INTER-TRADE INTERFACES. THE INTERFACES IDENTIFIED IN THE DOCUMENTATION ARE TO INDICATE AN INTENT AND ARE NOT INTENDED TO BE EXHAUSTIVE. MAKE ALLOWANCES AS REQUIRED.

ISSUED FOR CONSTRUCTION

--	--	



NOTES:

1. DO NO SCALE DRAWINGS. WRITTEN DIMENSIONS GOVERN.
2. ALL DIMENSIONS ARE IN MILLIMETRES UNLESS NOTED OTHERWISE
3. ALL DIMENSIONS SHALL BE VERIFIED ON SITE BEFORE PROCEEDING WITH THE WORK. RELEVANT PARTY SHALL BE NOTIFIED IN WRITING OF ANY DISCREPANCIES.
4. THIS DRAWING MUST BE READ IN CONJUNCTION WITH ALL RELEVANT CONTRACTS, SPECIFICATIONS, REPORTS AND DRAWINGS.

2. REFER TO ARCHITECTS DRAWINGS FOR DIMENSIONS AND LEVELS
3. REFER TO 12-A-152-ST0002 TO ST0031 FOR STANDARD CONNECTIONS DETAILS
3. REFER TO 12-A-152-ST0003 & ST0004 FOR STANDARD NOTES
4. REFER TO THE STRUCTURAL SPECIFICATION FOR H.D. GALVANISING REQUIREMENTS
5. CONTRACTOR TO NOTE THAT THE MAIN WAREHOUSE FRAME ROOF BRACING ARE DESIGNED TO FUNCTION IN THE PERMANENT WORKS CASE AS TENSION ONLY BRACES AND TO MAKE DUE ALLOWANCE WHEN CONSIDERING TEMPORARY WORKS REQUIREMENTS FOR SAFE ERECTION
6. BRIDGING REQUIREMENTS AS NOTED ON PLANS, REFER TO MANUFACTURES' SPECIFICATIONS.
7. GIRTS AND PURLINS TO BE PROVIDED WITH A MINIMUM ZINC COATING CLASS OF Z450
8. PROVIDE A 50X50X3 COLD FORMED ANGLE TRIMMER BETWEEN ALL PURLINS AT ROOF HIP, VALLEY AND PENETRATION LOCATIONS TO SUPPORT CUT EDGES OF ROOF SHEETING
9. REFER TO SERVICES SUBCONTRACTOR DETAILS FOR SECONDARY STEELWORK TO SUPPORT SERVICES EQUIPMENT AND FOR ISOLATION DETAILS
10. PROVIDE EDGE PROTECTION TO ARCHITECTS DETAILS
11. ALL DIMENSIONS TO PRECAST PANELS ARE NOMINAL ONLY AND SHOULD BE REFERENCED WITH THE ARCHITECTS DRAWINGS. THESE SHALL BE CONFIRMED WITH THE PRECAST CONTRACTOR
12. REFER TO THE ARCHITECTS DRAWINGS FOR REBATES, CHAMFERS, DRIPS, SEALS, BAFFLES, ETC. AND EXTENT OF FINISHES
13. DOWEL TUBE SPACING ON PRECAST SHOP DRAWINGS SHALL INCORPORATE THE SURVEYED AS BUILT SETOUT OF DOWELS
14. IT IS THE CONTRACTORS RESPONSIBILITY TO CO-ORDINATE ALL PENETRATIONS FOR SERVICES ETC. ALL PENETRATIONS SHALL BE SHOWN ON SHOP DRAWINGS FOR APPROVAL PRIOR TO FABRICATION OF ANY PANEL
15. REFER TO THE ARCHITECTS DRAWINGS FOR ALL JOINTING DETAILS



1 : 100

NOTES:

1. PURLINS/GIRTS TO BE LAPPED WHERE SHOWN. LAP LENGTH TO BE AS PER MANUFACTURER'S RECOMMENDATIONS (MIN 15% OF SPAN).
2. PURLINS/GIRTS TO BE PROVIDED WITH MIN 1 MIDSPAN BRIDGING FOR ALL SPANS ABOVE 4m [U.N.O.]
3. PROVIDE GIRT HANGERS/SAG RODS/BRIDGING TO MANUFACTURERS DETAILS

NOTES:

1. PURLINS/GIRTS TO BE LAPPED WHERE SHOWN. LAP LENGTH TO BE AS PER MANUFACTURER'S RECOMMENDATIONS (MIN 15% OF SPAN).
2. PURLINS/GIRTS TO BE PROVIDED WITH MIN 1 MIDSPAN BRIDGING FOR ALL SPANS ABOVE 4m (U.N.O).
3. PROVIDE GIRT HANGERS/SAG RODS/BRIDGING TO MANUFACTURERS DETAILS

aurecon
www.aurecongroup.com

www.aurecongroup.com

505695-0000-DRG-ST-1638

REFERENCES

SCALE :	As indicated (@ A1)
DATUM :	HORIZONTAL: PCG94 VERTICAL: AHD71
PTA ACCEPTANCE STAMP	

DESIGNED	J.SPANO
DRAWN	A.DAWSON
CHECKED	M.PEARCE
APPROVED FOR ISSUE	
G.BENTLEY	
DATE	



Government of Western Australia
Public Transport Authority

DETAILED DESIGN FOR THE BELLEVUE DEPOT

HV TESTING FACILITY


STRUCTURAL

SOUTH ELEVATION - ZONE 01

PTA Drawing No: 12-A-152-ST0255

REV : C

Plot Date: 10/1/2019 9:25:57 AM Office: Filename: RIM 360://505695 - Bellevue Depot/505695-ST-BELL EVUE DEPOT-02B.c...

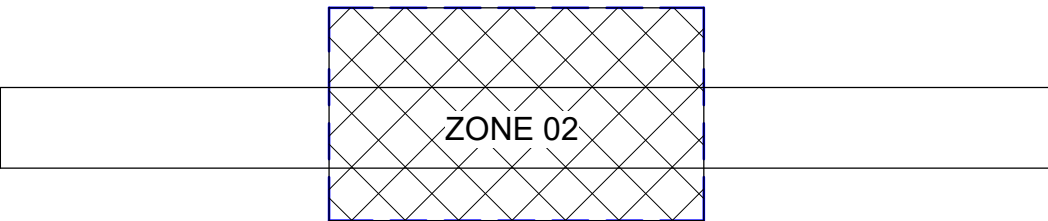


ZONE PLAN

NOTES:

- DO NO SCALE DRAWINGS. WRITTEN DIMENSIONS GOVERN.
- ALL DIMENSIONS ARE IN MILLIMETRES UNLESS NOTED OTHERWISE
- ALL DIMENSIONS SHALL BE VERIFIED ON SITE BEFORE PROCEEDING WITH THE WORK. RELEVANT PARTY SHALL BE NOTIFIED IN WRITING OF ANY DISCREPANCIES.
- THIS DRAWING MUST BE READ IN CONJUNCTION WITH ALL RELEVANT CONTRACTS, SPECIFICATIONS, REPORTS AND DRAWINGS.

NOTES:

- REFER TO ARCHITECTS DRAWINGS FOR DIMENSIONS AND LEVELS
- REFER TO 12-A-152-ST0022 TO ST0031 FOR STANDARD CONNECTIONS DETAILS
- REFER TO 12-A-152-ST0003 & ST0004 FOR STANDARD NOTES
- REFER TO THE STRUCTURAL SPECIFICATION FOR H.D. GALVANISING REQUIREMENTS
- CONTRACTOR TO NOTE THAT THE MAIN WAREHOUSE FRAME ROOF BRACING ARE DESIGNED TO FUNCTION IN THE PERMANENT WORKS CASE AS TENSION ONLY BRACES AND TO MAKE DUE ALLOWANCE WHEN CONSIDERING TEMPORARY WORKS REQUIREMENTS FOR SAFE ERECTION
- BRIDGING REQUIREMENTS AS NOTED ON PLANS, REFER TO MANUFACTURES' SPECIFICATIONS.
- GIRTS AND PURLINS TO BE PROVIDED WITH A MINIMUM ZINC COATING CLASS OF Z450
- PROVIDE A 50X50X3 COLD FORMED ANGLE TRIMMER BETWEEN ALL PURLINS AT ROOF HIP, VALLEY AND PENETRATION LOCATIONS TO SUPPORT CUT EDGES OF ROOF SHEETING
- REFER TO SERVICES SUBCONTRACTOR DETAILS FOR SECONDARY STEELWORK TO SUPPORT SERVICES EQUIPMENT AND FOR ISOLATION DETAILS
- PROVIDE EDGE PROTECTION TO ARCHITECTS DETAILS
- ALL DIMENSIONS TO PRECAST PANELS ARE NOMINAL ONLY AND SHOULD BE REFERENCED WITH THE ARCHITECTS DRAWINGS. THESE SHALL BE CONFIRMED WITH THE PRECAST CONTRACTOR
- REFER TO THE ARCHITECTS DRAWINGS FOR REBATES, CHAMFERS, DRIPS, SEALS, BAFFLES, ETC. AND EXTENT OF FINISHES
- DOWEL TUBE SPACING ON PRECAST SHOP DRAWINGS SHALL INCORPORATE THE SURVEYED AS BUILT SETOUT OF DOWELS
- IT IS THE CONTRACTORS RESPONSIBILITY TO CO-ORDINATE ALL PENETRATIONS FOR SERVICES ETC. ALL PENETRATIONS SHALL BE SHOWN ON SHOP DRAWINGS FOR APPROVAL PRIOR TO FABRICATION OF ANY PANEL
- REFER TO THE ARCHITECTS DRAWINGS FOR ALL JOINTING DETAILS

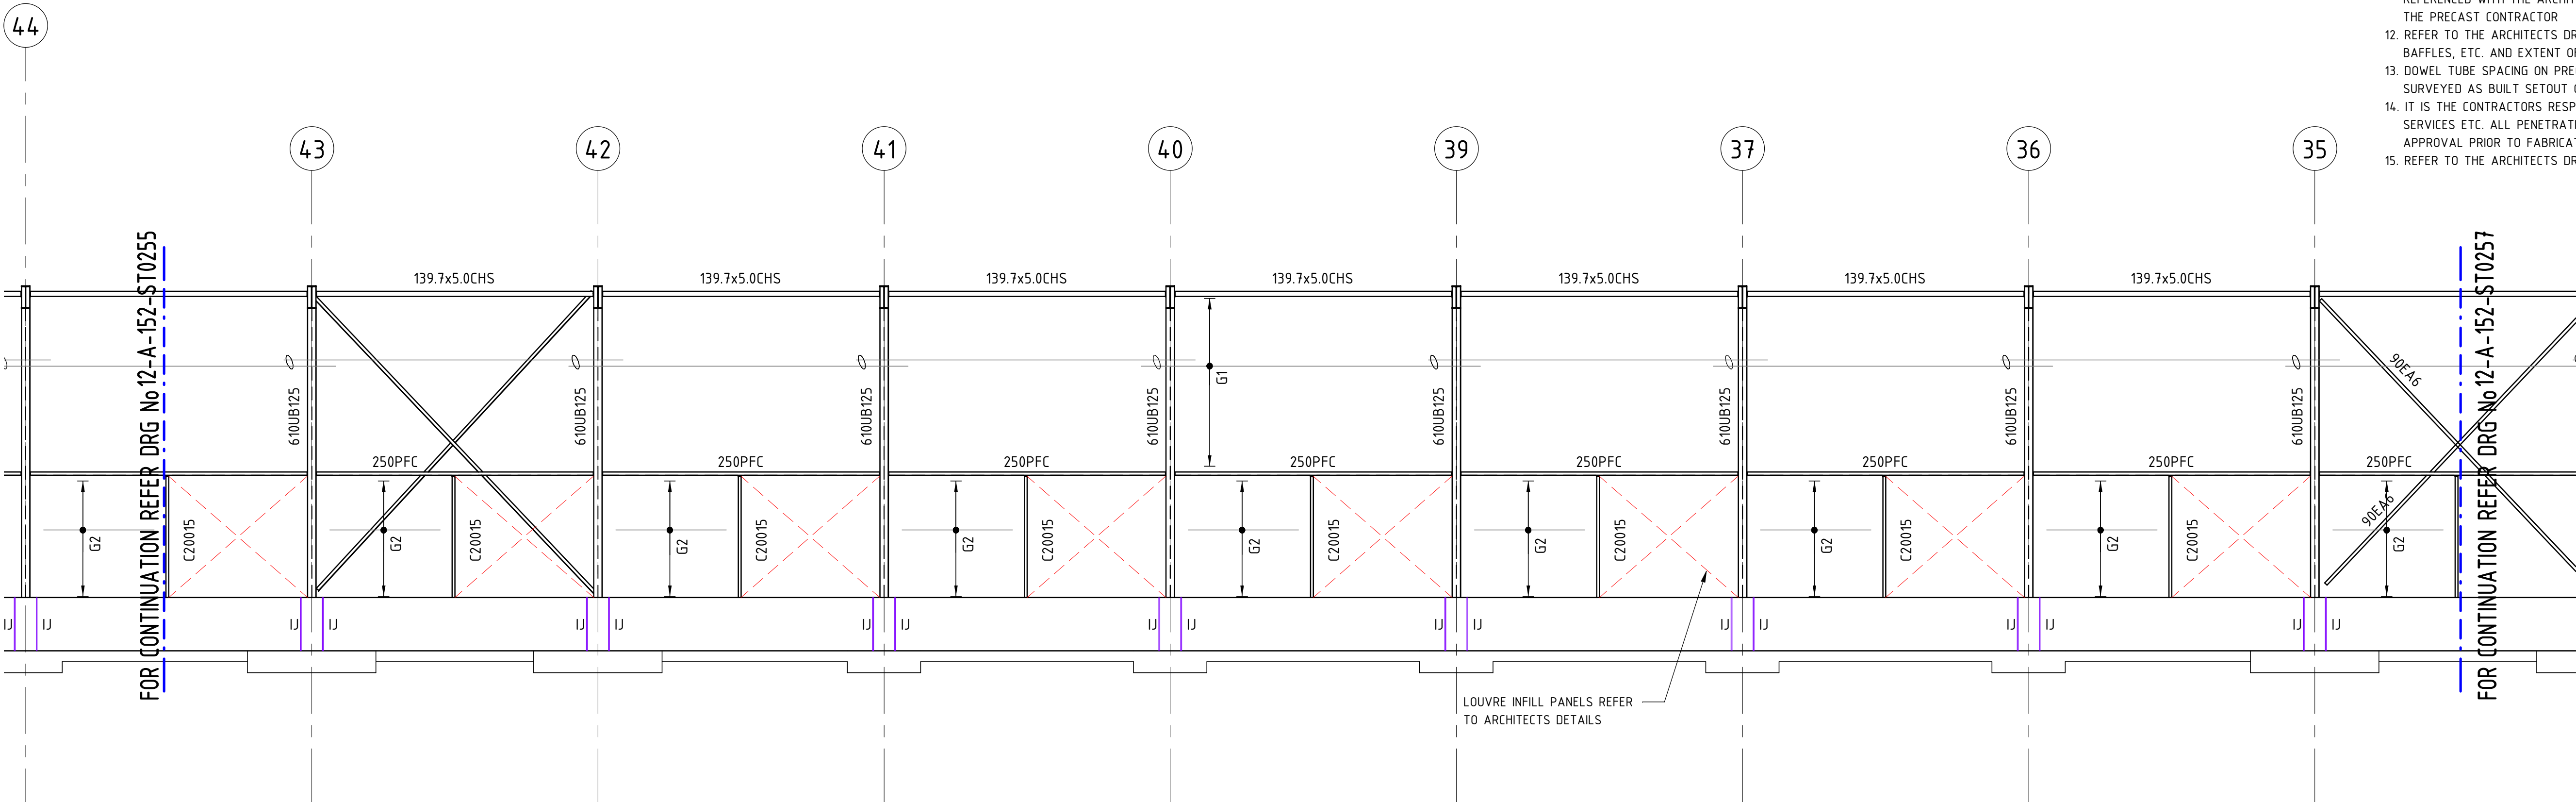

TAG	MEMBER	COMMENTS
G1	Z20024 AT 1200 CTS	1 ROW OF BRIDGING (MIN 4 LAPPED SPANS)
G2	Z20019 AT 1200CTS	(SINGLE SPAN)
G3	Z20019 AT 600CTS	(SINGLE SPAN)
G4	Z20019 AT 600CTS	MIN 4 LAPPED SPANS

NOTES:

- PURLINS/GIRTS TO BE LAPPED WHERE SHOWN. LAP LENGTH TO BE AS PER MANUFACTURER'S RECOMMENDATIONS (MIN 15% OF SPAN).
- PURLINS/GIRTS TO BE PROVIDED WITH MIN 1 MIDSPAN BRIDGING FOR ALL SPANS ABOVE 4m (U.N.O).
- PROVIDE GIRT HANGERS/SAG RODS/BRIDGING TO MANUFACTURERS DETAILS

USE OF THESE DRAWINGS

- THIS DRAWING SHALL BE READ IN CONJUNCTION WITH THE DISCIPLINE CONTRACT SPECIFICATION AND OTHER PROJECT DOCUMENTS.
- DRAWINGS AND DESIGNS UNDERTAKEN BY A SHOP DETAILER SHALL BE PRESENTED TO THE PTA FOR REVIEW AND CONCURRENCE THAT THE DESIGN INTENT HAS BEEN ACHIEVED.
- THE CONTRACTORS SHALL BE FULLY AWARE OF THE OTHER INTERFACING PACKAGES AND SHALL HAVE DEEMED TO HAVE INCLUDED INTER-TRADE INTERFACES. THE INTERFACES IDENTIFIED IN THE DOCUMENTATION ARE TO INDICATE AN INTENT AND ARE NOT INTENDED TO BE EXHAUSTIVE. MAKE ALLOWANCES AS REQUIRED.

ISSUED FOR CONSTRUCTION

REV	DATE	AMENDMENT	DSN	DRN	CHKD	APP
0	01.10.19	ISSUED FOR CONSTRUCTION	J.S.	A.C.D.	M.P.	G.B.
A1						

aurecon
www.aurecongroup.com

505695-0000-DRG-ST-1639

REFERENCES

SCALE :
As indicated (@ A1)
DATUM :
HORIZONTAL: PCG94
VERTICAL: AHD71
PTA ACCEPTANCE STAMP

DESIGNED J.SPANO
DRAWN A.DAWSON
CHECKED M.PEARCE
APPROVED FOR ISSUE
G.BENTLEY
DATE



DETAILED DESIGN FOR THE BELLEVUE DEPOT

HV TESTING FACILITY

STRUCTURAL

SOUTH ELEVATION - ZONE 02

PTA Drawing No: 12-A-152-ST0256

REV : 0

ZONE 03

NOTES:

- NOTES:

- 1 : 100

DATE _____



1. DO NO SCALE DRAWINGS. WRITTEN DIMENSIONS GOVERN.
2. ALL DIMENSIONS ARE IN MILLIMETRES UNLESS NOTED OTHERWISE
3. ALL DIMENSIONS SHALL BE VERIFIED ON SITE BEFORE PROCEEDING WITH THE WORK. RELEVANT PARTY SHALL BE NOTIFIED IN WRITING OF ANY DISCREPANCIES.
4. THIS DRAWING MUST BE READ IN CONJUNCTION WITH ALL RELEVANT CONTRACTS, SPECIFICATIONS, REPORTS AND DRAWINGS.

1. PURLINS/GIRTS TO BE LAPPED WHERE SHOWN. LAP LENGTH TO BE AS PER MANUFACTURER'S RECOMMENDATIONS (MIN 15% OF SPAN).
2. PURLINS/GIRTS TO BE PROVIDED WITH MIN 1 MIDSPAN BRIDGING FOR ALL SPANS ABOVE 4m [U.N.O].
3. PROVIDE GIRT HANGERS/SAG RODS/BRIDGING TO MANUFACTURERS DETAILS

aurecon
www.aurecongroup.com

505695-0000-DRG-ST-1641

SCALE :
As indicated (@ A1)

DATUM :
HORIZONTAL: PCG94
VERTICAL: AHD71

DESIGNED	J.SPANO
DRAWN	A.DAWSON
CHECKED	M.PEARCE
APPROVED FOR ISSUE	
G.BENTLEY	
DATE	

1. THIS DRAWING SHALL BE READ IN CONJUNCTION WITH THE DISCIPLINE CONTRACT SPECIFICATION AND OTHER PROJECT DOCUMENTS.
2. DRAWINGS AND DESIGNS UNDERTAKEN BY A SHOP DETAILER SHALL BE PRESENTED TO THE PTA FOR REVIEW AND CONCURRENCE THAT THE DESIGN INTENT HAS BEEN ACHIEVED.
3. THE CONTRACTORS SHALL BE FULLY AWARE OF THE OTHER INTERFACING PACKAGES AND SHALL HAVE DEEMED TO HAVE INCLUDED INTER-TRADE INTERFACES. THE INTERFACES IDENTIFIED IN THE DOCUMENTATION ARE TO INDICATE AN INTENT AND ARE NOT INTENDED TO BE EXHAUSTIVE. MAKE ALLOWANCES AS REQUIRED.

Government of Western Australia
Public Transport Authority



DETAILED DESIGN FOR THE BELLEVUE DEPOT

PTA Drawing No: 12-A-152-ST0258

REV : C

NOTES:

1. DO NO SCALE DRAWINGS. WRITTEN DIMENSIONS GOVERN.
2. ALL DIMENSIONS ARE IN MILLIMETRES UNLESS NOTED OTHERWISE
3. ALL DIMENSIONS SHALL BE VERIFIED ON SITE BEFORE PROCEEDING WITH THE WORK. RELEVANT PARTY SHALL BE NOTIFIED IN WRITING OF ANY DISCREPANCIES.
4. THIS DRAWING MUST BE READ IN CONJUNCTION WITH ALL RELEVANT CONTRACTS, SPECIFICATIONS, REPORTS AND DRAWINGS.

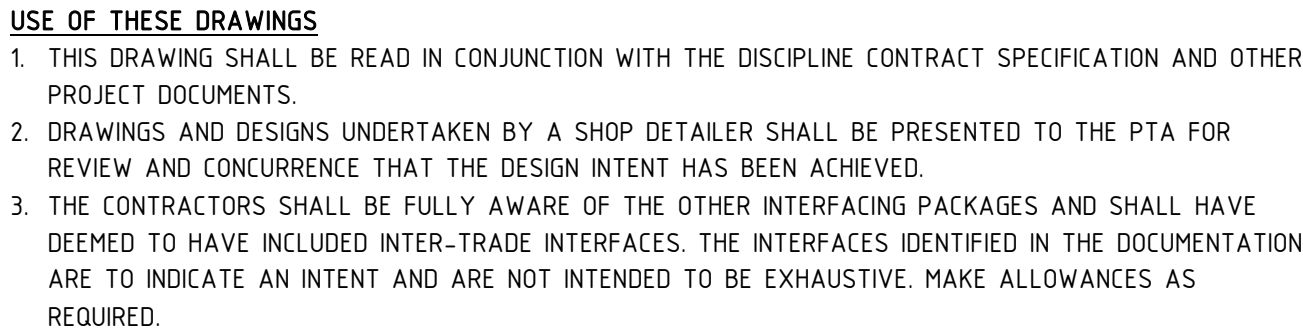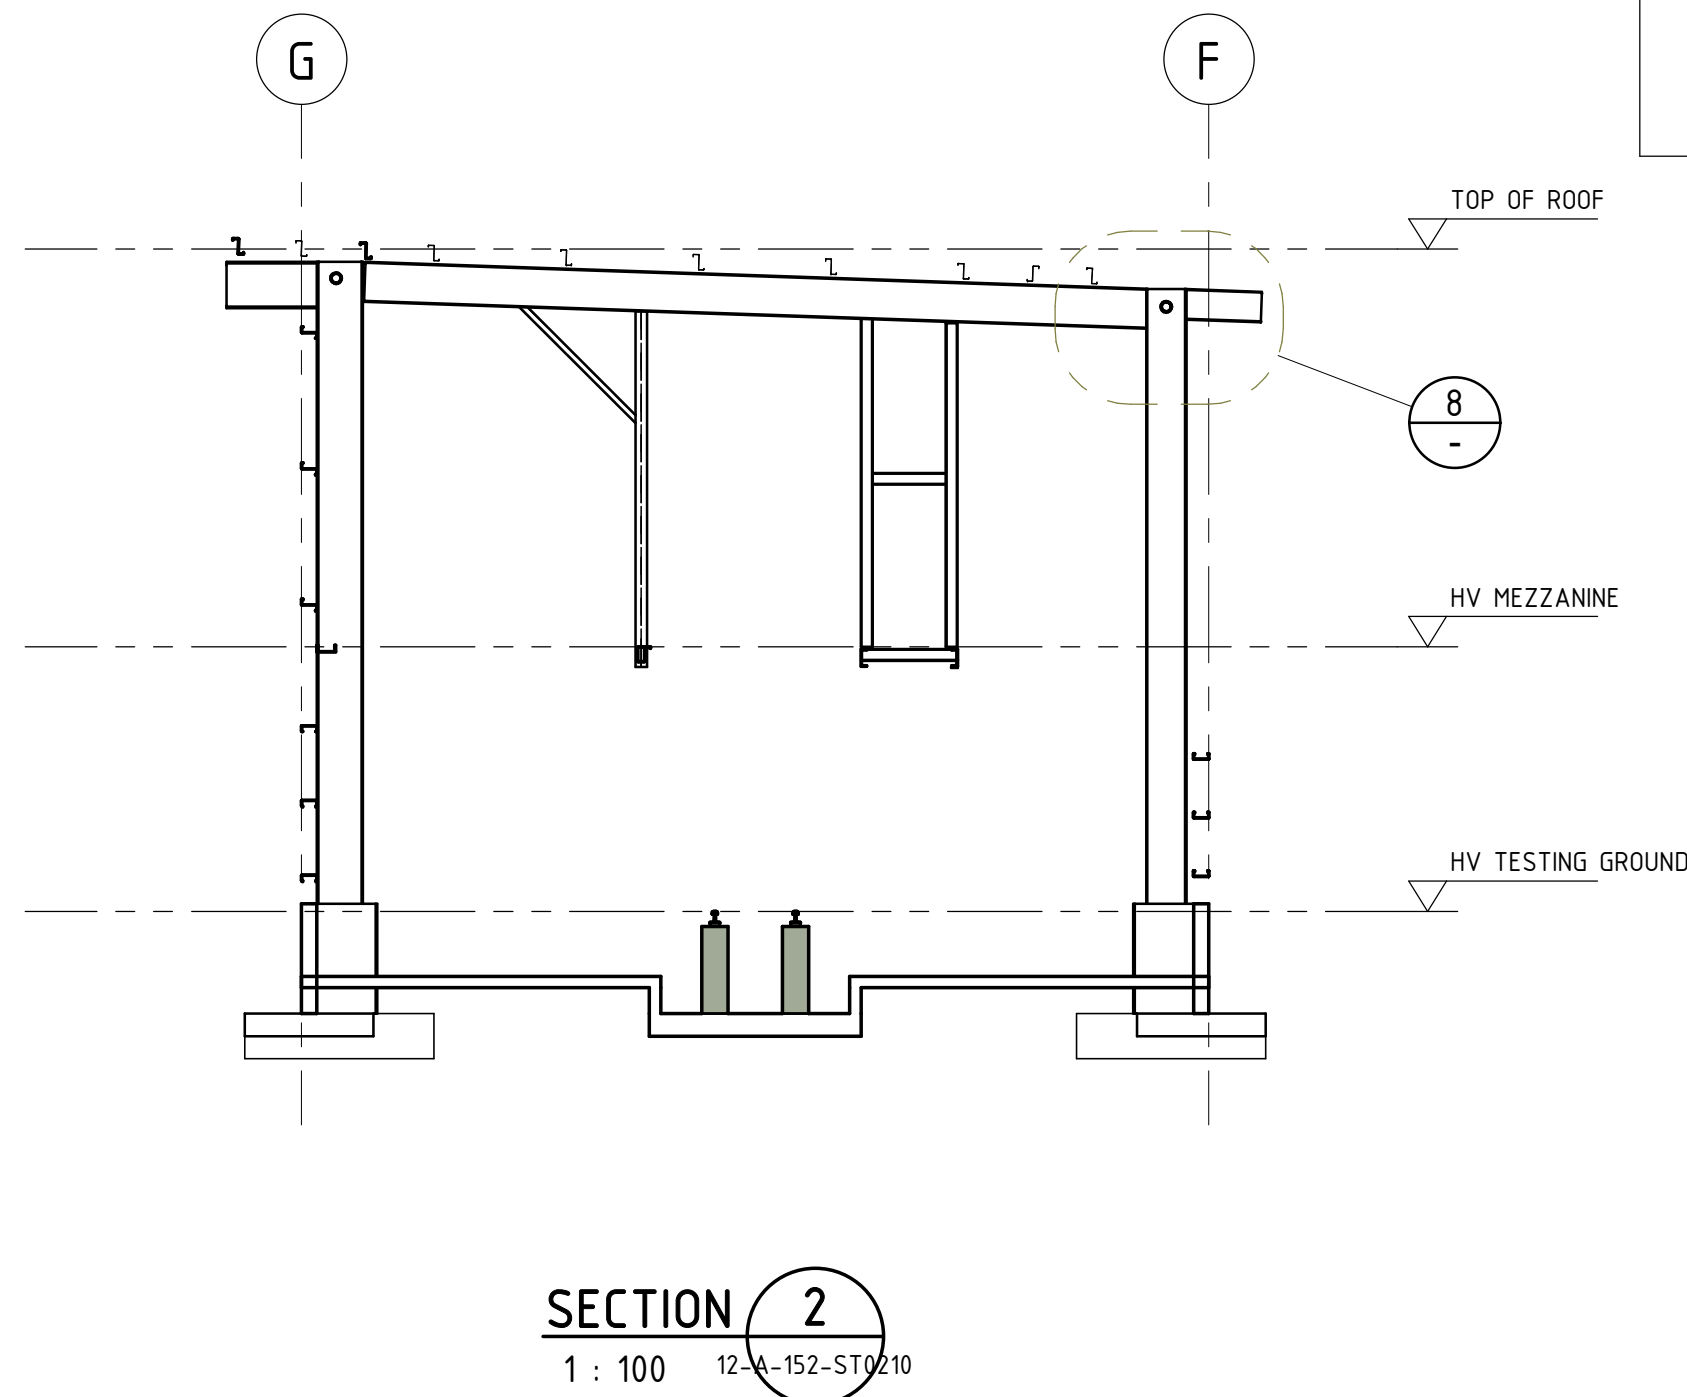

ISSUED FOR CONSTRUCTION



Government of Western Australia
Public Transport Authority

DETAILED DESIGN FOR THE BELLEVUE DEPOT

HV TESTING FACILITY

STRUCTURAL

BUILDING SECTIONS - SHEET 1 OF 1

PTA Drawing No: 12-A-152-ST0260

REV : C

[illegible]

www.aurecongroup.com

505695-0000-DRG-ST-1710

REFERENCES

SCALE :
As indicated (@ A1)

DATUM :
HORIZONTAL: PCG94
VERTICAL: AHD71

PTA ACCEPTANCE STAMP

DESIGNED	J.SPANO
----------	---------

DRAWN	A.DAWSON
CHECKED	M.PEARCE

APPROVED FOR ISSUE

G.BENTLEY

DAT

ZONE 01	ZONE 02	ZONE 03
---------	---------	---------


ZONE PLAN

NOTES:


- DO NO SCALE DRAWINGS. WRITTEN DIMENSIONS GOVERN.
- ALL DIMENSIONS ARE IN MILLIMETRES UNLESS NOTED OTHERWISE
- ALL DIMENSIONS SHALL BE VERIFIED ON SITE BEFORE PROCEEDING WITH THE WORK. RELEVANT PARTY SHALL BE NOTIFIED IN WRITING OF ANY DISCREPANCIES.
- THIS DRAWING MUST BE READ IN CONJUNCTION WITH ALL RELEVANT CONTRACTS, SPECIFICATIONS, REPORTS AND DRAWINGS.

NOTES:


- REFER TO 12-A-152-ST004 FOR GENERAL STEEL NOTES
- REFER TO ARCHITECTURAL DRAWINGS FOR TYP. SYSTEM WIDE PROPRIETARY HANDRAIL DETAILS

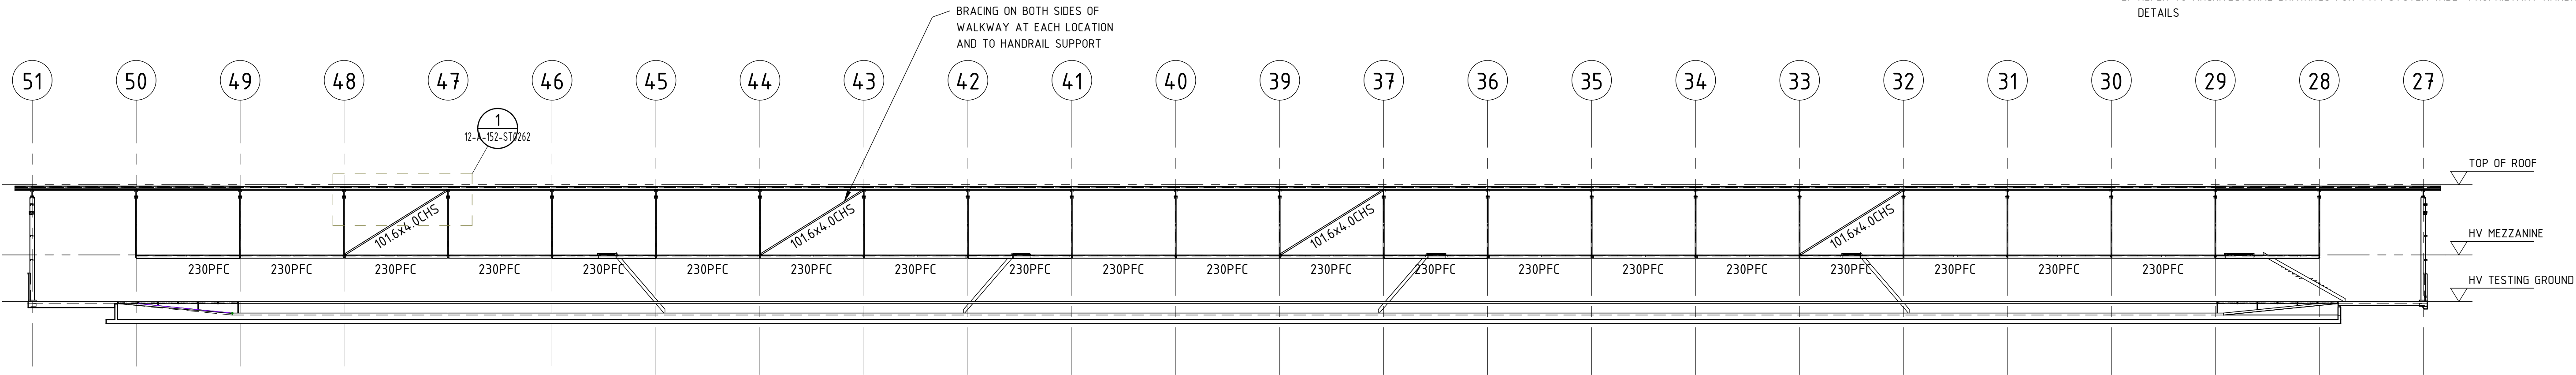


SECTION 5
1 : 250 12-A-152-ST0210

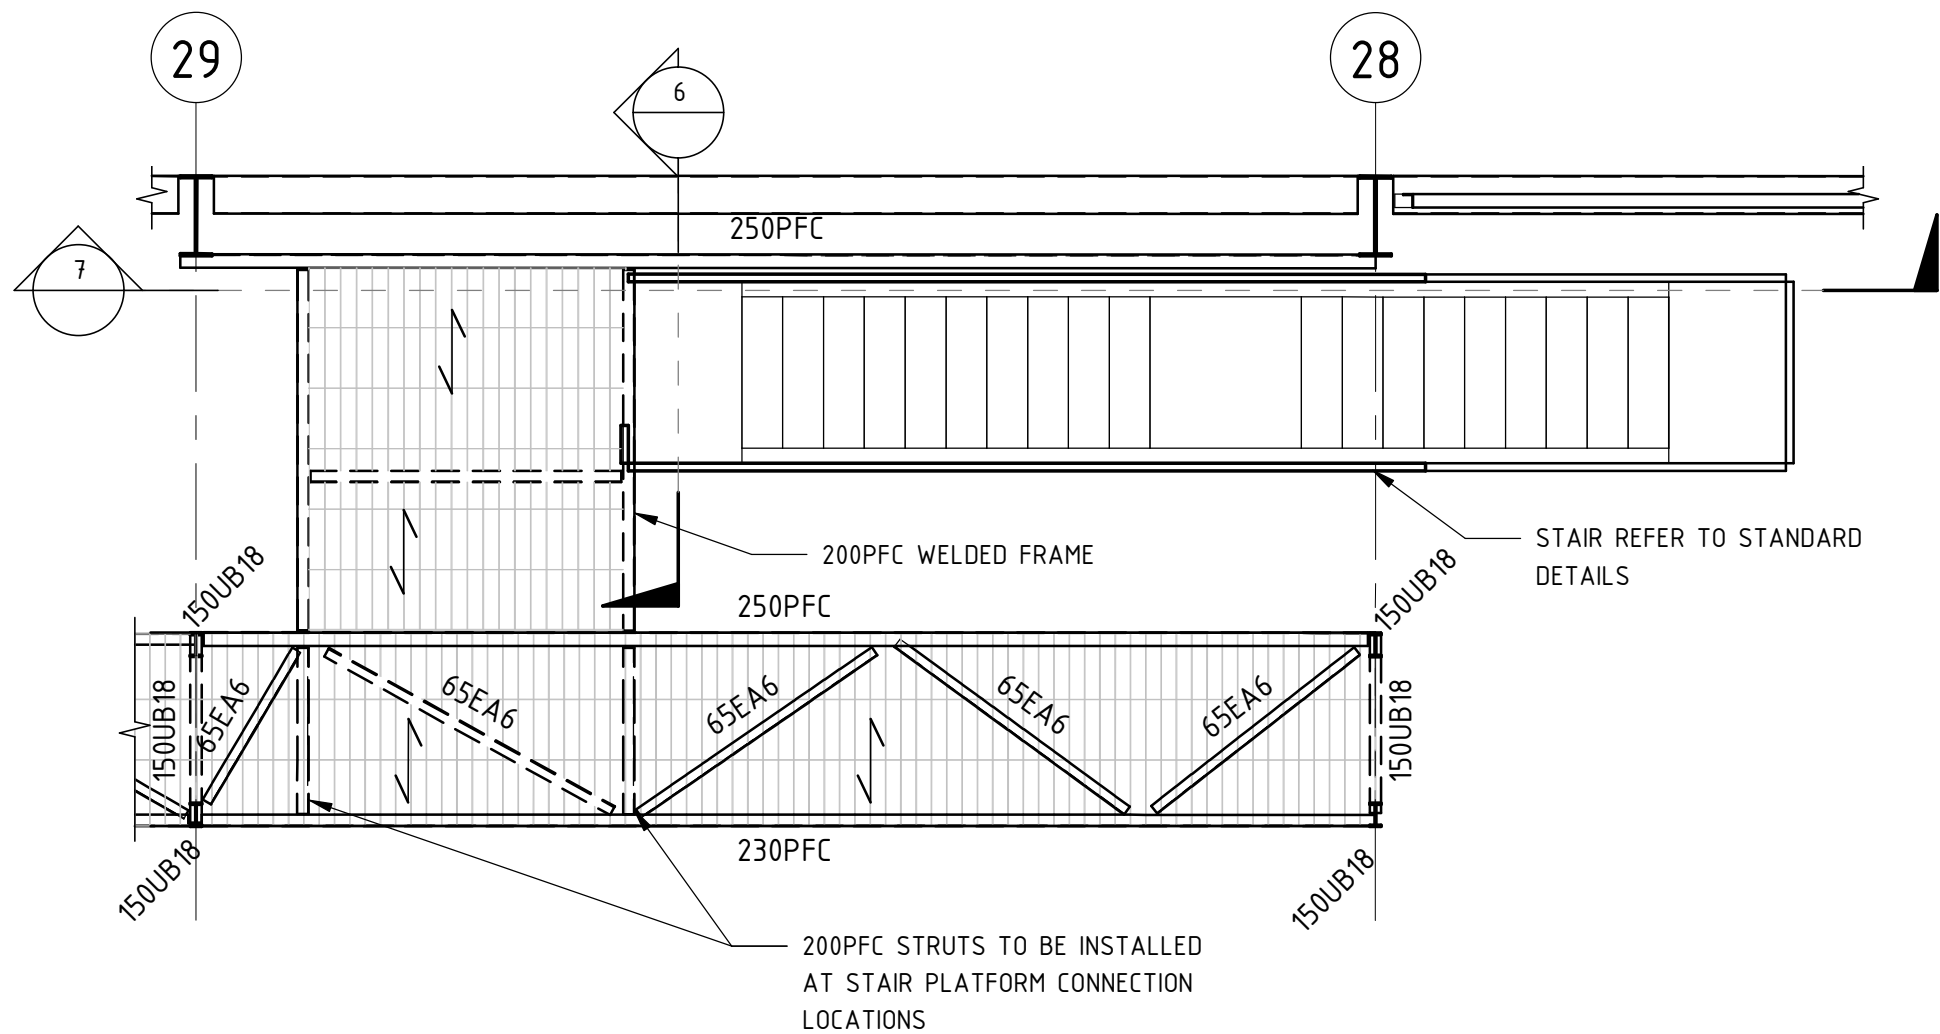


DETAIL 4
1 : 50 12-A-152-ST0223

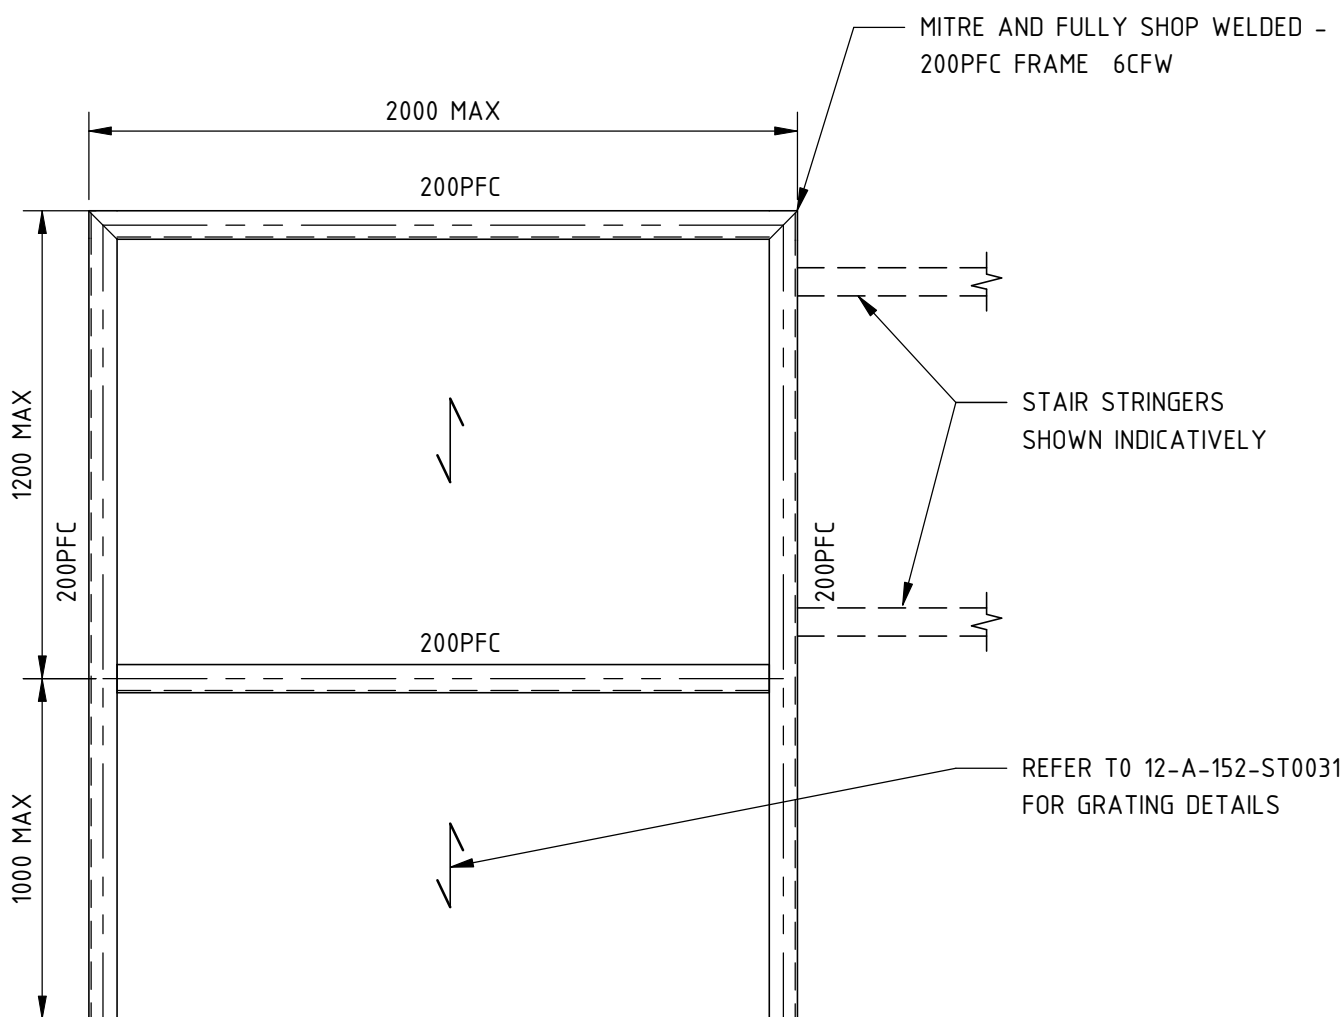


200PFC WELDED FRAME STAIR LANDING PLATFORM PLAN
1 : 20

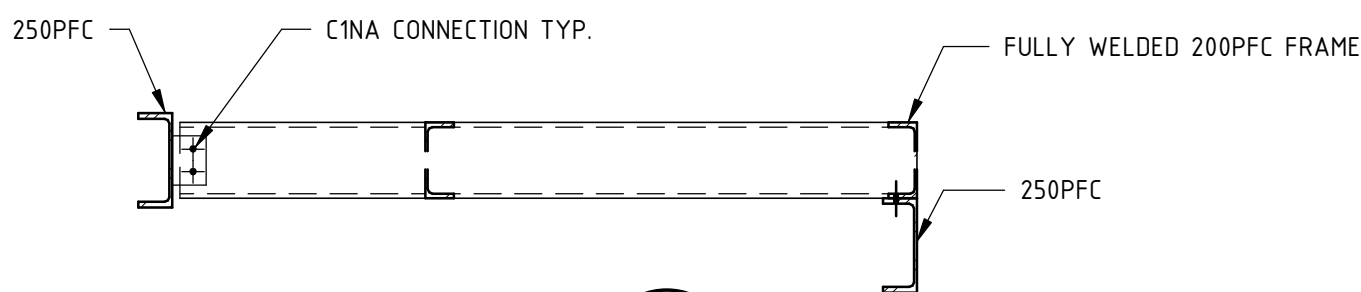


SECTION 6
1 : 20 12-A-152-ST0261

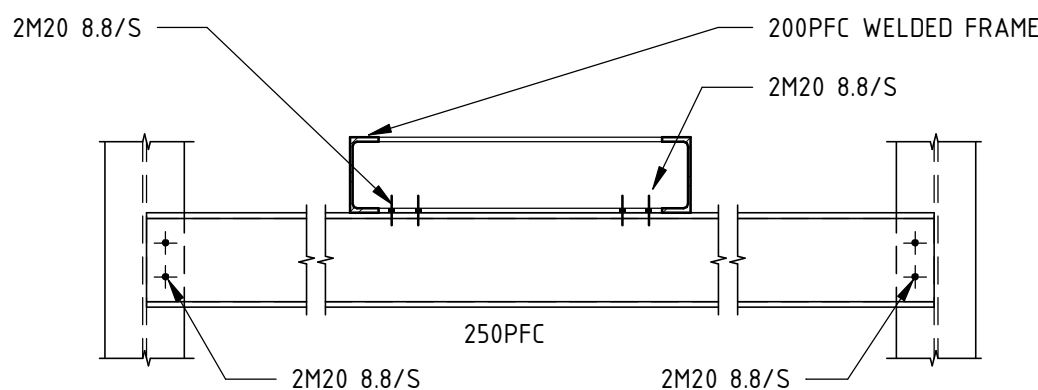

SECTION 7
1 : 20 12-A-152-ST0261

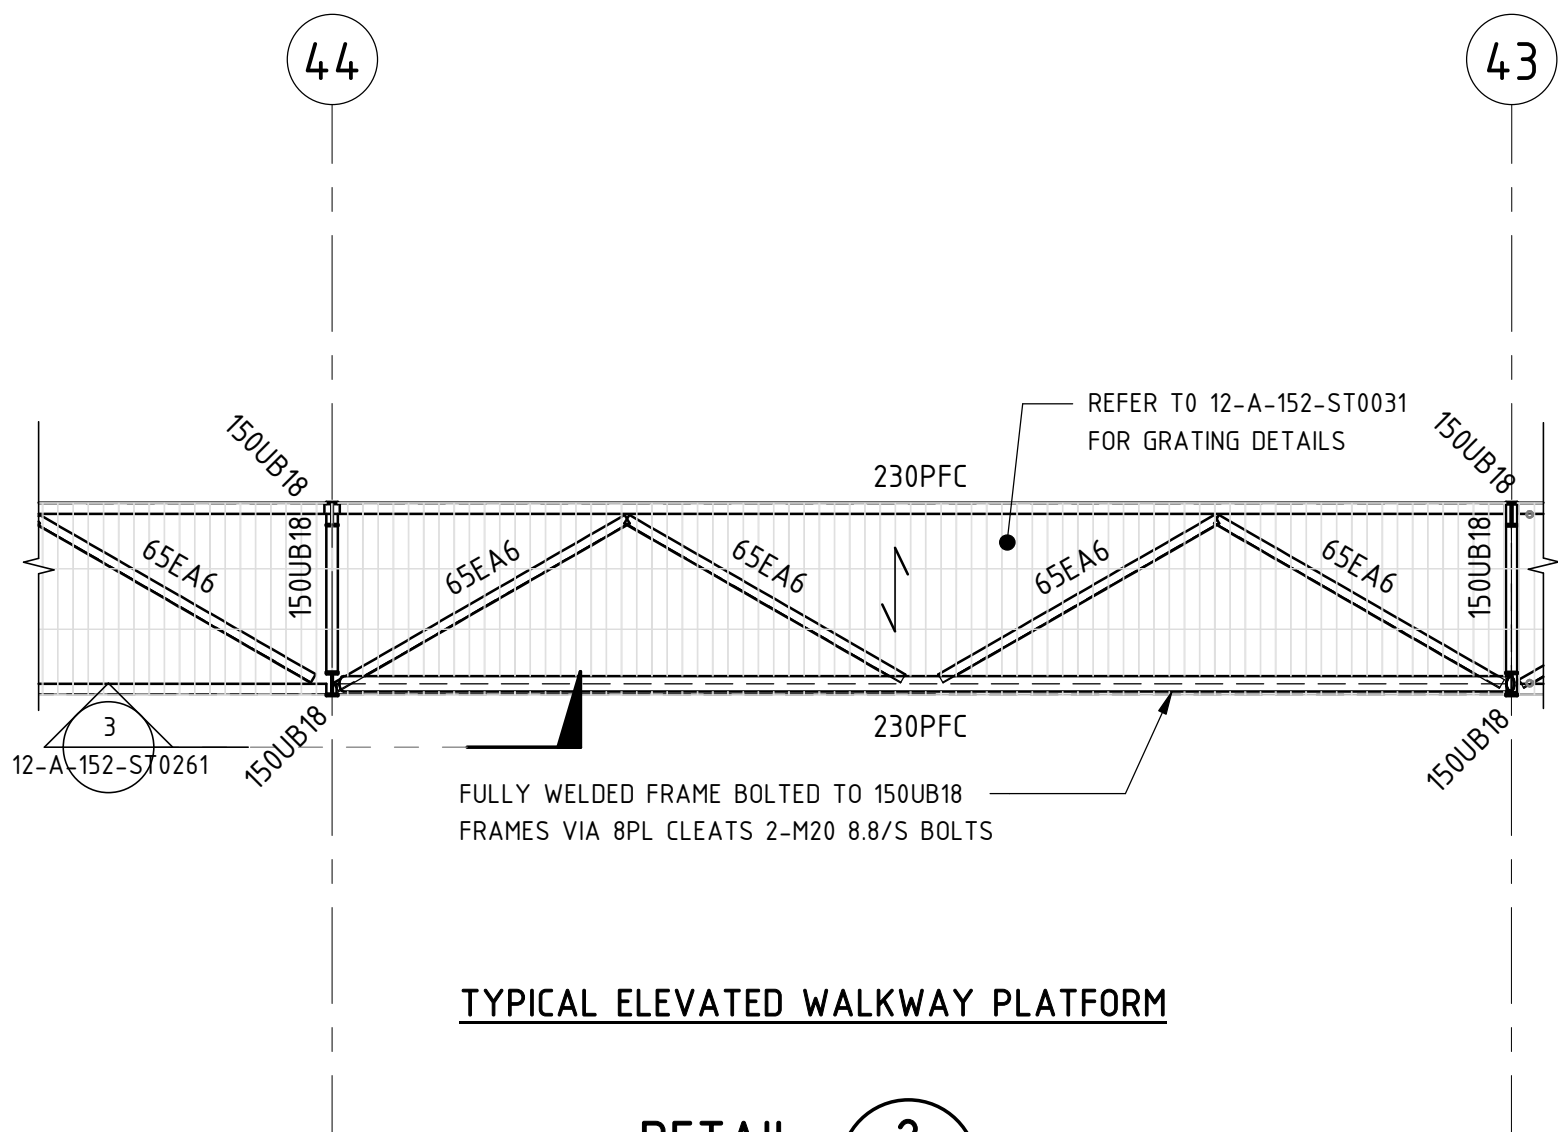

DETAIL 2
1 : 50 12-A-152-ST0221

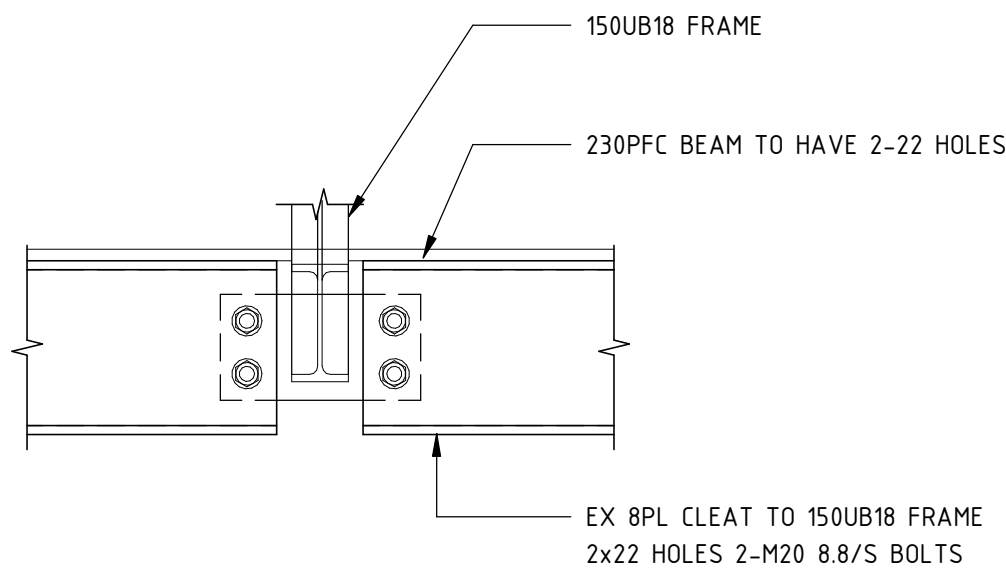

SECTION 3
1 : 10 12-A-152-ST0261

USE OF THESE DRAWINGS

- THIS DRAWING SHALL BE READ IN CONJUNCTION WITH THE DISCIPLINE CONTRACT SPECIFICATION AND OTHER PROJECT DOCUMENTS.
- DRAWINGS AND DESIGNS UNDERTAKEN BY A SHOP DETAILER SHALL BE PRESENTED TO THE PTA FOR REVIEW AND CONCURRENCE THAT THE DESIGN INTENT HAS BEEN ACHIEVED.
- THE CONTRACTORS SHALL BE FULLY AWARE OF THE OTHER INTERFACING PACKAGES AND SHALL HAVE DEEMED TO HAVE INCLUDED INTER-TRADE INTERFACES. THE INTERFACES IDENTIFIED IN THE DOCUMENTATION ARE TO INDICATE AN INTENT AND ARE NOT INTENDED TO BE EXHAUSTIVE. MAKE ALLOWANCES AS REQUIRED.

ISSUED FOR CONSTRUCTION

0	01.10.19	ISSUED FOR CONSTRUCTION	J.S.	A.C.D.	M.P.	G.B.
REV	DATE	AMENDMENT	DSN	DRN	CHKD	APP
ORIG SIZE	A1	SCALE 1:250 AT A1				

aurecon
www.aurecongroup.com

505695-0000-DRG-ST-1711

REFERENCES

SCALE :
As indicated (@ A1)
DATUM :
HORIZONTAL: PCG94
VERTICAL: AHD71
PTA ACCEPTANCE STAMP

DESIGNED J.SPANO
DRAWN A.DAWSON
CHECKED M.PEARCE
APPROVED FOR ISSUE
G.BENTLEY
DATE





DETAILED DESIGN FOR THE BELLEVUE DEPOT


HV TESTING FACILITY
STRUCTURAL
PLATFORM DETAILS

PTA Drawing No: 12-A-152-ST0261

REV : 0

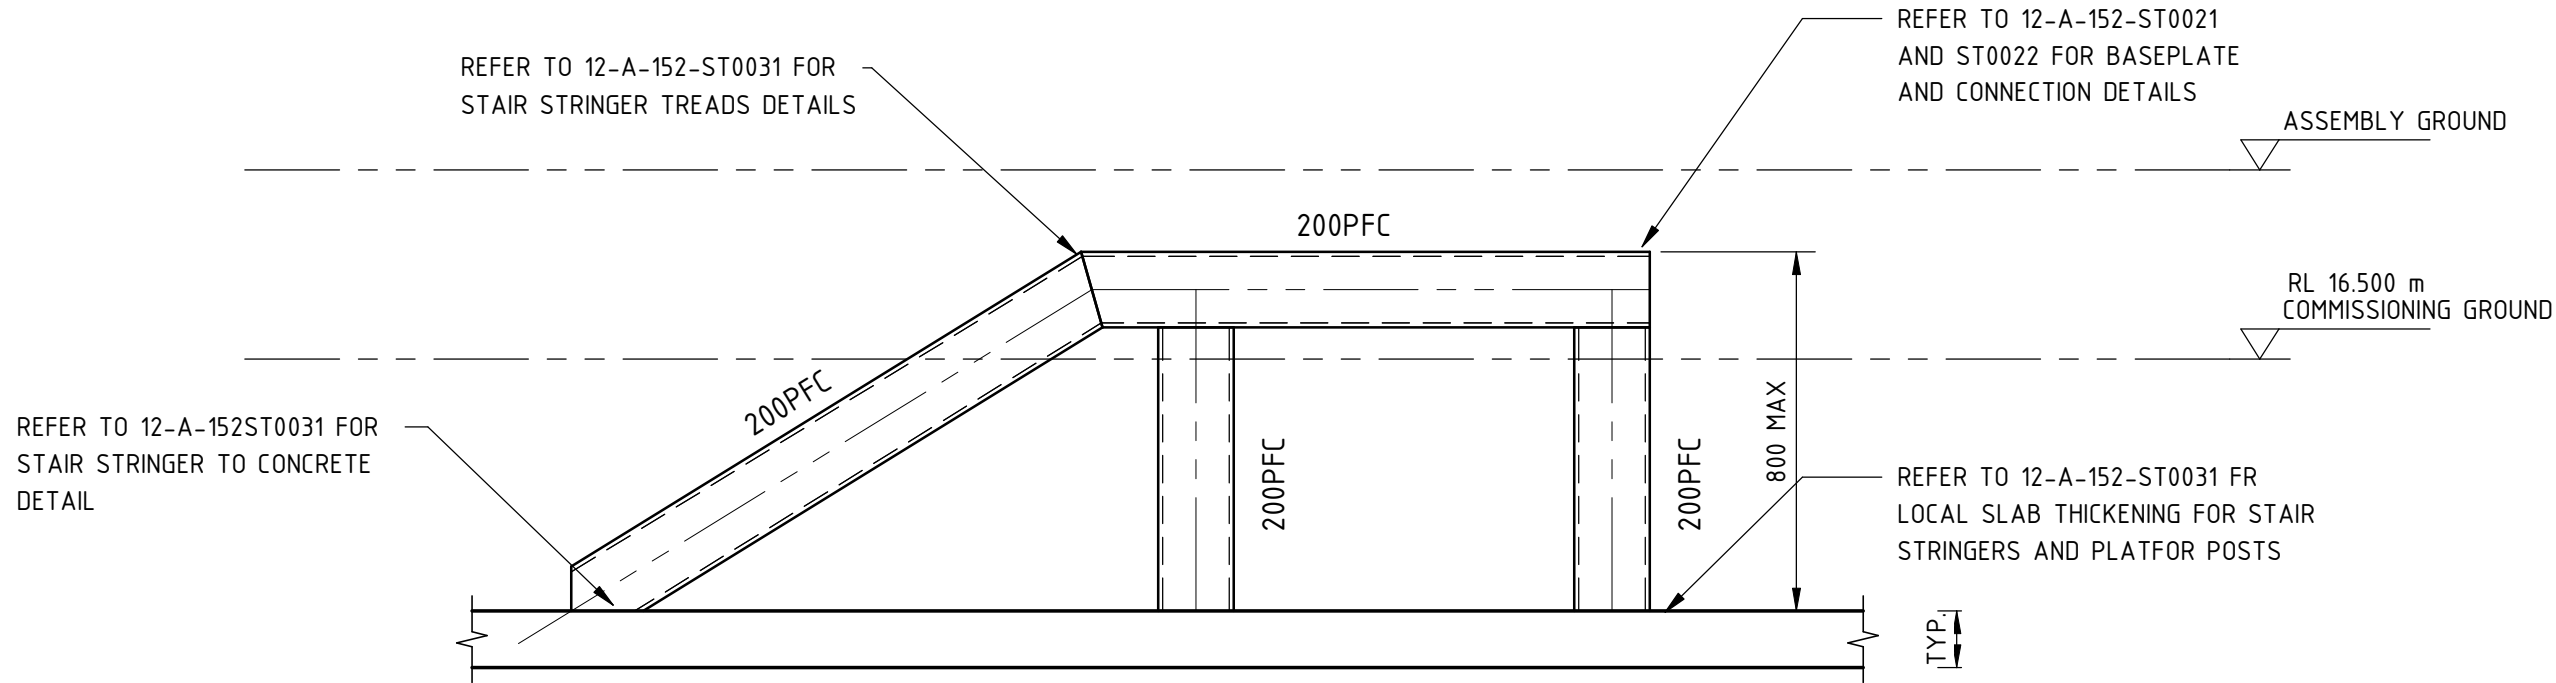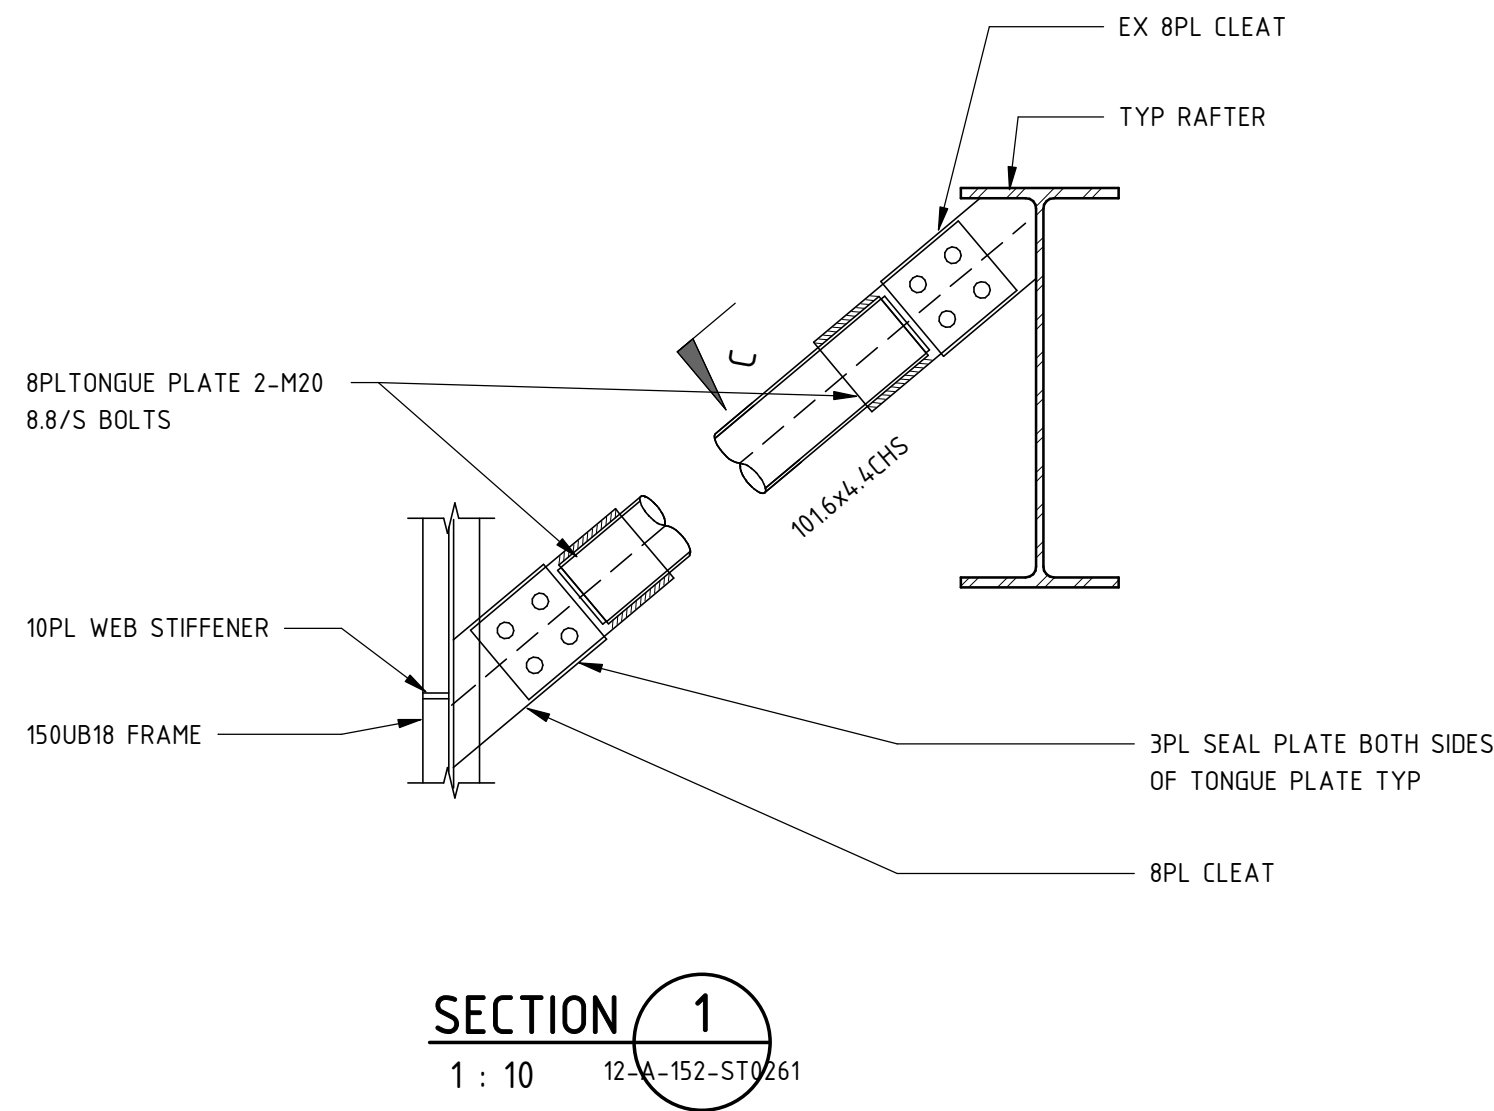

TYPICAL LOW LEVEL STAIR PLATFORM ELEVATION
1 : 20

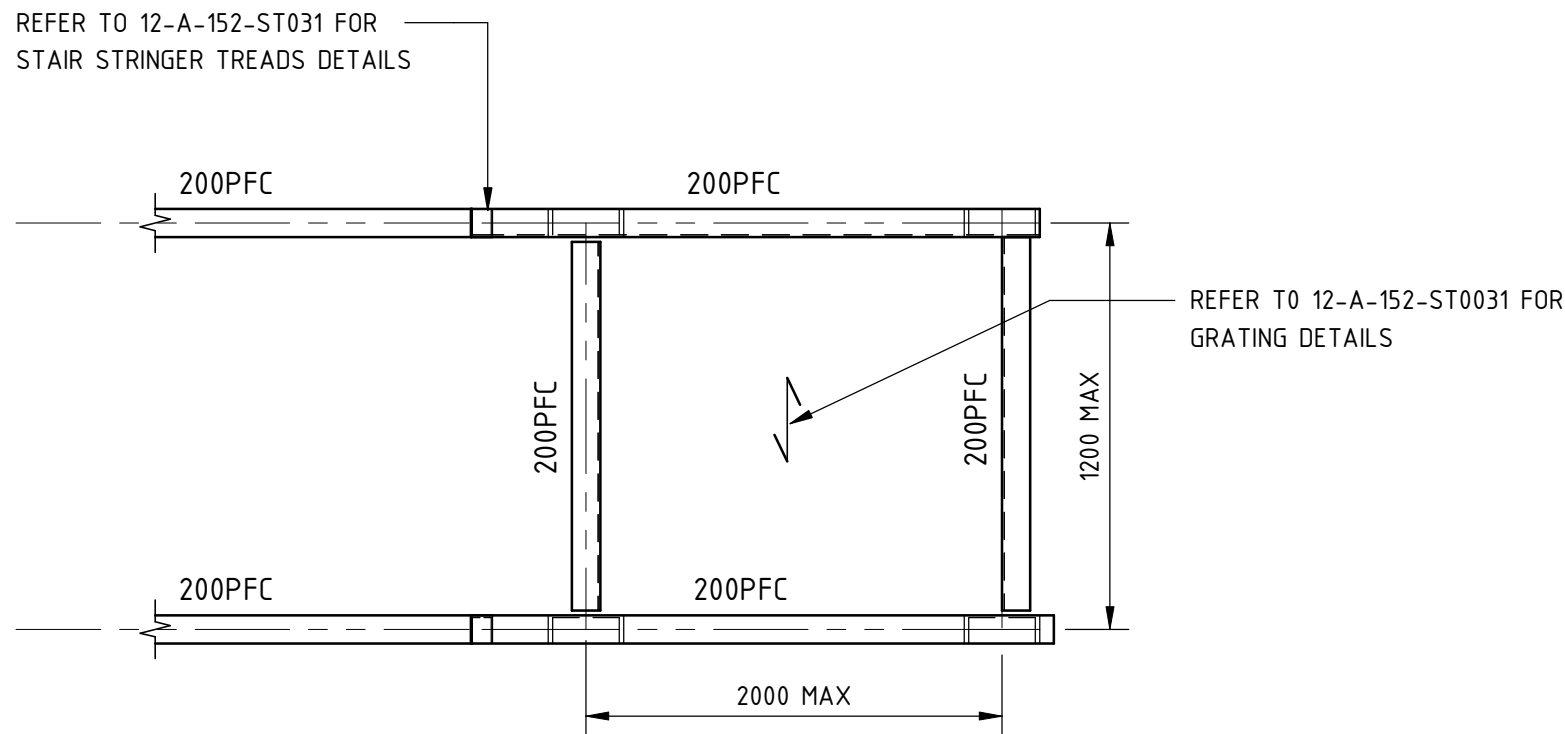

TYPICAL LOW LEVEL STAIR PLATFORM PLAN
1 : 20

NOTES:

- DO NO SCALE DRAWINGS. WRITTEN DIMENSIONS GOVERN.
- ALL DIMENSIONS ARE IN MILLIMETRES UNLESS NOTED OTHERWISE
- ALL DIMENSIONS SHALL BE VERIFIED ON SITE BEFORE PROCEEDING WITH THE WORK. RELEVANT PARTY SHALL BE NOTIFIED IN WRITING OF ANY DISCREPANCIES.
- THIS DRAWING MUST BE READ IN CONJUNCTION WITH ALL RELEVANT CONTRACTS, SPECIFICATIONS, REPORTS AND DRAWINGS.

ZONE PLAN

NOTES:

- REFER TO 12-A-152-ST004 FOR GENERAL STEEL NOTES
- REFER TO ARCHITECTURAL DRAWINGS FOR TYP. SYSTEM WIDE PROPRIETARY HANDRAIL DETAILS

USE OF THESE DRAWINGS

- THIS DRAWING SHALL BE READ IN CONJUNCTION WITH THE DISCIPLINE CONTRACT SPECIFICATION AND OTHER PROJECT DOCUMENTS.
- DRAWINGS AND DESIGNS UNDERTAKEN BY A SHOP DETAILER SHALL BE PRESENTED TO THE PTA FOR REVIEW AND CONCURRENCE THAT THE DESIGN INTENT HAS BEEN ACHIEVED.
- THE CONTRACTORS SHALL BE FULLY AWARE OF THE OTHER INTERFACING PACKAGES AND SHALL HAVE DEEMED TO HAVE INCLUDED INTER-TRADE INTERFACES. THE INTERFACES IDENTIFIED IN THE DOCUMENTATION ARE TO INDICATE AN INTENT AND ARE NOT INTENDED TO BE EXHAUSTIVE. MAKE ALLOWANCES AS REQUIRED.

ISSUED FOR CONSTRUCTION

0	01.10.19	ISSUED FOR CONSTRUCTION				J.S.	A.C.D.	M.P.	G.B.
REV	DATE	AMENDMENT				DSN	DRN	CHKD	APP
ORIG SIZE									
A1									



505695-0000-DRG-ST-1712

REFERENCES

SCALE :
As indicated (@ A1)
DATUM :
HORIZONTAL: PC694
VERTICAL: AHD71
PTA ACCEPTANCE STAMP

DESIGNED J.SPANO
DRAWN A.DAWSON
CHECKED M.PEARCE
APPROVED FOR ISSUE
G.BENTLEY
DATE




DETAILED DESIGN FOR THE BELLEVUE DEPOT




HV TESTING FACILITY
STRUCTURAL
SECTION AND DETAILS

PTA Drawing No: 12-A-152-ST0262

REV : 0

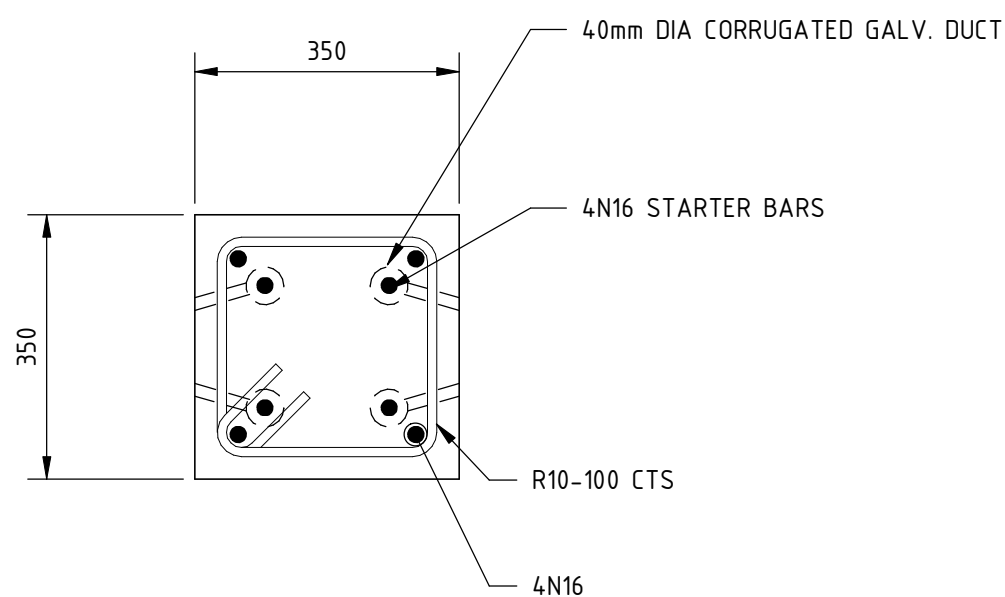

SECTION A-1
1 : 10

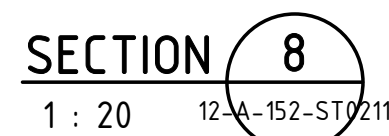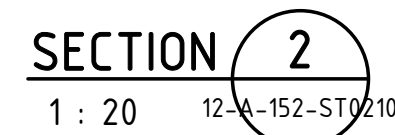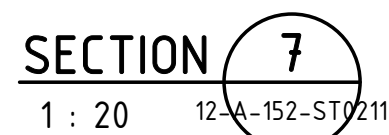

1. THIS DRAWING SHALL BE READ IN CONJUNCTION WITH THE DISCIPLINE CONTRACT SPECIFICATION AND OTHER PROJECT DOCUMENTS.
2. DRAWINGS AND DESIGNS UNDERTAKEN BY A SHOP DETAILER SHALL BE PRESENTED TO THE PTA FOR REVIEW AND CONCURRENCE THAT THE DESIGN INTENT HAS BEEN ACHIEVED.
3. THE CONTRACTORS SHALL BE FULLY AWARE OF THE OTHER INTERFACING PACKAGES AND SHALL HAVE DEEMED TO HAVE INCLUDED INTER-TRADE INTERFACES. THE INTERFACES IDENTIFIED IN THE DOCUMENTATION ARE TO INDICATE AN INTENT AND ARE NOT INTENDED TO BE EXHAUSTIVE. MAKE ALLOWANCES AS REQUIRED.

PTA Drawing No: 12-A-152-ST0270	REV : 0
---------------------------------	---------

[illegible]

aurecon
www.aurecongroup.com


505695-0000-DRG-ST-1810

REFERENCES


SCALE :	As indicated (@ A1)
DATUM :	HORIZONTAL: PCG94 VERTICAL: AHD71

PTA ACCEPTANCE STAMP


DESIGNED	J.SPANO
DRAWN	A.DAWSON
CHECKED	M.PEARCE
APPROVED FOR ISSUE	
G.BENTLEY	
DATE	

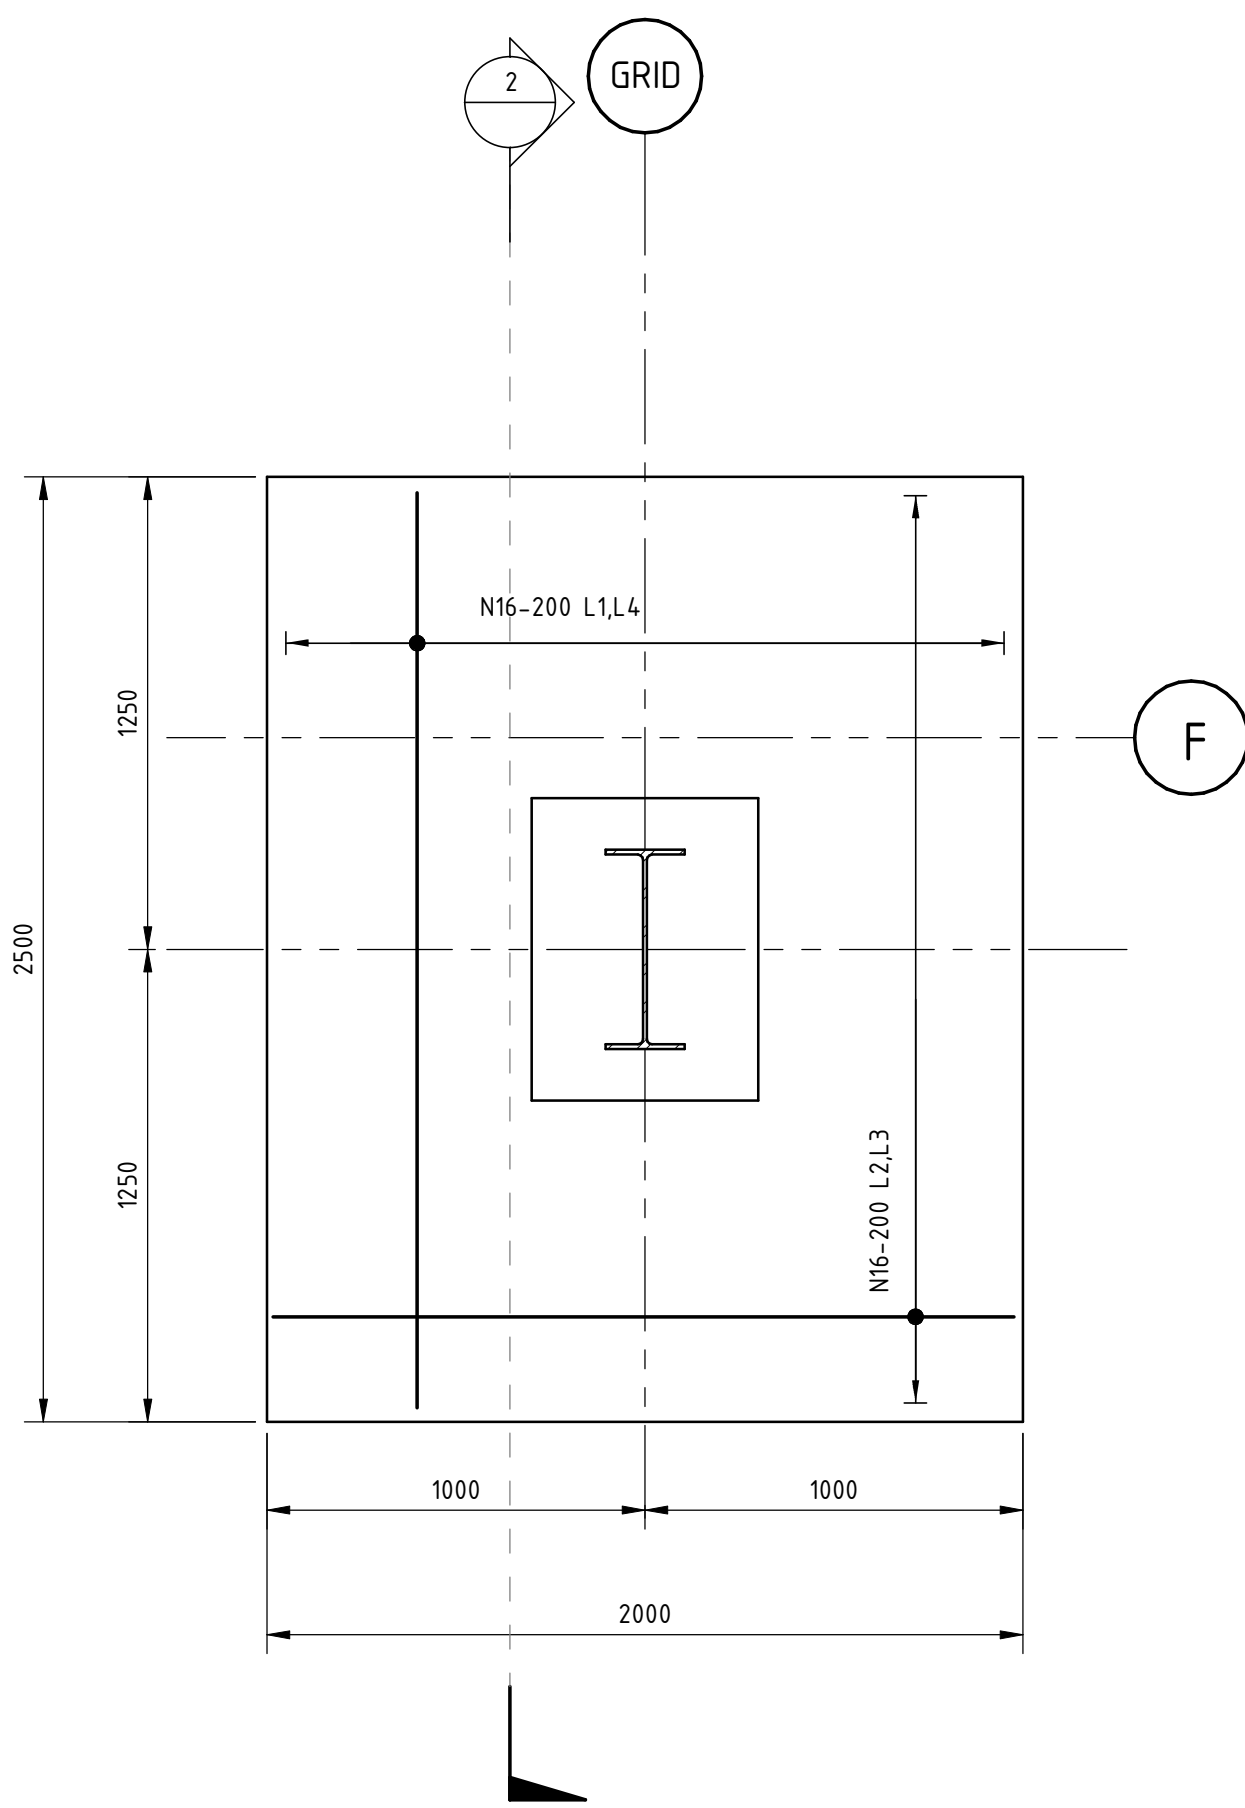


PF1 PAD FOOTING PLAN

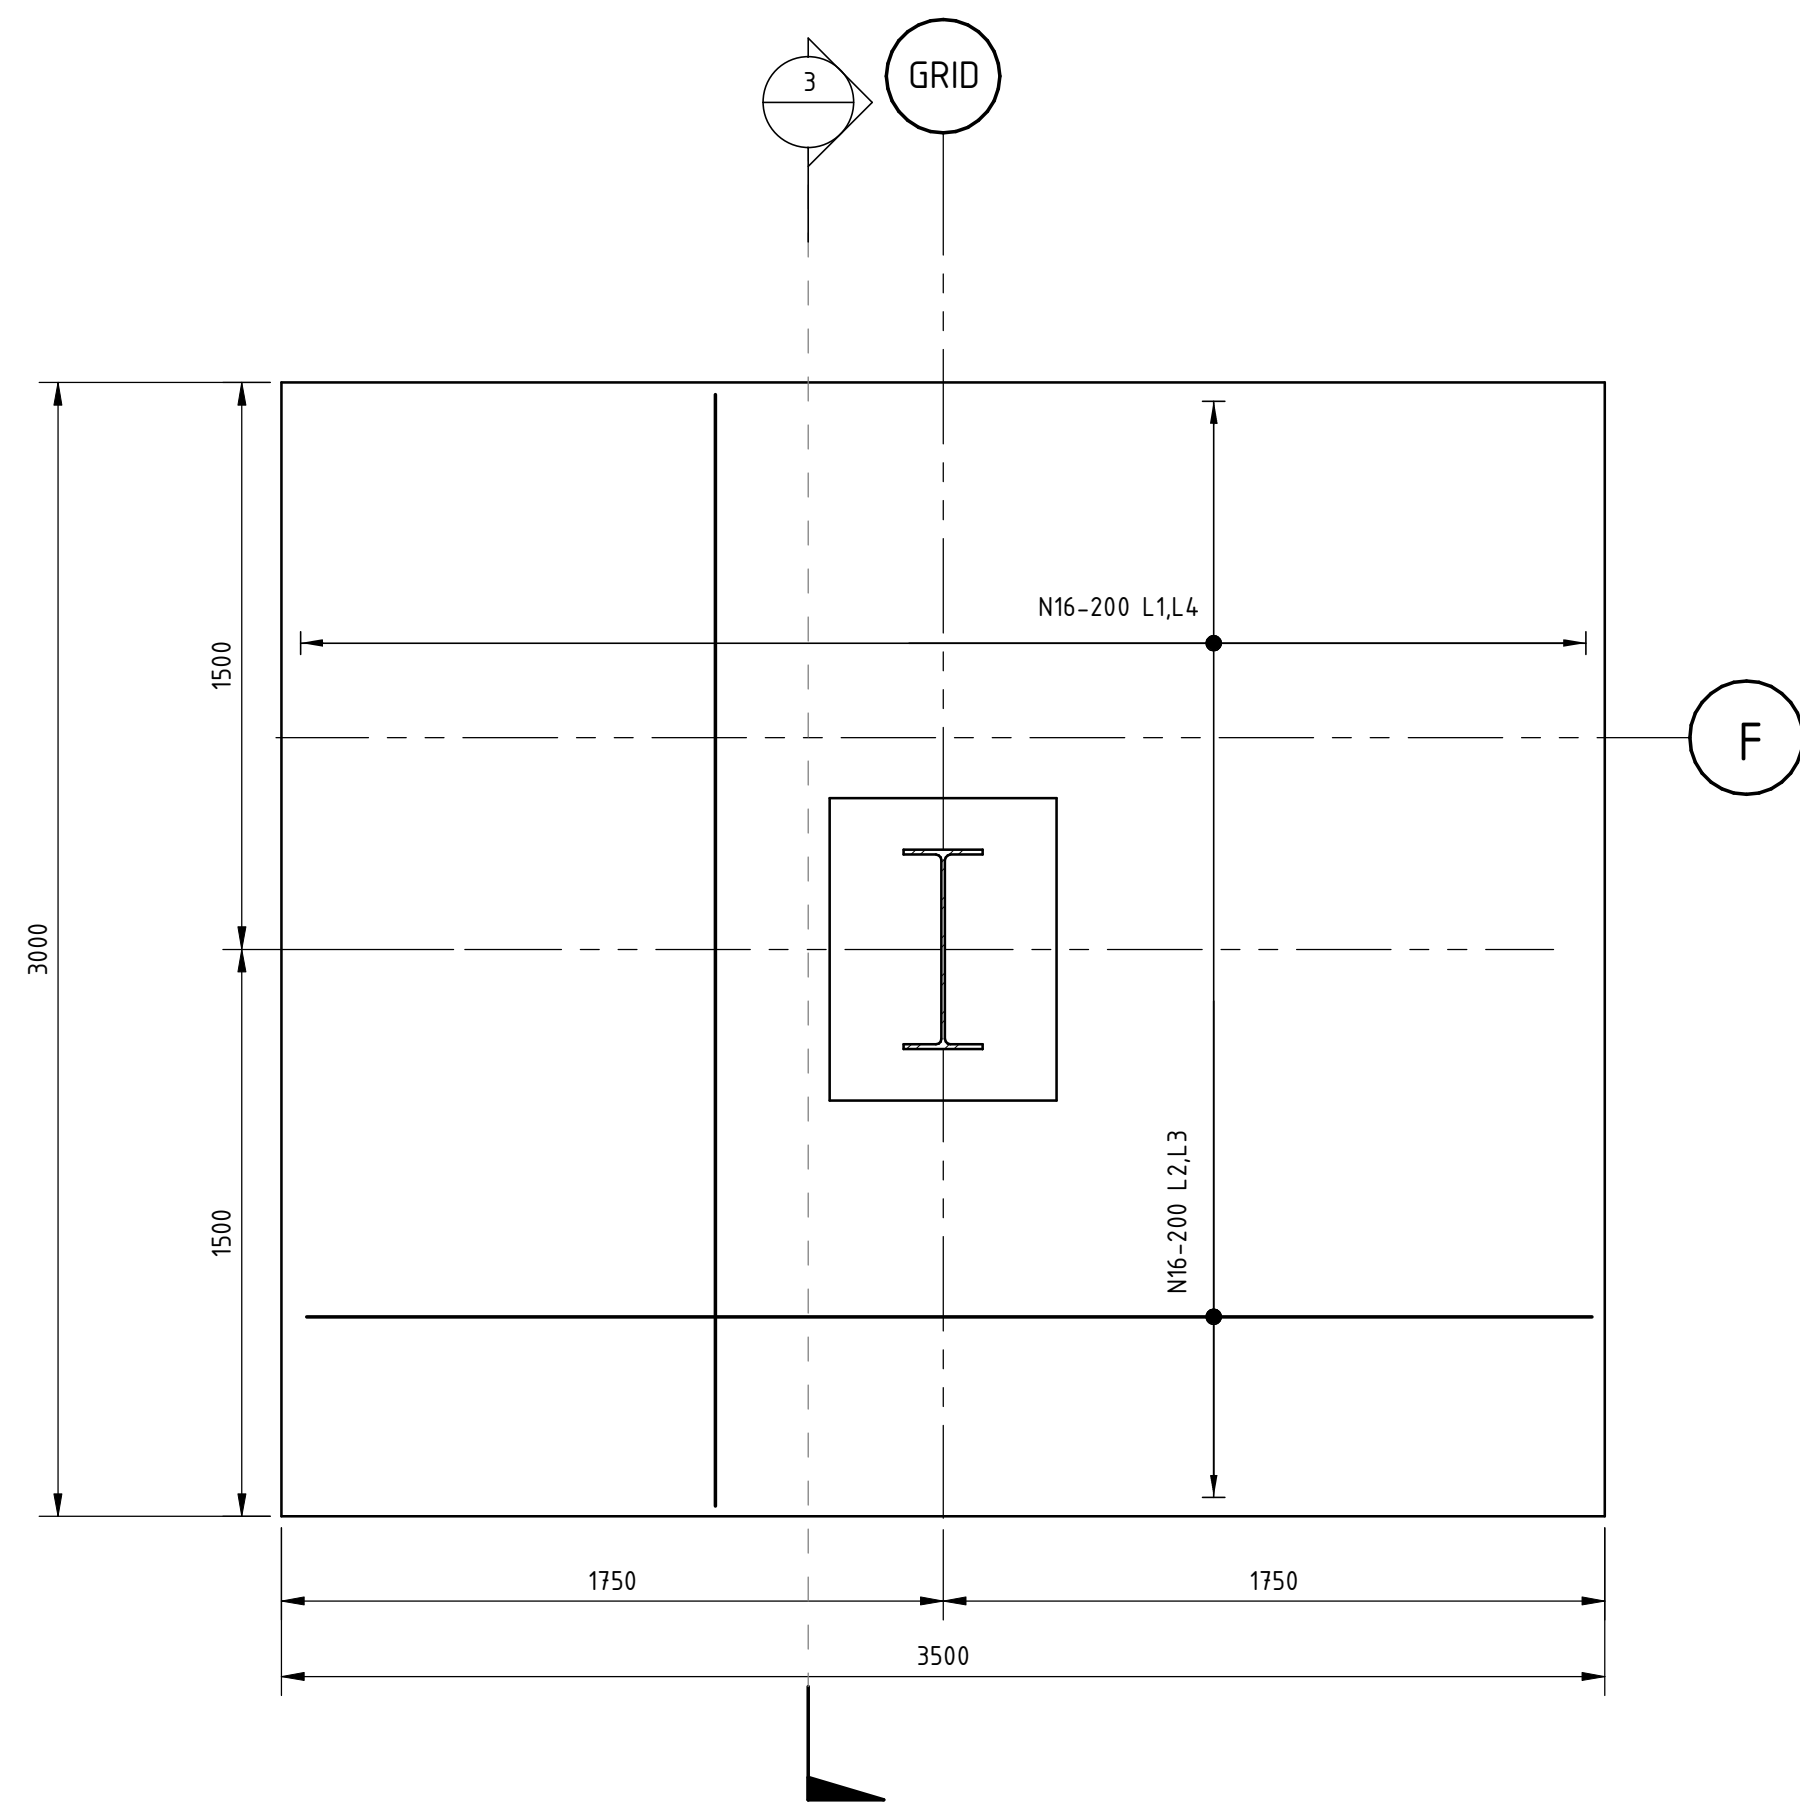


PF2 PAD FOOTING PLAN

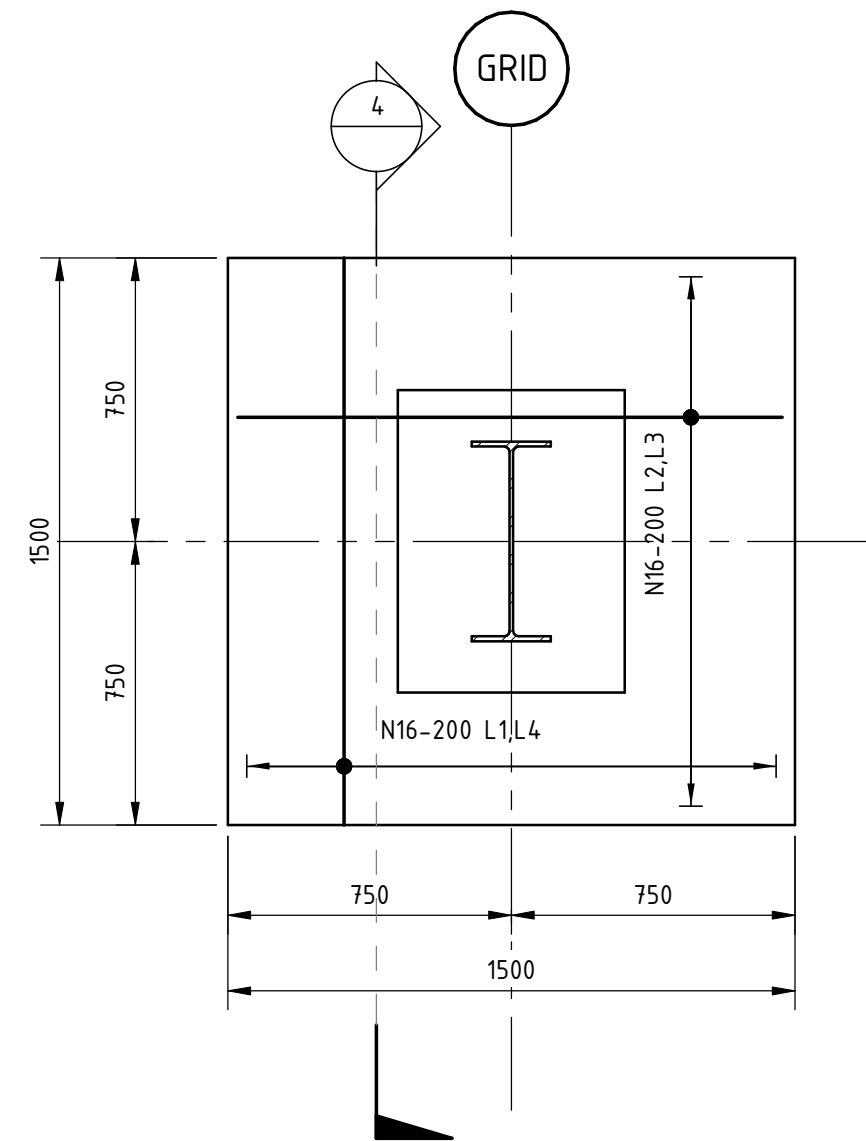


PF3 PAD FOOTING PLAN

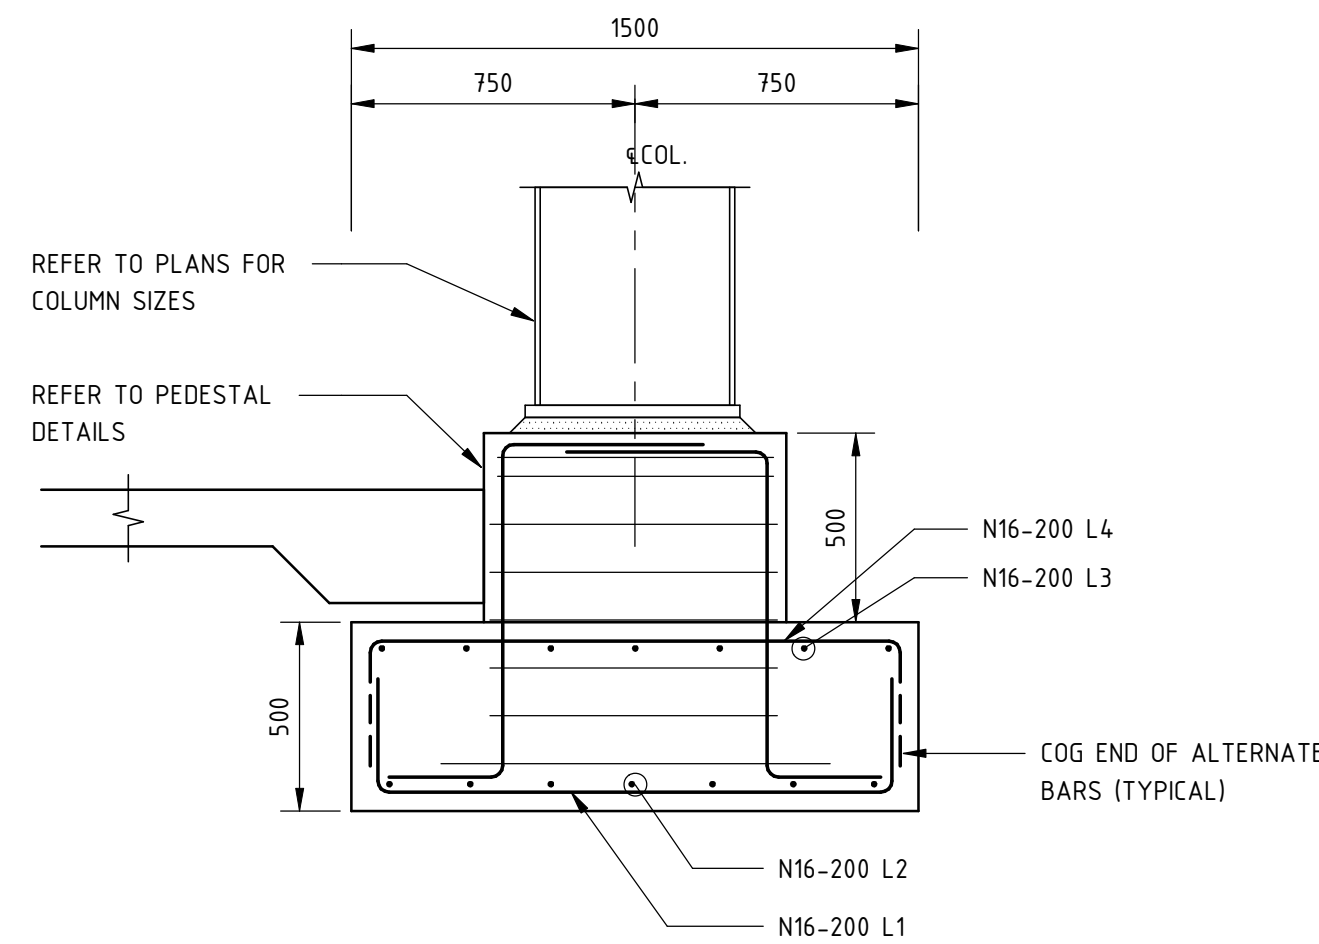


SECTION 4
1 : 20

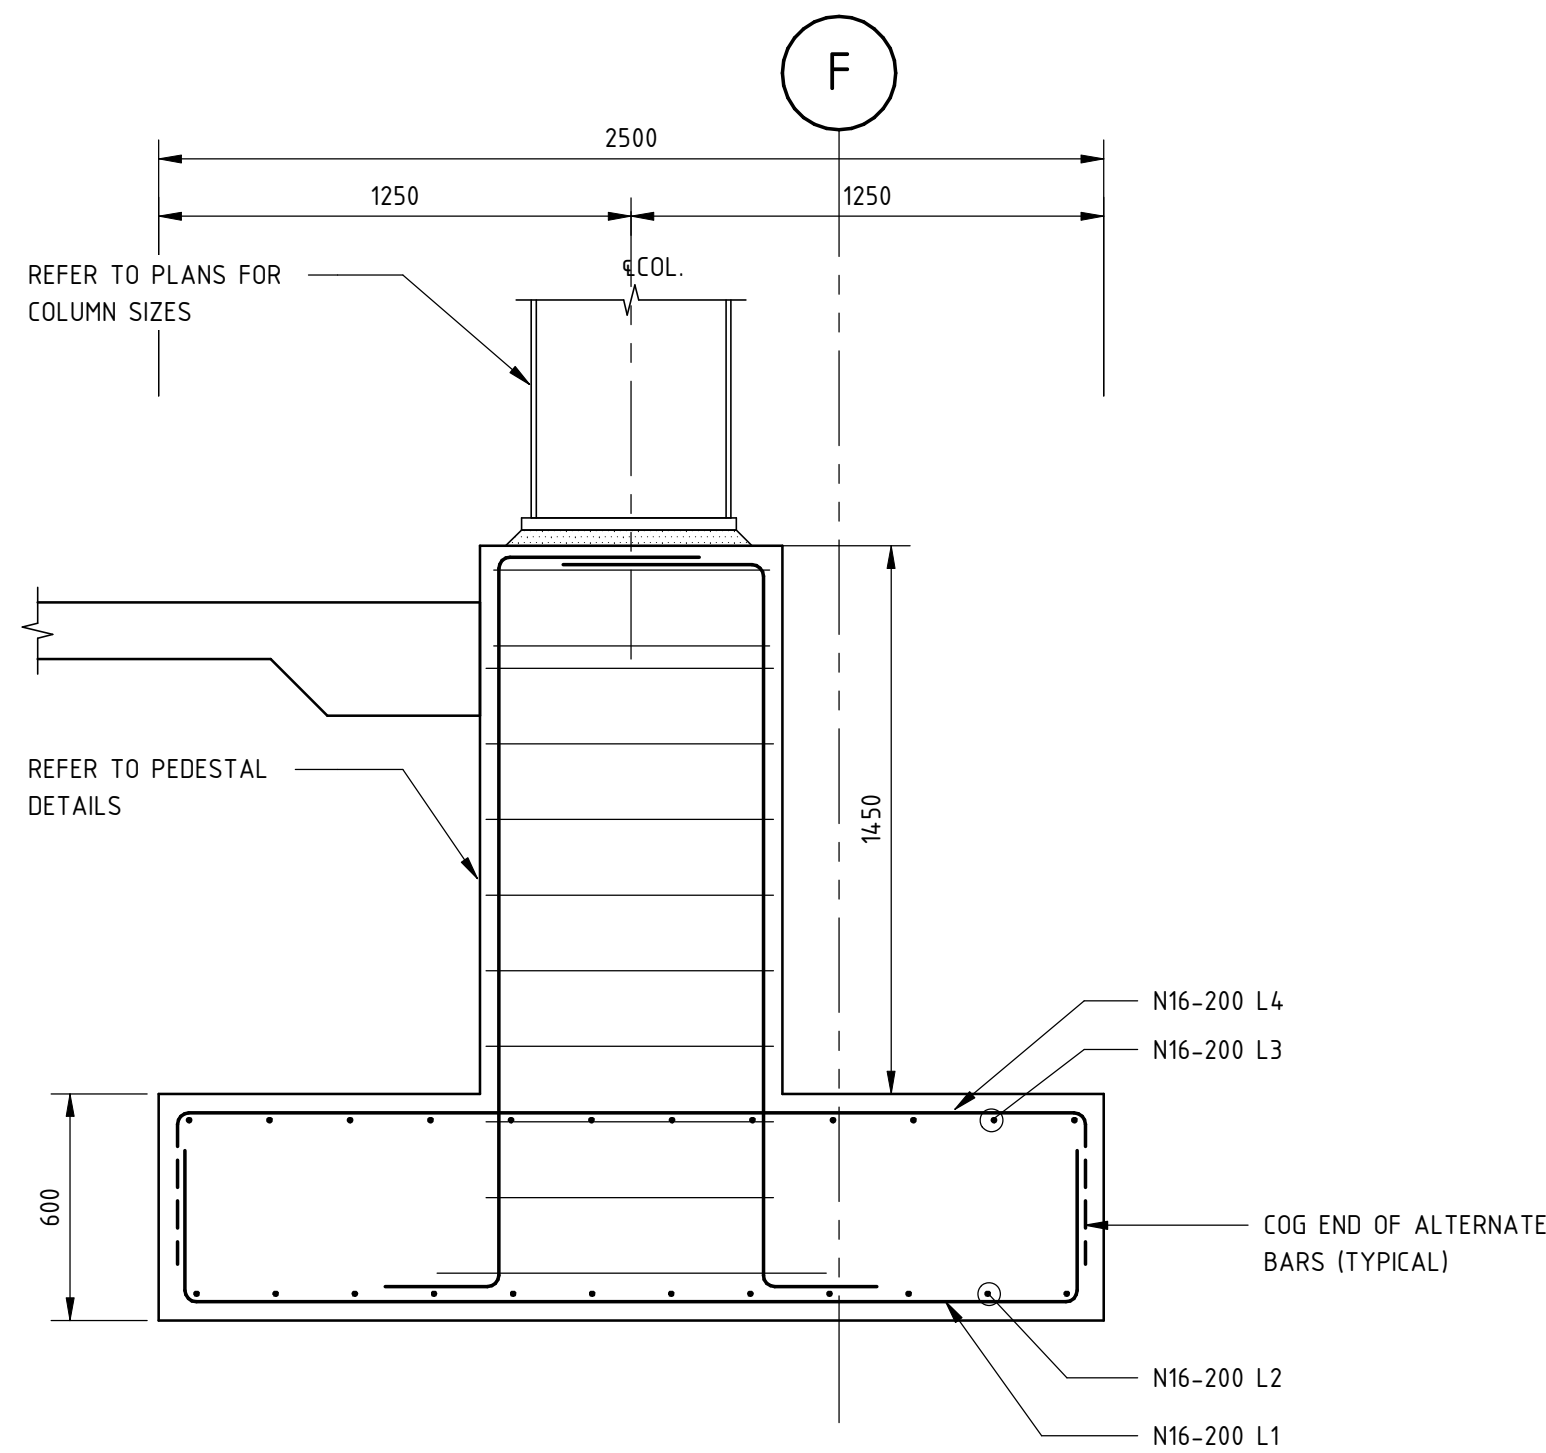

SECTION 2
1 : 20

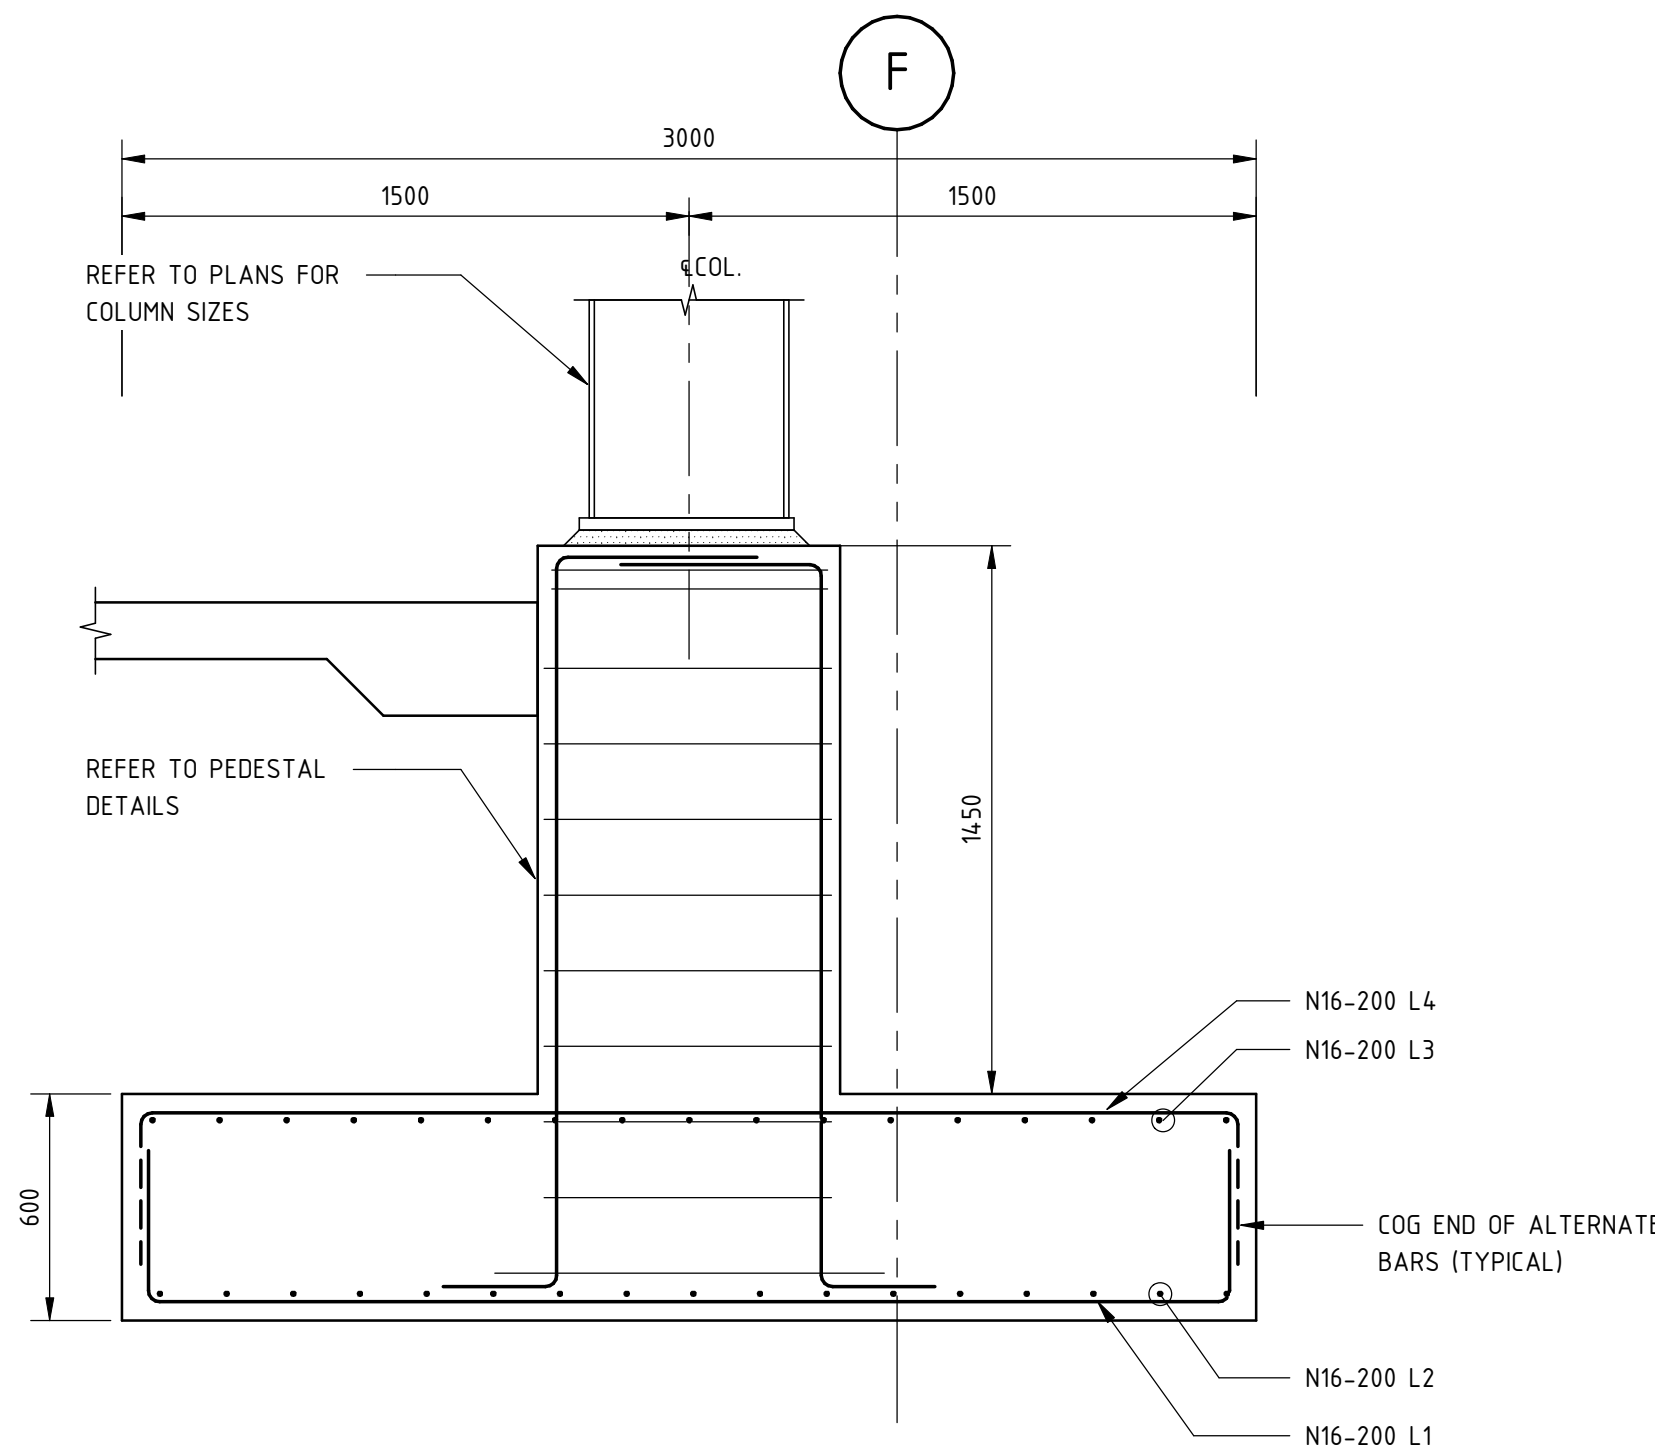

SECTION 3
1 : 20

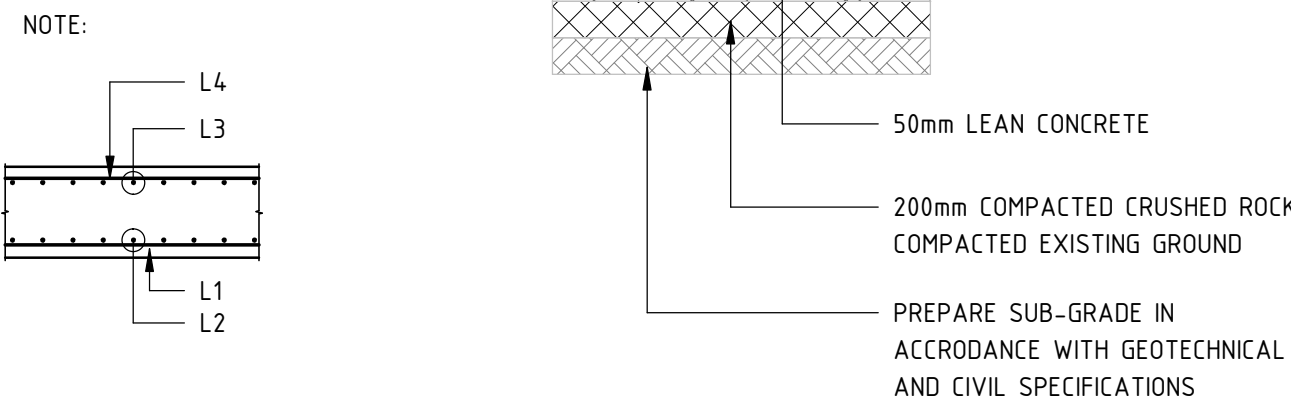

REINFORCEMENT KEY TYPICAL COMPACTION DETAIL

- USE OF THESE DRAWINGS
- THIS DRAWING SHALL BE READ IN CONJUNCTION WITH THE DISCIPLINE CONTRACT SPECIFICATION AND OTHER PROJECT DOCUMENTS.
 - DRAWINGS AND DESIGNS UNDERTAKEN BY A SHOP DETAILER SHALL BE PRESENTED TO THE PTA FOR REVIEW AND CONCURRENCE THAT THE DESIGN INTENT HAS BEEN ACHIEVED.
 - THE CONTRACTORS SHALL BE FULLY AWARE OF THE OTHER INTERFACING PACKAGES AND SHALL HAVE DEEMED TO HAVE INCLUDED INTER-TRADE INTERFACES. THE INTERFACES IDENTIFIED IN THE DOCUMENTATION ARE TO INDICATE AN INTENT AND ARE NOT INTENDED TO BE EXHAUSTIVE. MAKE ALLOWANCES AS REQUIRED.

ISSUED FOR CONSTRUCTION

REV	DATE	AMENDMENT	DSN	DRN	CHKD	APP
0	01.10.19	ISSUED FOR CONSTRUCTION	J.S.	A.C.D.	M.P.	G.B.
A1						

Plot Date: 10/1/2019 9:26:14 AM Office: PERTH Filename: BIM 360://505695 - Bellevue Depot/505695-ST-BELLEVUE DEPOT-028.rvt

aurecon
www.aurecongroup.com




505695-0000-DRG-ST-1811

REFERENCES

SCALE :
As indicated (@ A1)
DATUM :
HORIZONTAL: PC694
VERTICAL: AHD71
PTA ACCEPTANCE STAMP

DESIGNED J.SPANO
DRAWN A.DAWSON
CHECKED M.PEARCE
APPROVED FOR ISSUE
G.BENTLEY
DATE

Government of Western Australia
Public Transport Authority
DETAILED DESIGN FOR THE BELLEVUE DEPOT
HV TESTING FACILITY
STRUCTURAL
SECTIONS AND DETAILS - SHEET 2 OF 7
PTA Drawing No: 12-A-152-ST0271
REV : 0

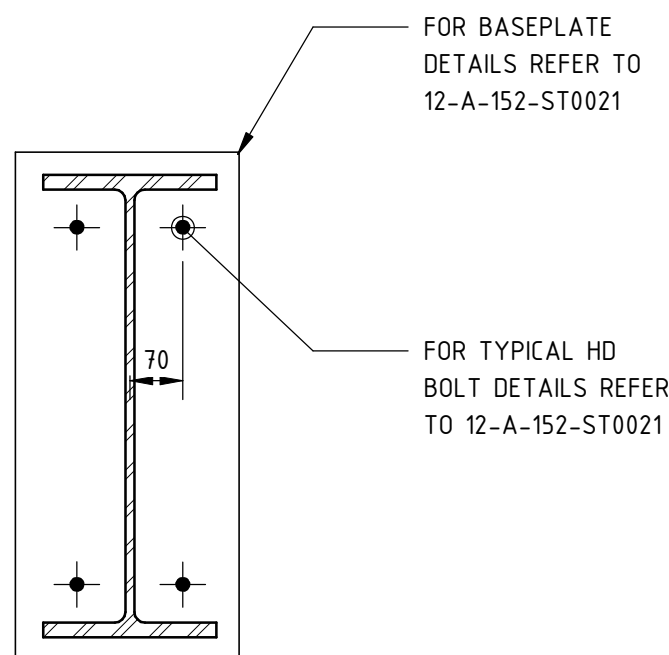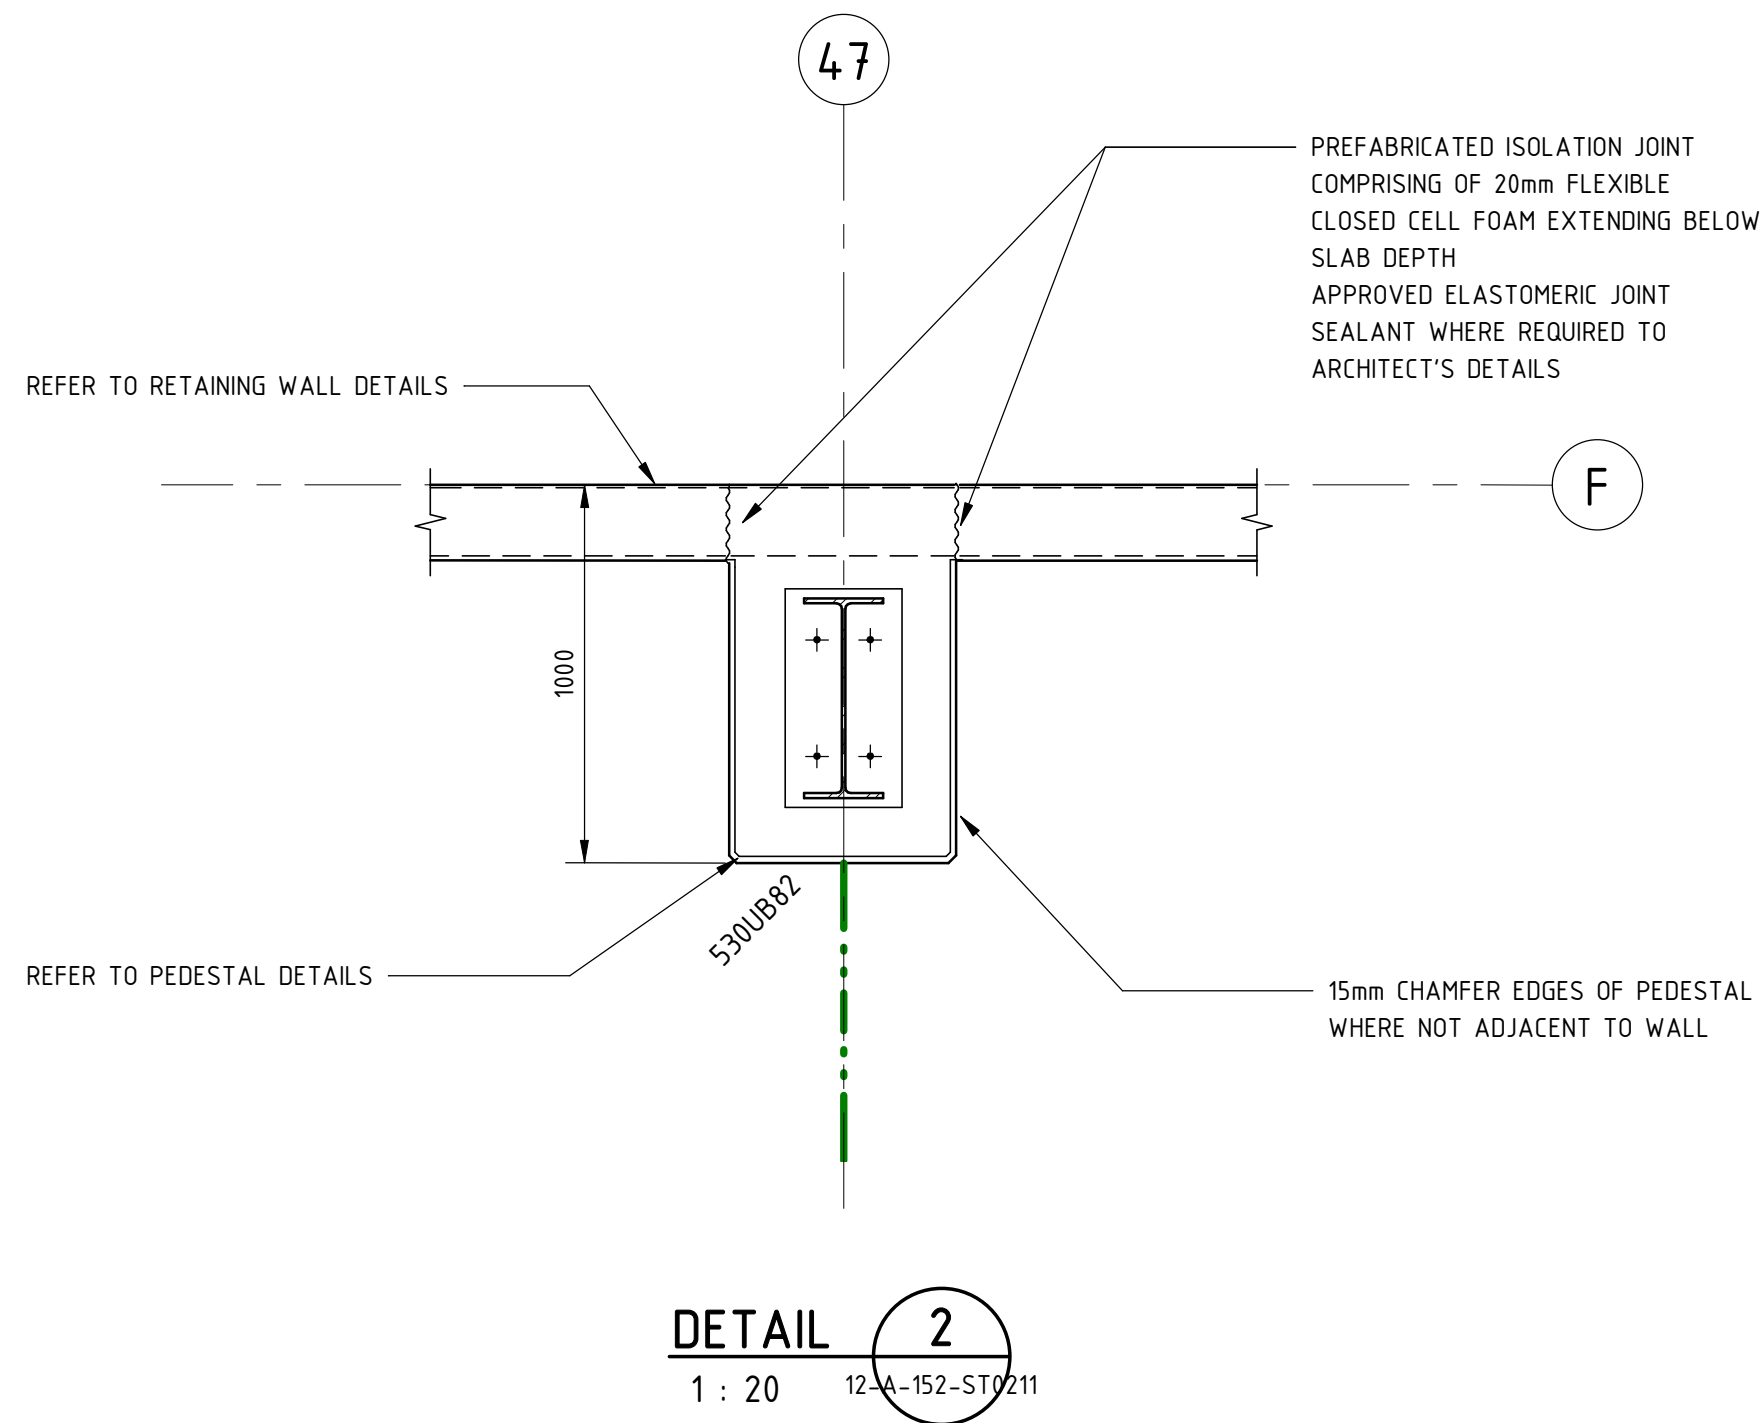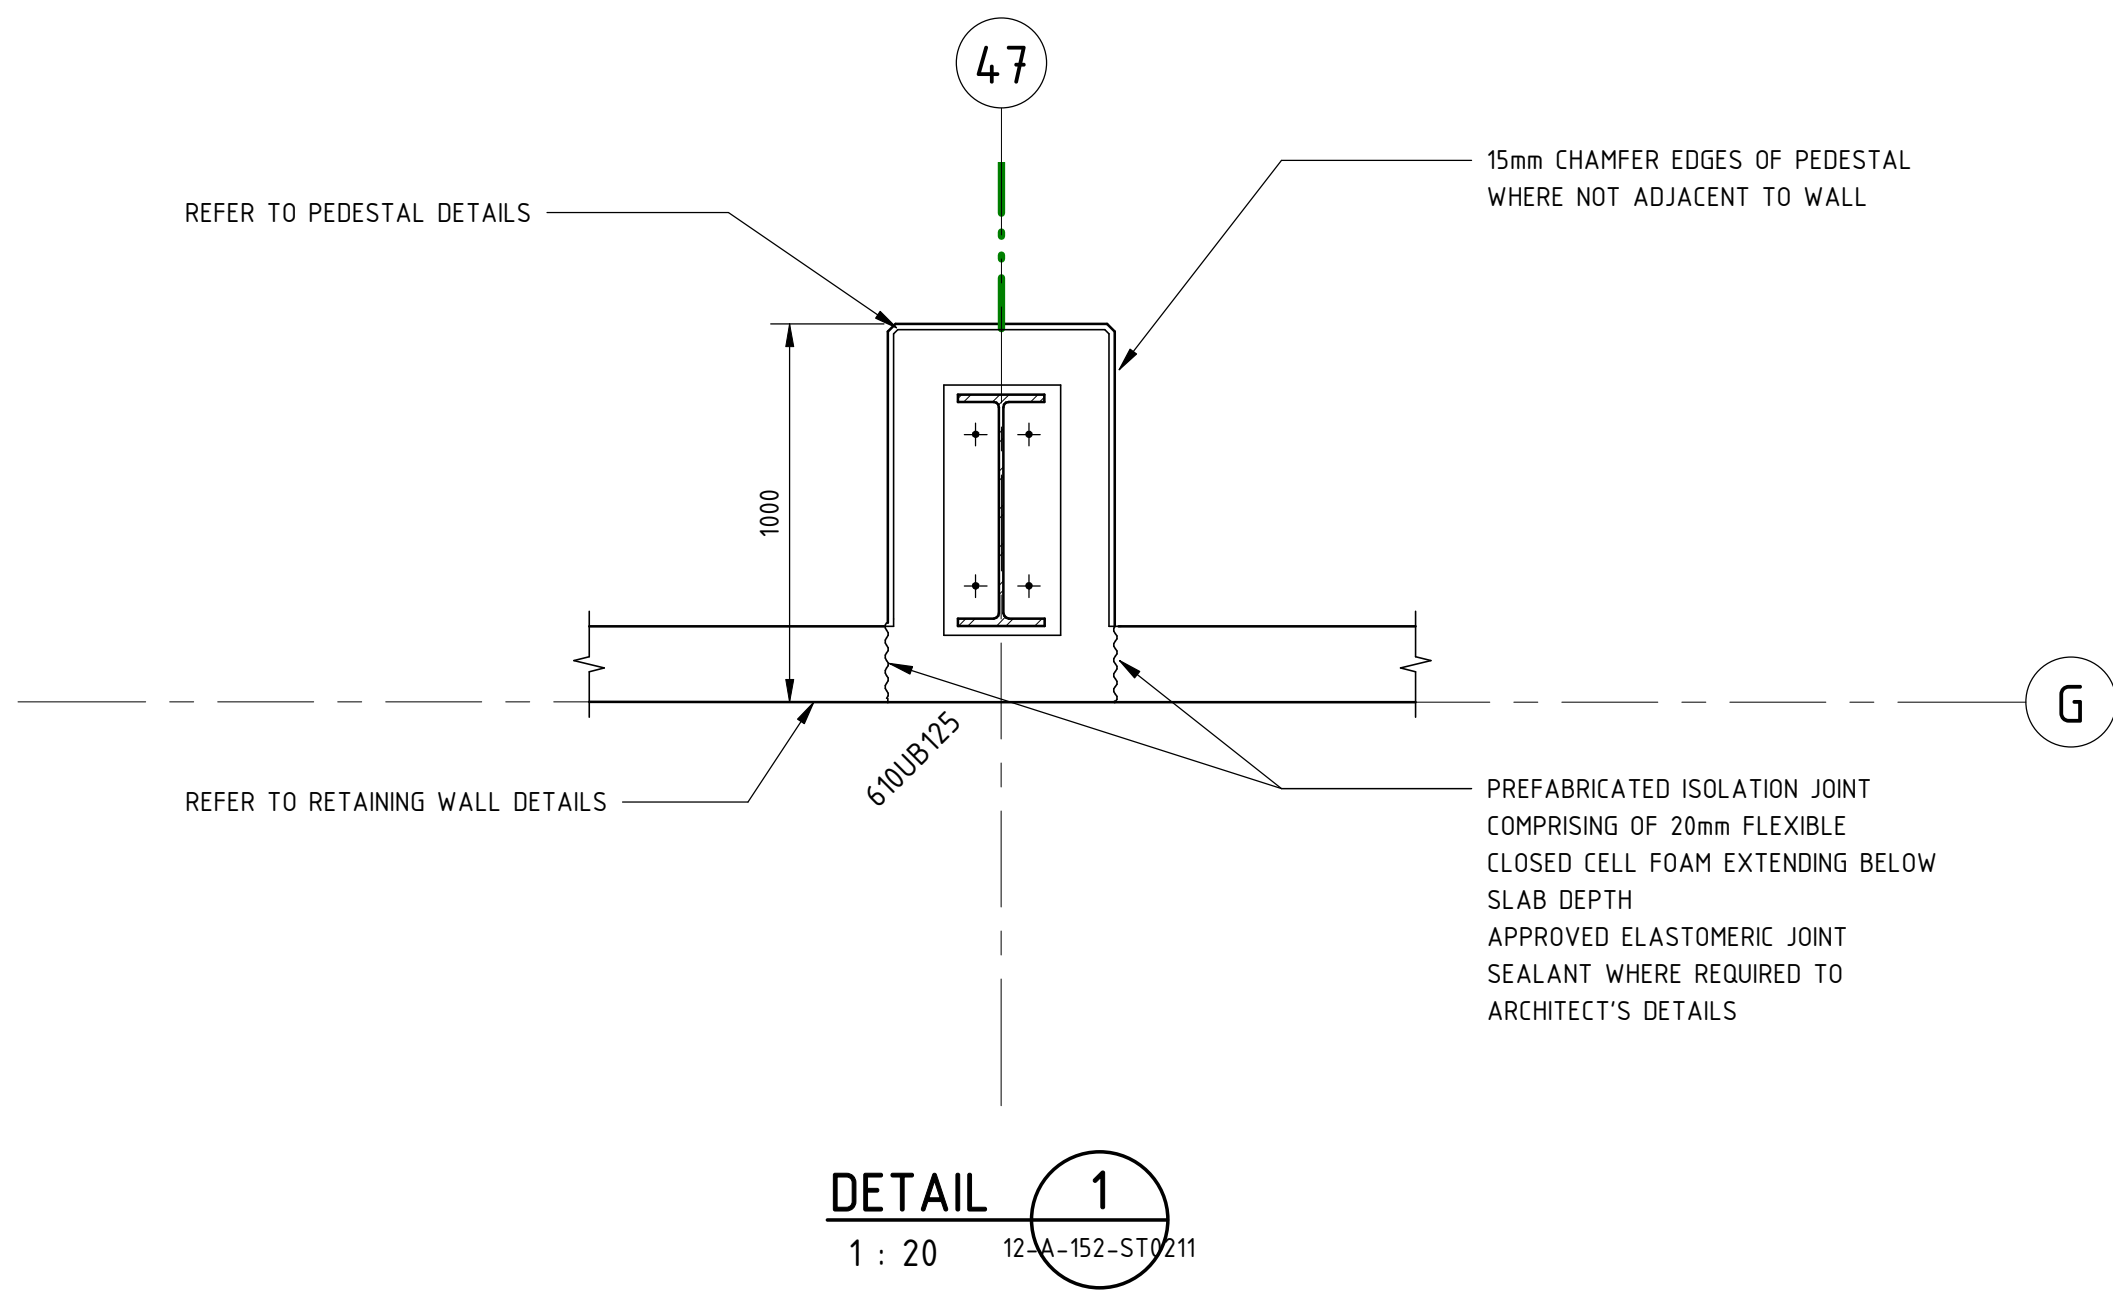

TYPICAL BASEPLATE DETAIL
1 : 10


ZONE PLAN

NOTES:


- DO NO SCALE DRAWINGS. WRITTEN DIMENSIONS GOVERN.
- ALL DIMENSIONS ARE IN MILLIMETRES UNLESS NOTED OTHERWISE
- ALL DIMENSIONS SHALL BE VERIFIED ON SITE BEFORE PROCEEDING WITH THE WORK. RELEVANT PARTY SHALL BE NOTIFIED IN WRITING OF ANY DISCREPANCIES.
- THIS DRAWING MUST BE READ IN CONJUNCTION WITH ALL RELEVANT CONTRACTS, SPECIFICATIONS, REPORTS AND DRAWINGS.

NOTES:


- REFER TO PLANS FOR PEDESTAL SET OUT AND PAD FOOTING DETAILS
- PROVIDE ADDITIONAL SET OF TIES WITH 100mm FROM TOP OF PEDESTAL
- FIRST SET OR PEDESTAL TIES TO BE A MAX 50MM FROM BASE OF PEDESTAL
- PROVIDE MIN. 2 SETS OF TIES TO PEDESTAL STARTER BARS WITHIN PAD DEPTH
- PAD REINFORCEMENT OMITTED FOR CLARITY
- THIS DRAWING SHOULD BE READ IN CONJUNCTION WITH THE STANDARD DETAILS AND NOTES
- REFER TO 12-A-152-ST003 FOR GENERAL CONCRETE NOTES
- REFER TO 12-A-152-ST0010 & ST0011 FOR STEEL REINFORCEMENT AND CONCRETE DETAILS

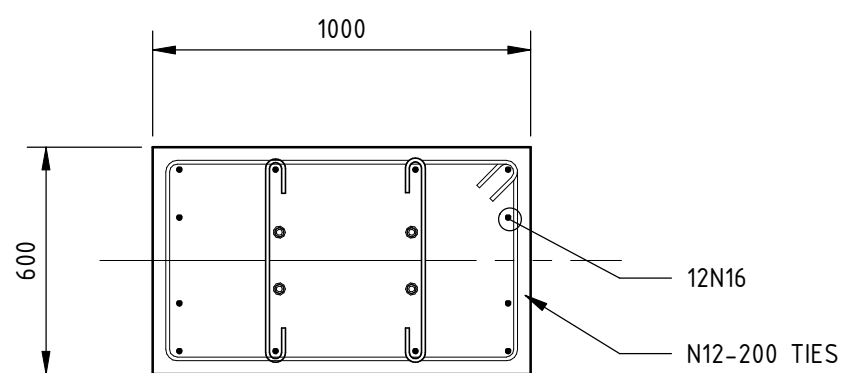


TYPICAL SECTION THROUGH P1

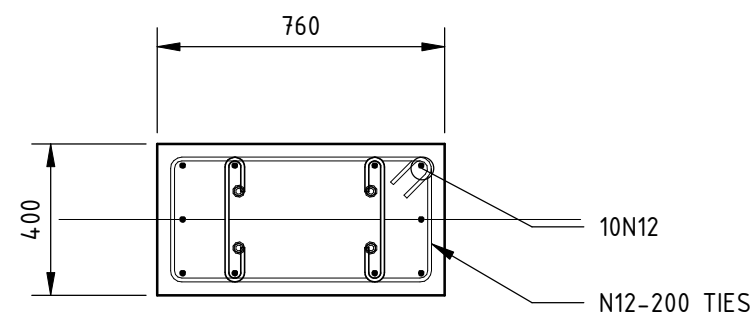

TYPICAL SECTION THROUGH P2

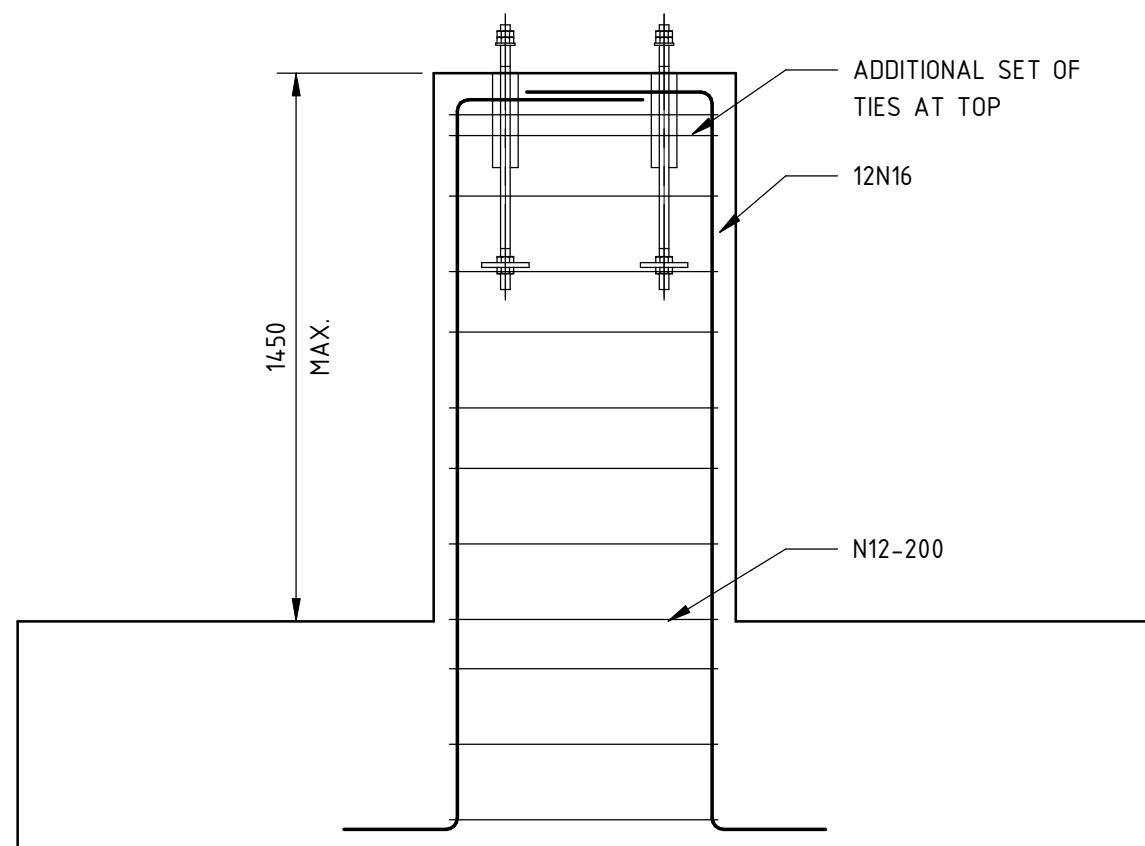

SECTION THROUGH P1

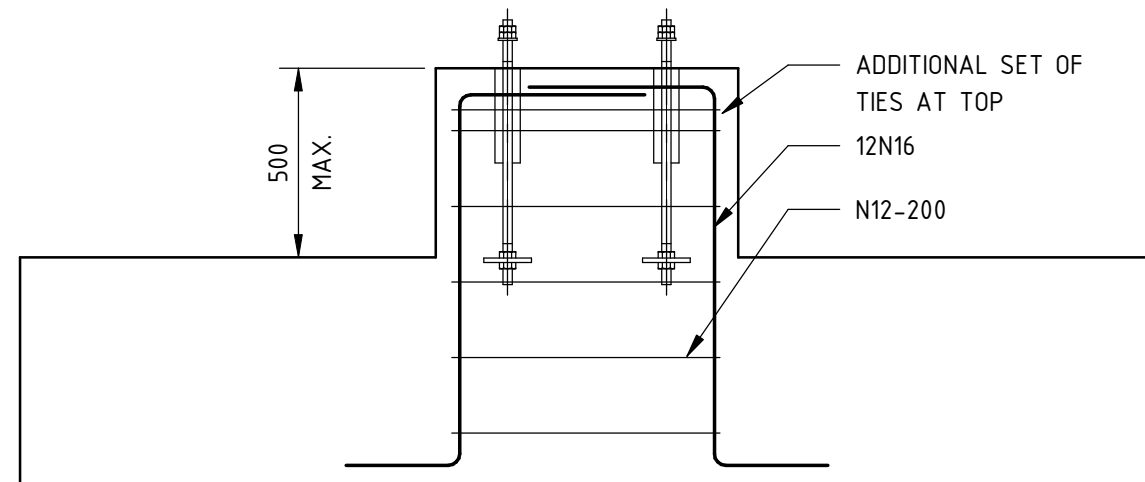

SECTION THROUGH P2

USE OF THESE DRAWINGS

- THIS DRAWING SHALL BE READ IN CONJUNCTION WITH THE DISCIPLINE CONTRACT SPECIFICATION AND OTHER PROJECT DOCUMENTS.
- DRAWINGS AND DESIGNS UNDERTAKEN BY A SHOP DETAILER SHALL BE PRESENTED TO THE PTA FOR REVIEW AND CONCURRENCE THAT THE DESIGN INTENT HAS BEEN ACHIEVED.
- THE CONTRACTORS SHALL BE FULLY AWARE OF THE OTHER INTERFACING PACKAGES AND SHALL HAVE DEEMED TO HAVE INCLUDED INTER-TRADE INTERFACES. THE INTERFACES IDENTIFIED IN THE DOCUMENTATION ARE TO INDICATE AN INTENT AND ARE NOT INTENDED TO BE EXHAUSTIVE. MAKE ALLOWANCES AS REQUIRED.

ISSUED FOR CONSTRUCTION

REV	DATE	AMENDMENT	DSN	DRN	CHKD	APP
0	01.10.19	ISSUED FOR CONSTRUCTION	J.S.	A.C.D.	M.P.	G.B.
A1						

SCALE 1:20 AT A1

0 0.2 0.4 0.6 0.8 1 2m

This document must not be copied without PTA's written permission, and the contents thereof must not be imparted to a third party nor be used for any unauthorised purpose.

aurecon
www.aurecongroup.com

505695-0000-DRG-ST-1812

REFERENCES

SCALE :
As indicated (@ A1)
DATUM :
HORIZONTAL: PC694
VERTICAL: AHD71
PTA ACCEPTANCE STAMP

DESIGNED J.SPANO
DRAWN A.DAWSON
CHECKED M.PEARCE
APPROVED FOR ISSUE
G.BENTLEY
DATE





DETAILED DESIGN FOR THE BELLEVUE DEPOT

HV TESTING FACILITY
STRUCTURAL
SECTIONS AND DETAILS - SHEET 3 OF 7

PTA Drawing No: 12-A-152-ST0272 REV : 0

1. DO NO SCALE DRAWINGS. WRITTEN DIMENSIONS GOVERN.
2. ALL DIMENSIONS ARE IN MILLIMETRES UNLESS NOTED OTHERWISE
3. ALL DIMENSIONS SHALL BE VERIFIED ON SITE BEFORE PROCEEDING WITH THE WORK. RELEVANT PARTY SHALL BE NOTIFIED IN WRITING OF ANY DISCREPANCIES.
4. THIS DRAWING MUST BE READ IN CONJUNCTION WITH ALL RELEVANT CONTRACTS, SPECIFICATIONS, REPORTS AND DRAWINGS.

1. REFER TO 12-A-152-ST003 FOR GENERAL CONCRETE NOTES
2. REFER TO 12-A-152-ST0010 & ST0011 FOR STEEL REINFORCEMENT AND CONCRETE DETAILS

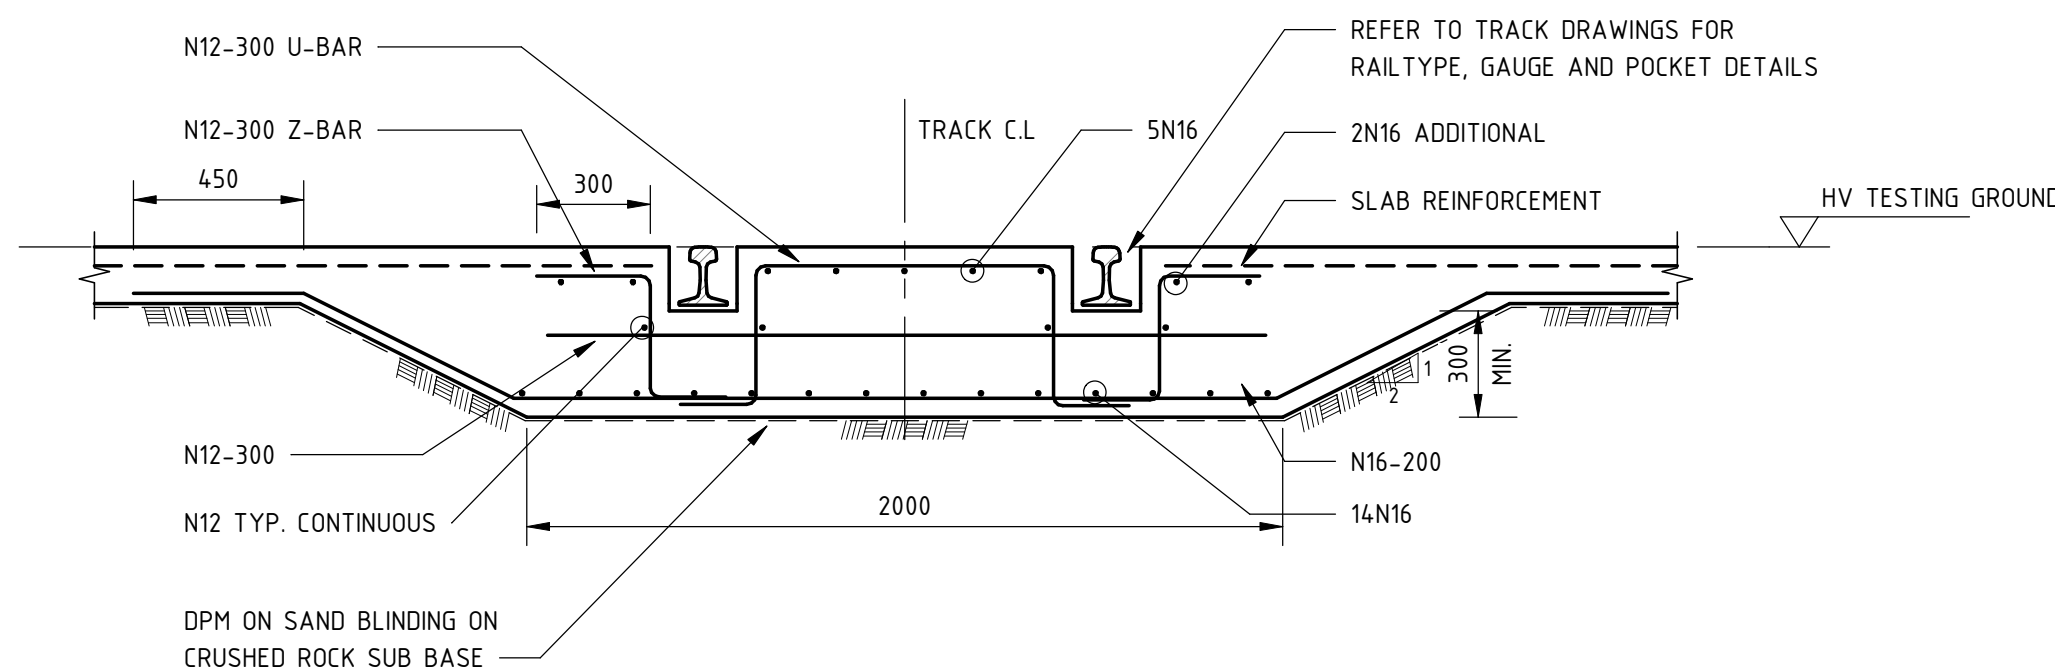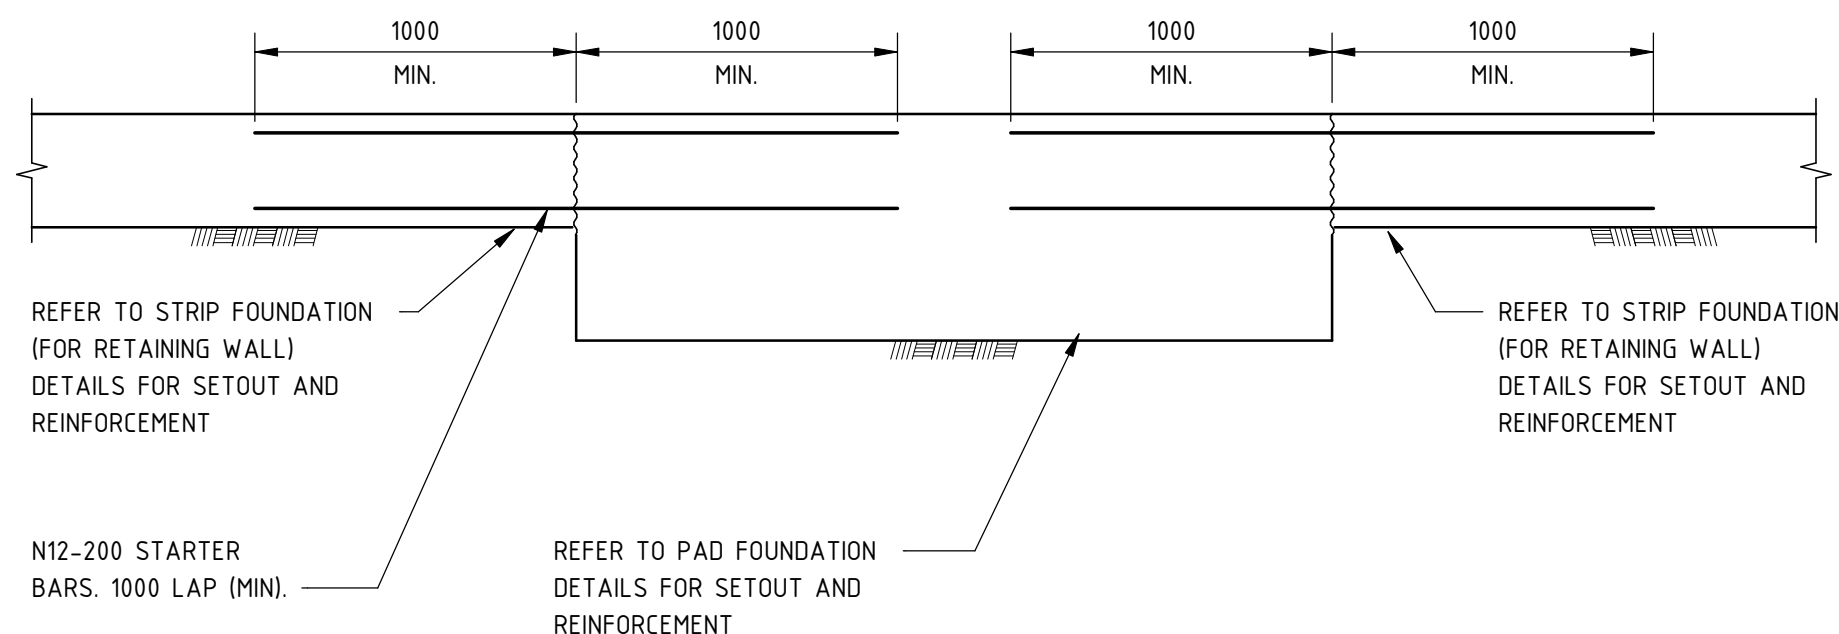

1 : 20

[illegible]

505695-0000-DRG-ST-1813

REFERENCES


SCALE :
As indicated (@ A1)

DATUM :
HORIZONTAL: PCG94
VERTICAL: AHD71


PTA ACCEPTANCE STAMP

DESIGNED	J.SPANO
DRAWN	A.DAWSON
CHECKED	M.PEARCE
APPROVED FOR ISSUE	
G.BENTLEY	
DATE	

Government of Western Australia Public Transport Authority	DETAILED DESIGN FOR THE BELLEVUE DEPOT
HV TESTING FACILITY STRUCTURAL SECTIONS AND DETAILS - SHEET 4 OF 7	
PTA Drawing No: 12-A-152-ST0273	REV : 0

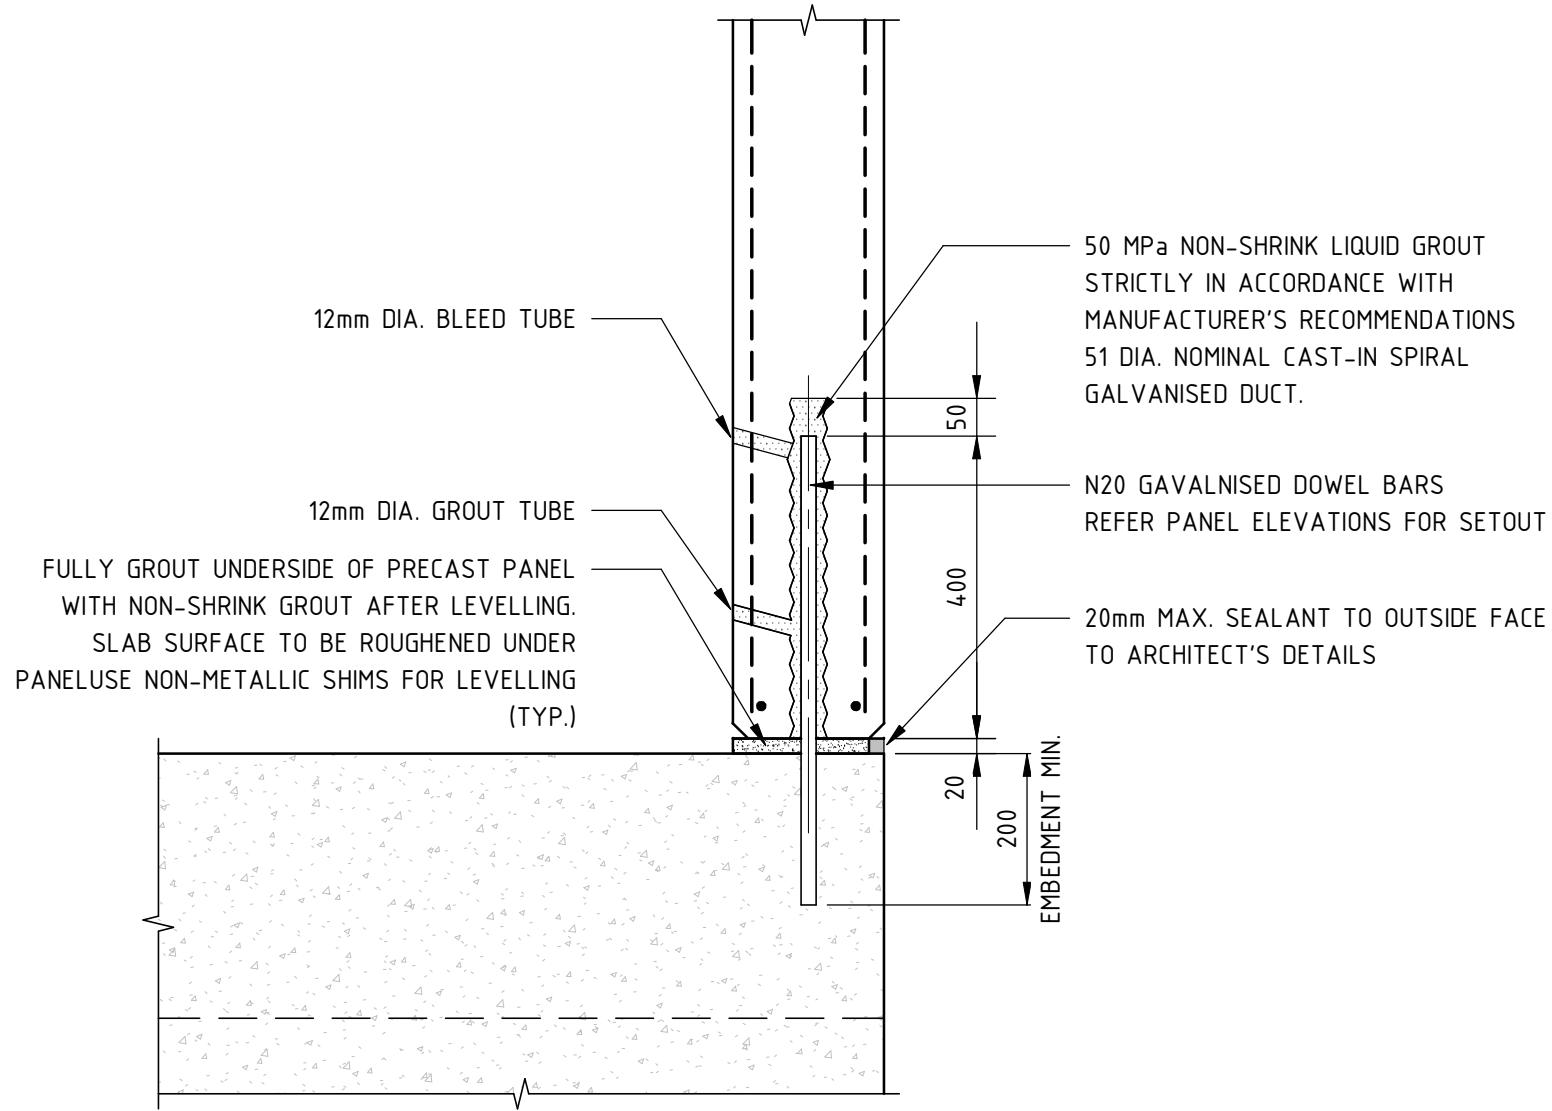


CONNECTION TYPE PC-CN01

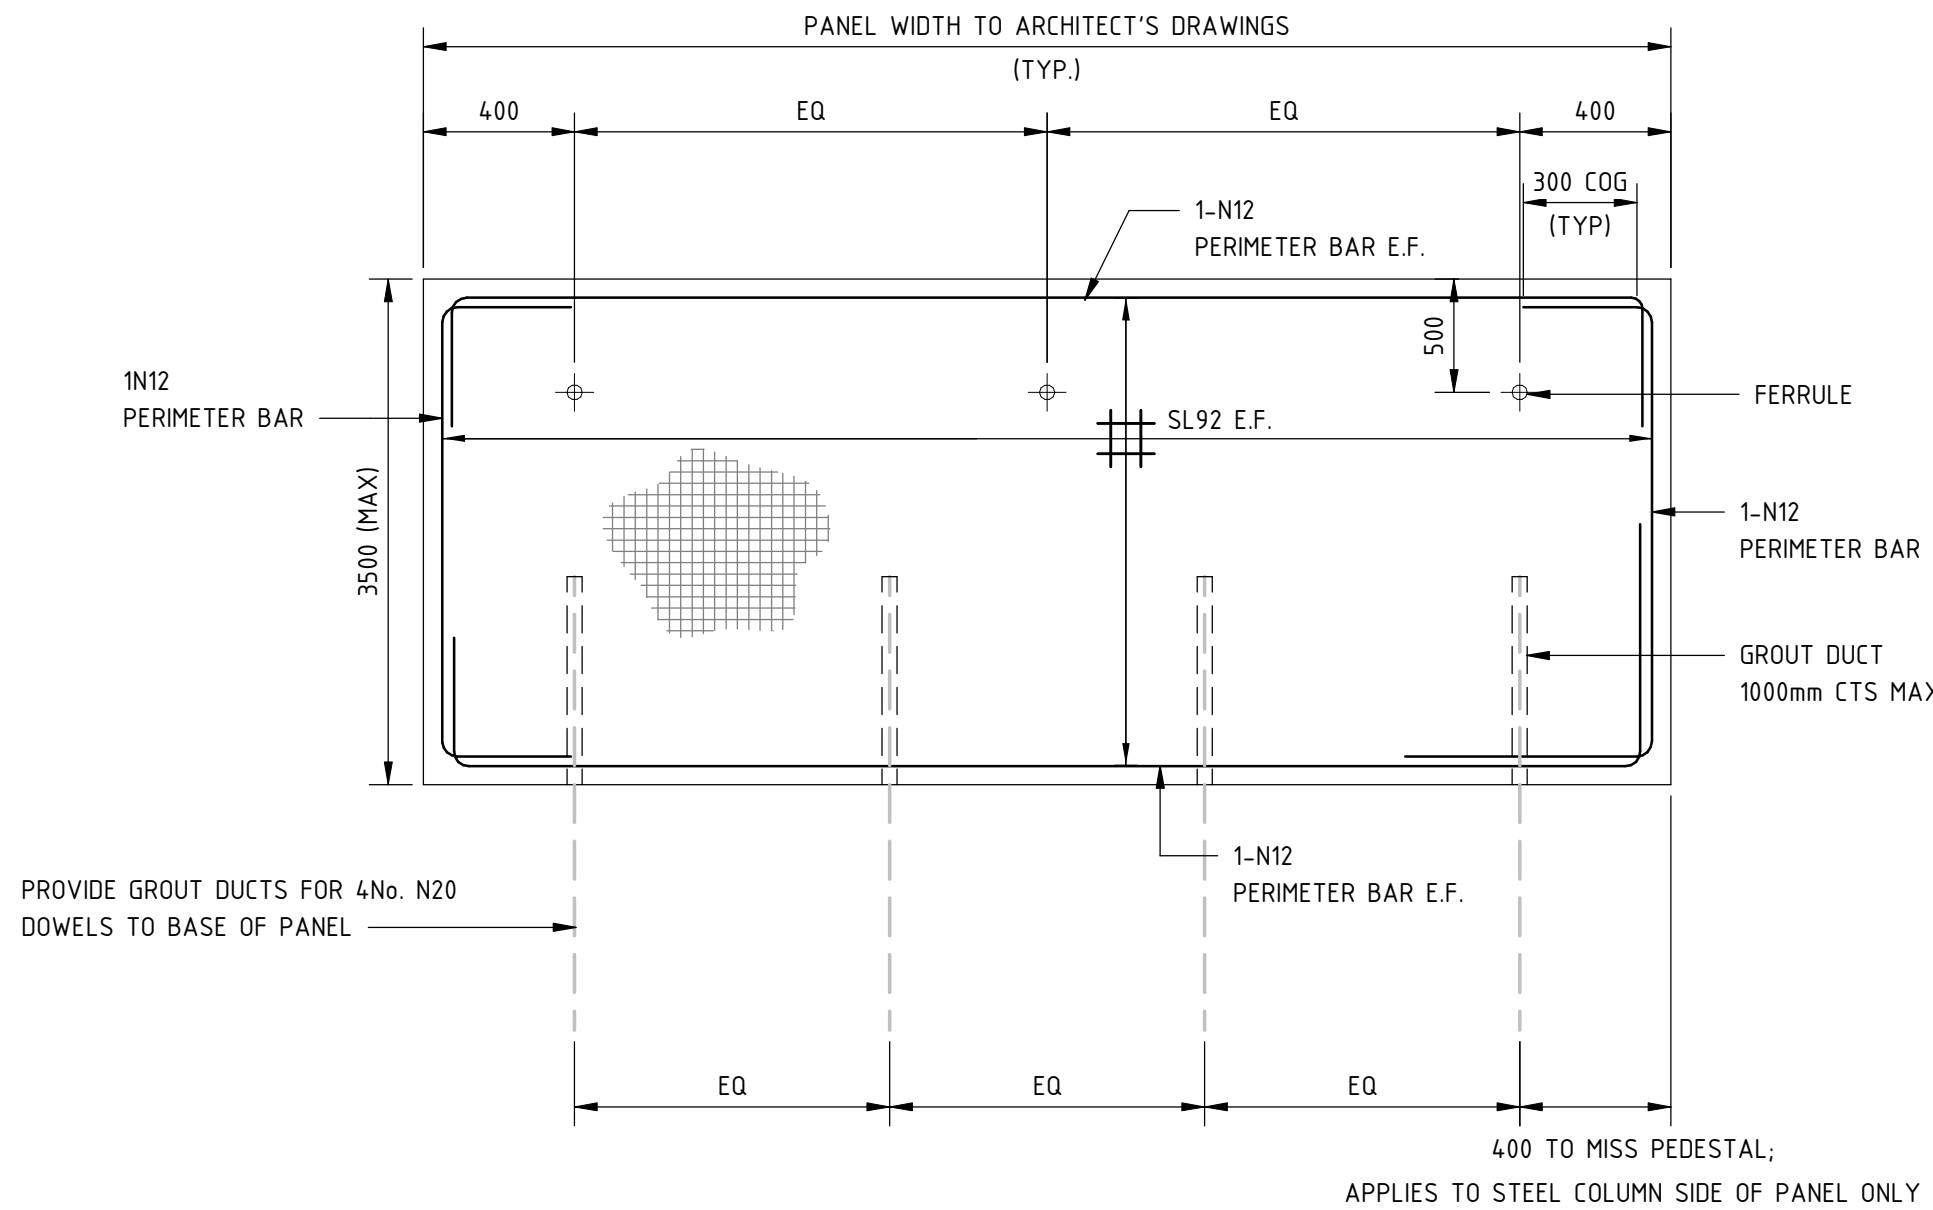


TYPICAL PANEL TYPE "PC01"

PRECAST PANEL: 150 STRUCTURAL THICKNESS

- BASE CONNECTION: PCN01
- TOP CONNECTION: PCN02

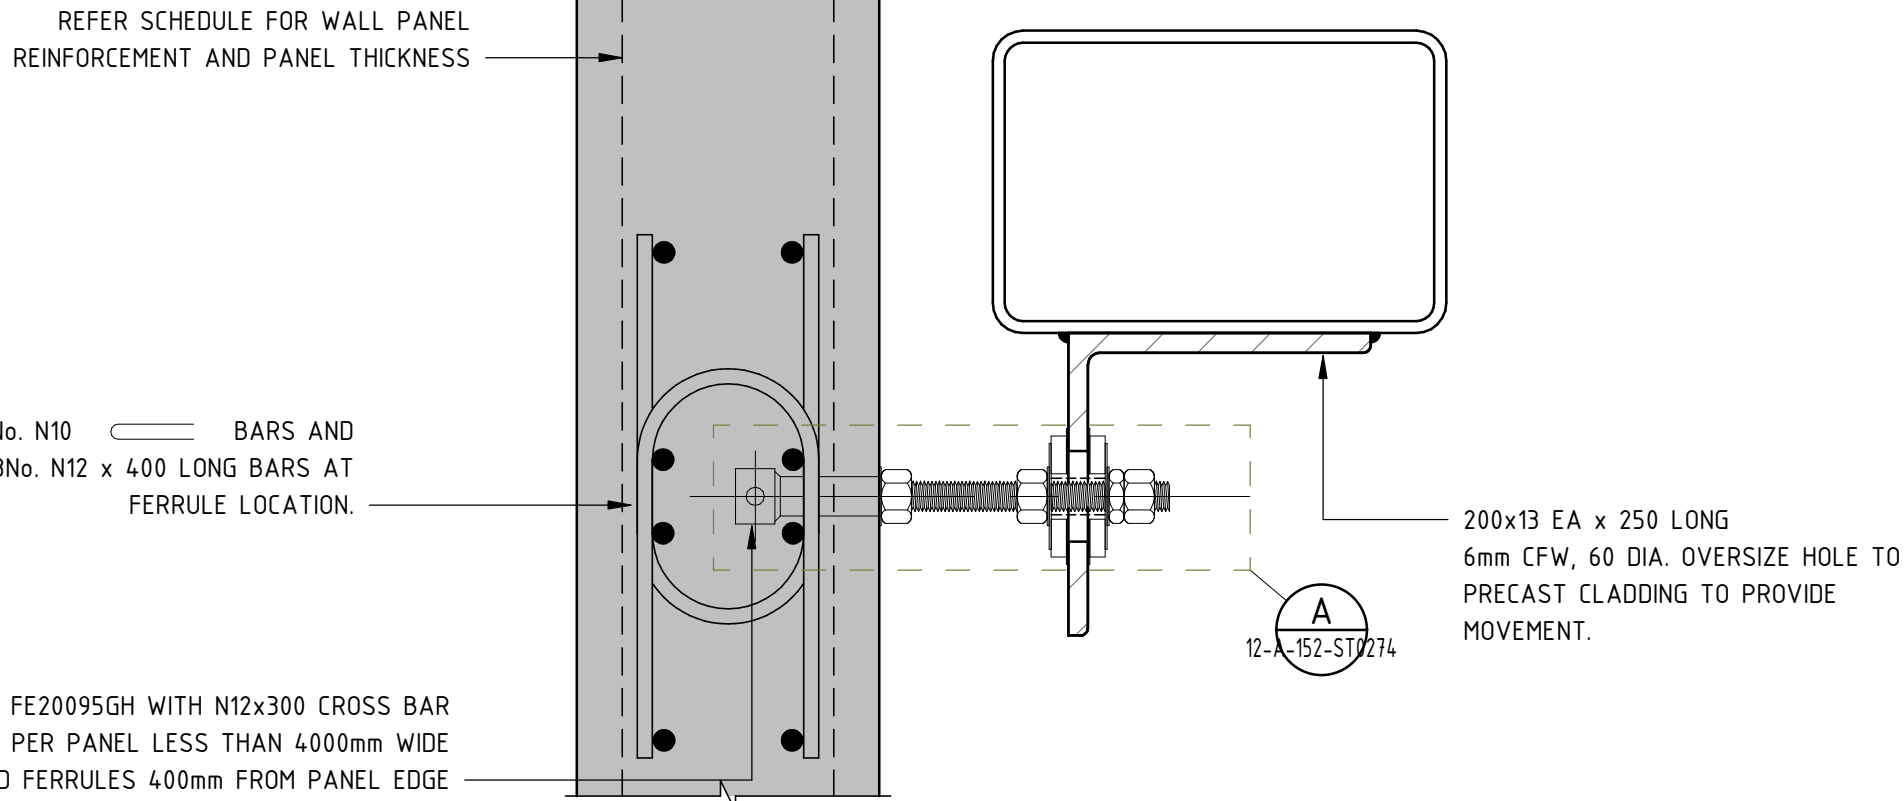

CONNECTION TYPE PC-CN02

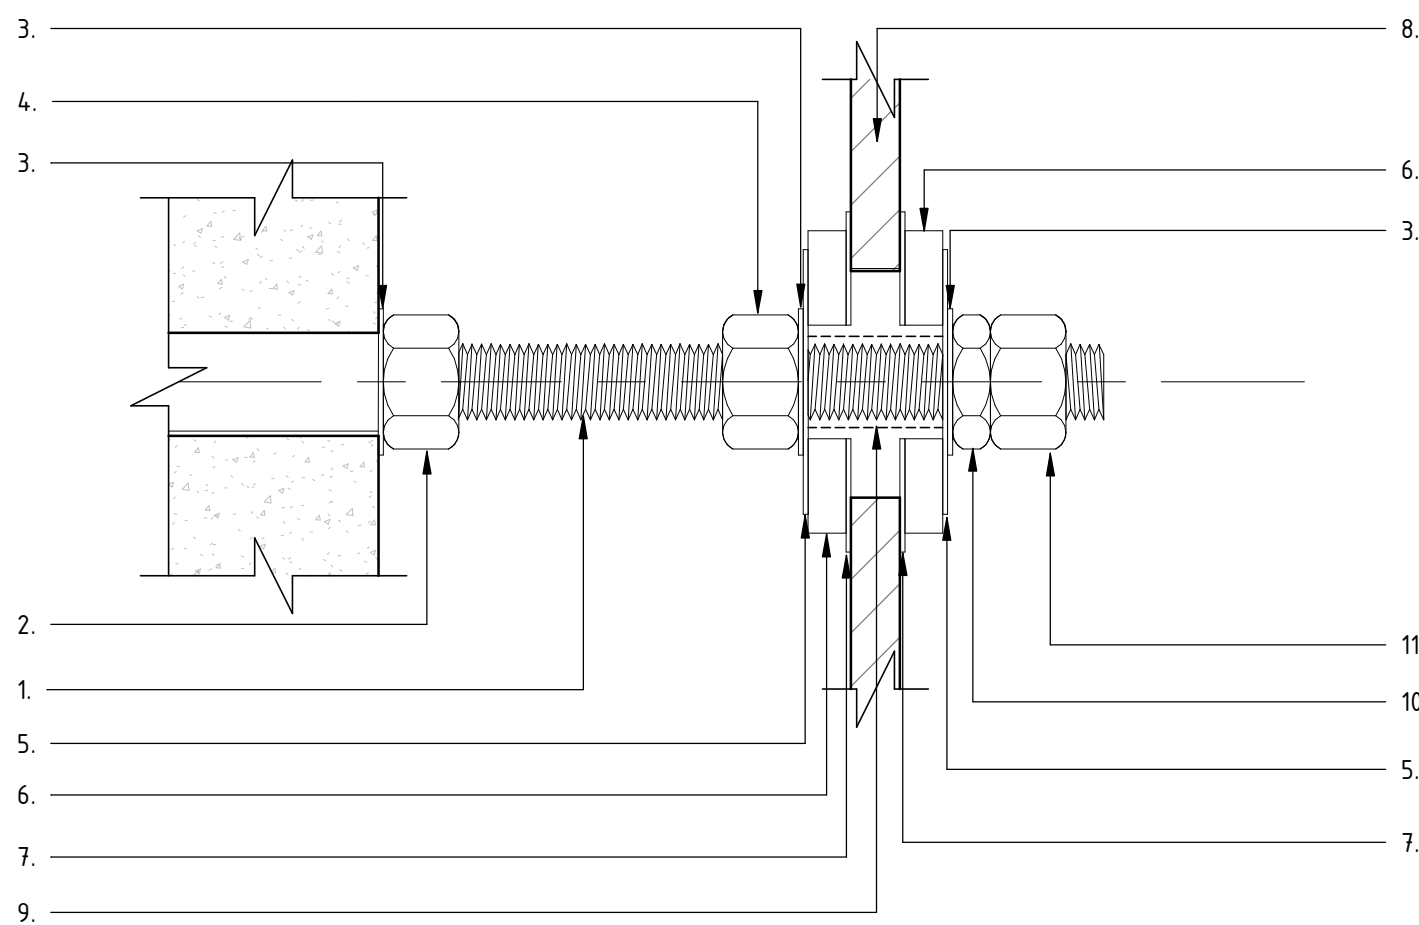


DETAIL A

1 : 2 12-A-152-ST0274


- ZONE PLAN**
- NOTES:**
- DO NO SCALE DRAWINGS. WRITTEN DIMENSIONS GOVERN.
 - ALL DIMENSIONS ARE IN MILLIMETRES UNLESS NOTED OTHERWISE
 - ALL DIMENSIONS SHALL BE VERIFIED ON SITE BEFORE PROCEEDING WITH THE WORK. RELEVANT PARTY SHALL BE NOTIFIED IN WRITING OF ANY DISCREPANCIES.
 - THIS DRAWING MUST BE READ IN CONJUNCTION WITH ALL RELEVANT CONTRACTS, SPECIFICATIONS, REPORTS AND DRAWINGS.

- NOTES:**
- DOWEL TUBE SPACING ON PRECAST SHOP DRAWINGS SHALL INCORPORATE THE SURVEYED AS BUILT SETOUT OF DOWELS
 - IT IS THE CONTRACTORS RESPONSIBILITY TO CO-ORDINATE ALL PENETRATIONS FOR SERVICES ETC. ALL PENETRATIONS SHALL BE SHOWN ON SHOP DRAWINGS FOR APPROVAL PRIOR TO FABRICATION OF ANY PANEL
 - REFER TO THE ARCHITECTS DRAWINGS FOR ALL JOINING DETAILS
 - REFER TO 12-A-152- ST0004 FOR PRECAST STANDARD NOTES

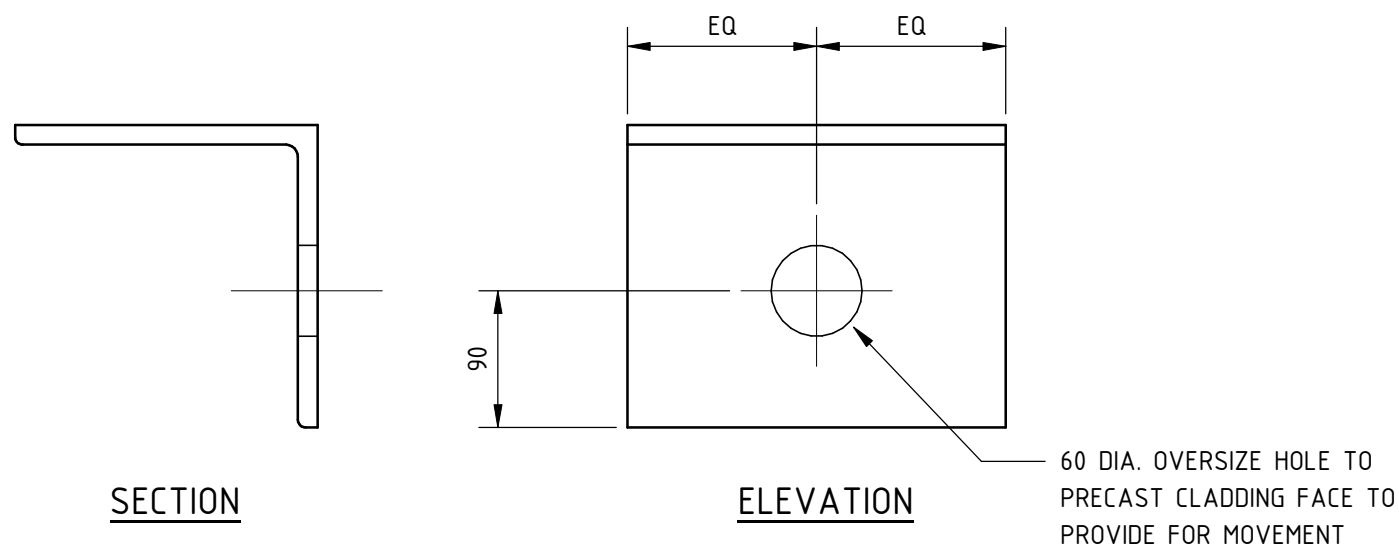

DETAIL B: TYPICAL ANGLE BRACKET

- M20 STAINLESS STEEL THREADED ROD GRADE 316
- M20 NUT INSTALLED IN ACCORDANCE WITH RAMSET TECHNICAL DATA SHEET
- M20 STAINLESS STEEL WASHER
- M20 STAINLESS STEEL NUT (TORQUE TO 80Nm)
- 50 DIA. x1 ISOLATION WASHER WITH 22 DIA. HOLE
- 80x80x10 GALVANISED PLATE WASHERS
- 90x90x1.0 PTFE SLIP WASHER
- GALVANISED ANGLE BRACKET
- PVC INSULATION TAPE ON BOLT SHANK
- M20 STAINLESS STEEL LOCK NUT (TORQUE TO 80Nm)
- M20/TB STAINLESS STEEL NUT

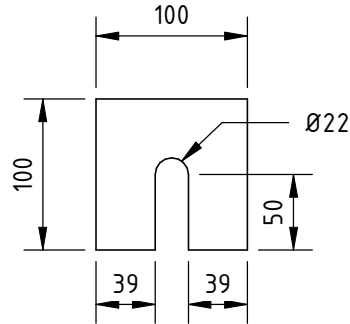

NOTE: PACKER PLATES TO BE PROVIDED IN THICKNESS OF 3mm & 10mm ALL PACKERS TO BE HOT DIP GALVANISED

PACKER PLATE DETAIL

- USE OF THESE DRAWINGS**
- THIS DRAWING SHALL BE READ IN CONJUNCTION WITH THE DISCIPLINE CONTRACT SPECIFICATION AND OTHER PROJECT DOCUMENTS.
 - DRAWINGS AND DESIGNS UNDERTAKEN BY A SHOP DETAILER SHALL BE PRESENTED TO THE PTA FOR REVIEW AND CONCURRENCE THAT THE DESIGN INTENT HAS BEEN ACHIEVED.
 - THE CONTRACTORS SHALL BE FULLY AWARE OF THE OTHER INTERFACING PACKAGES AND SHALL HAVE DEEMED TO HAVE INCLUDED INTER-TRADE INTERFACES. THE INTERFACES IDENTIFIED IN THE DOCUMENTATION ARE TO INDICATE AN INTENT AND ARE NOT INTENDED TO BE EXHAUSTIVE. MAKE ALLOWANCES AS REQUIRED.

ISSUED FOR CONSTRUCTION

REV	DATE	AMENDMENT	DSN	DRN	CHKD	APP
0	01.10.19	ISSUED FOR CONSTRUCTION	J.S.	A.C.D.	M.P.	G.B.
1	01.10.19	AMENDMENT				
2	01.10.19	AMENDMENT				
aurecon
www.aurecongroup.com



505695-0000-DRG-ST-1012


REFERENCES

SCALE :
As indicated (@ A1)
DATUM :
HORIZONTAL: PCG94
VERTICAL: AHD71
PTA ACCEPTANCE STAMP


DESIGNED J.SPANO
DRAWN A.DAWSON
CHECKED M.PEARCE
APPROVED FOR ISSUE
G.BENTLEY
DATE

Government of Western Australia
Public Transport Authority
DETAILED DESIGN FOR THE BELLEVUE DEPOT
HV TESTING FACILITY
STRUCTURAL
STANDARD PC CONCRETE DETAILS
PTA Drawing No: 12-A-152-ST0274
REV : 0

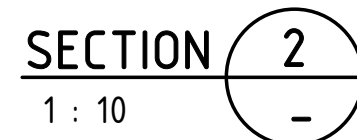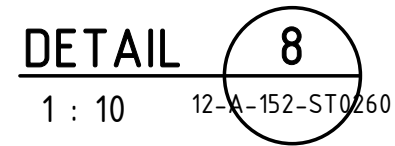


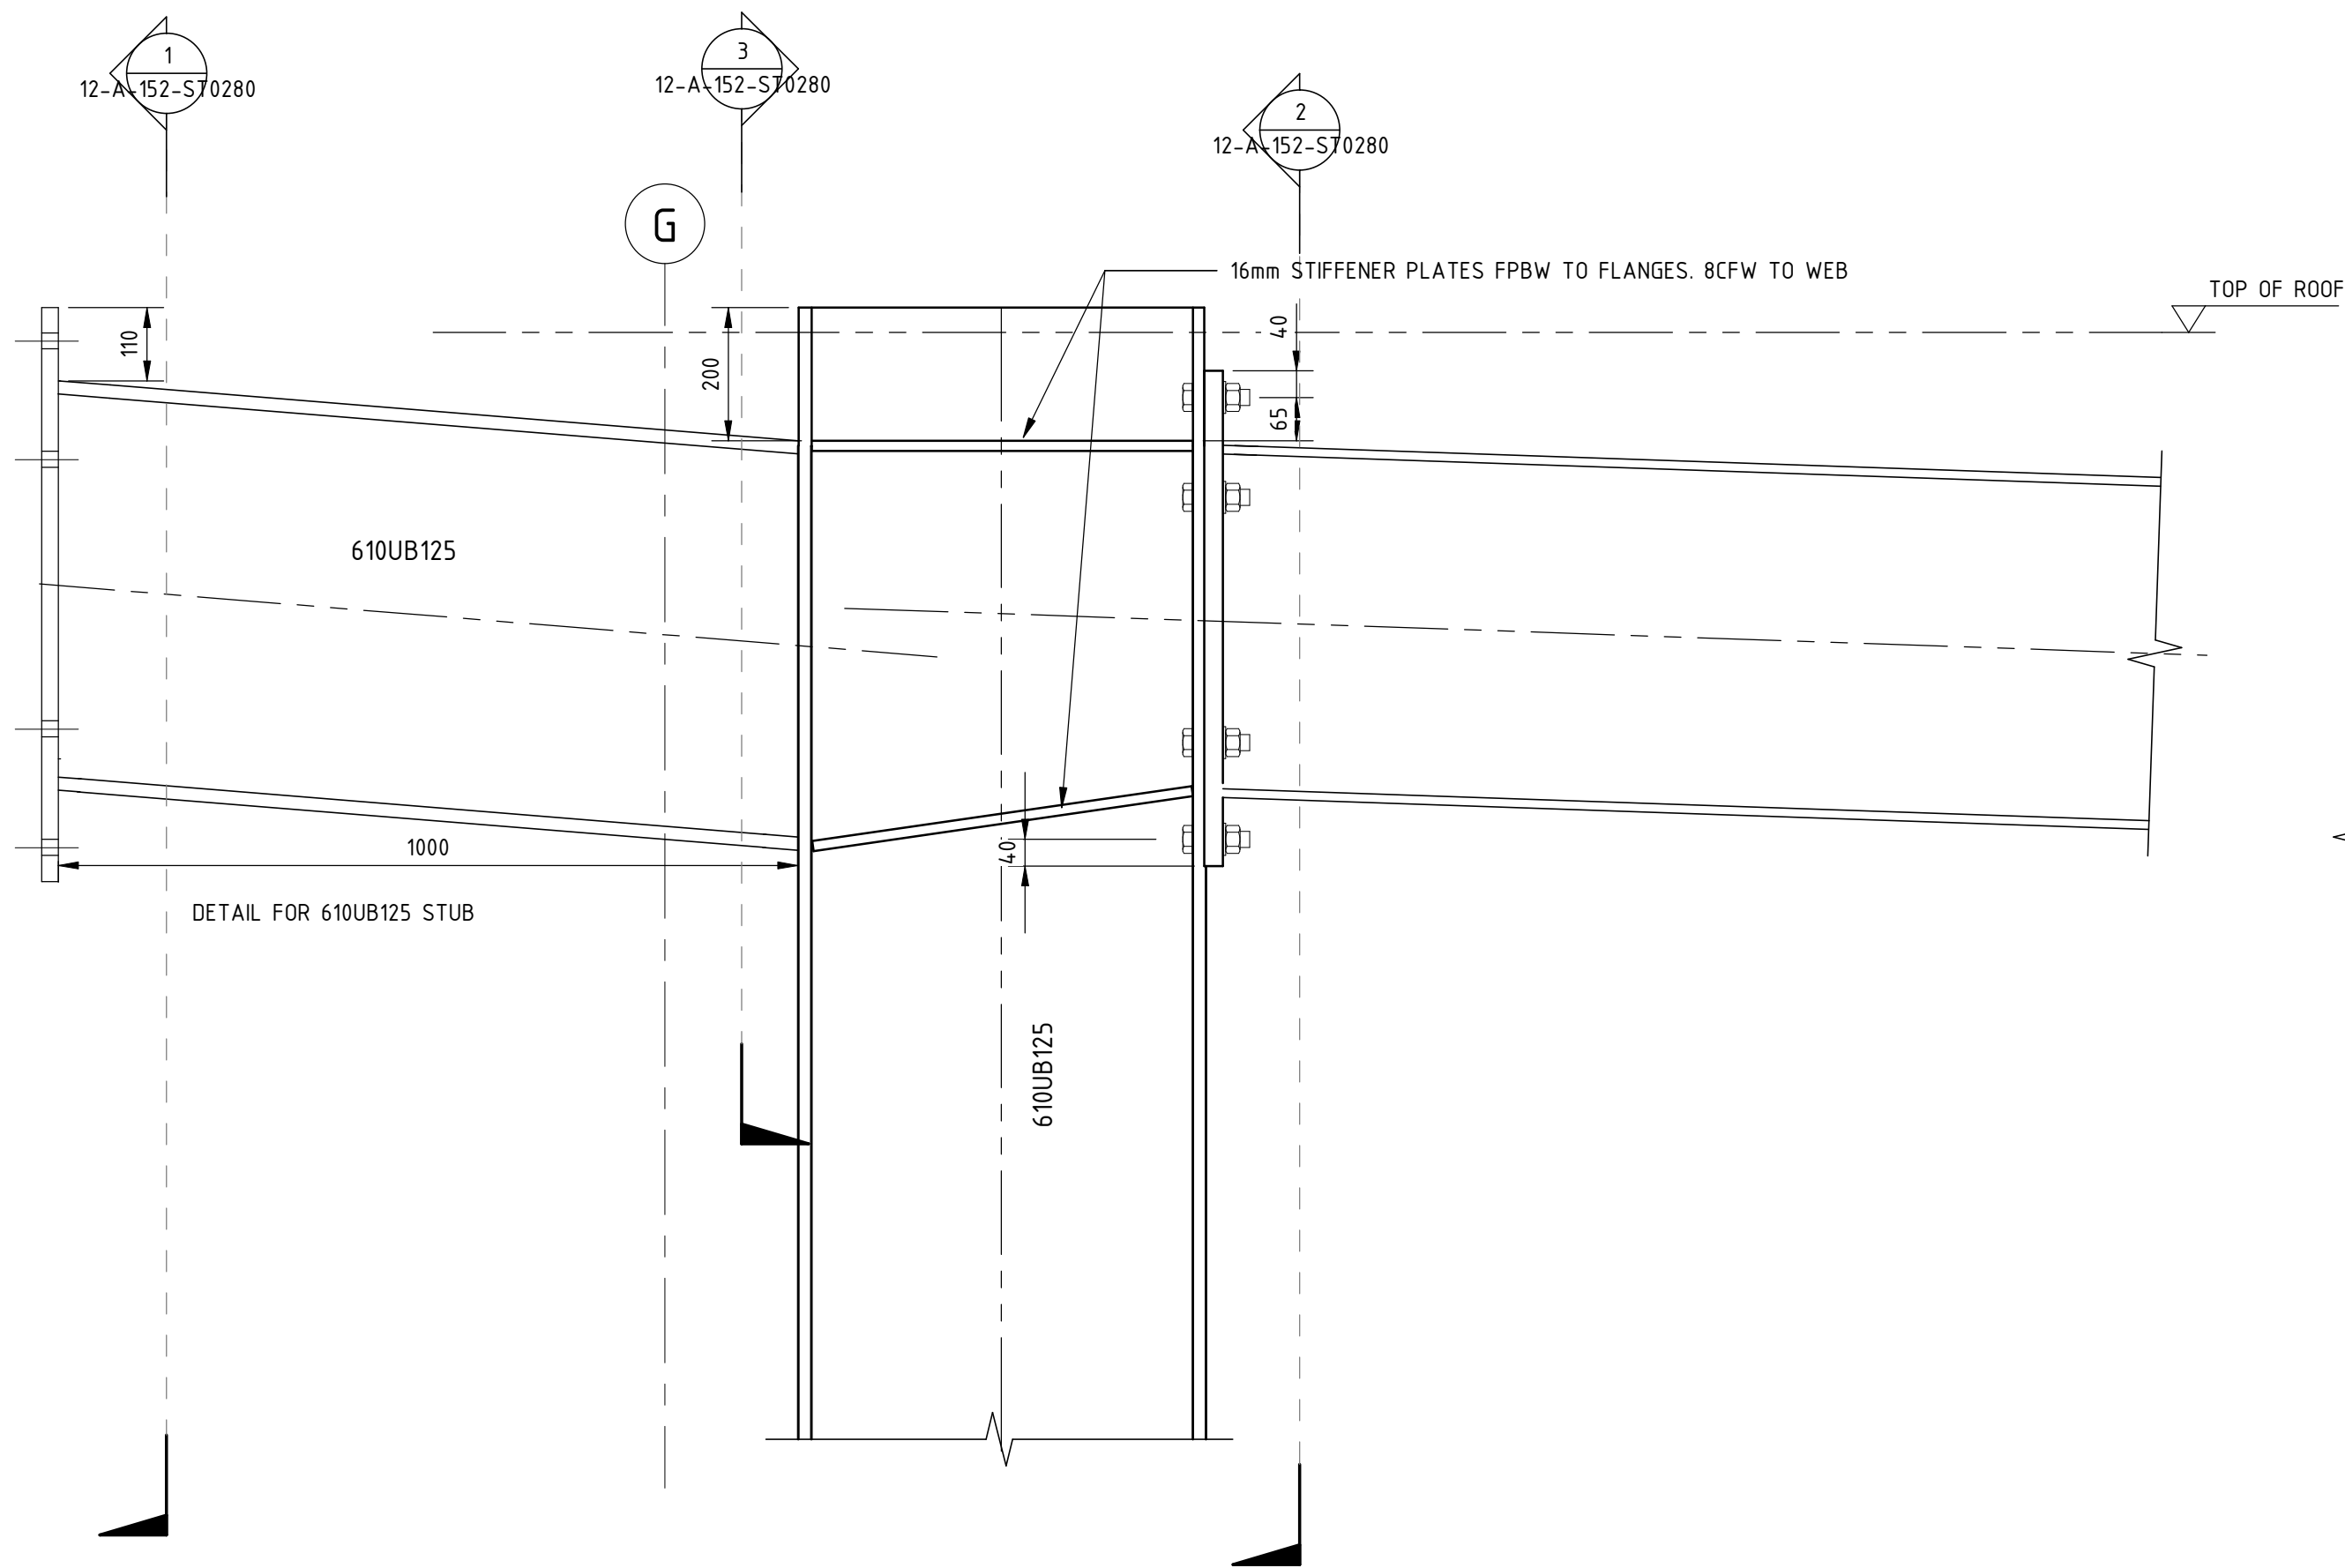


DETAIL 5
1 : 10 12-A-152-ST0258

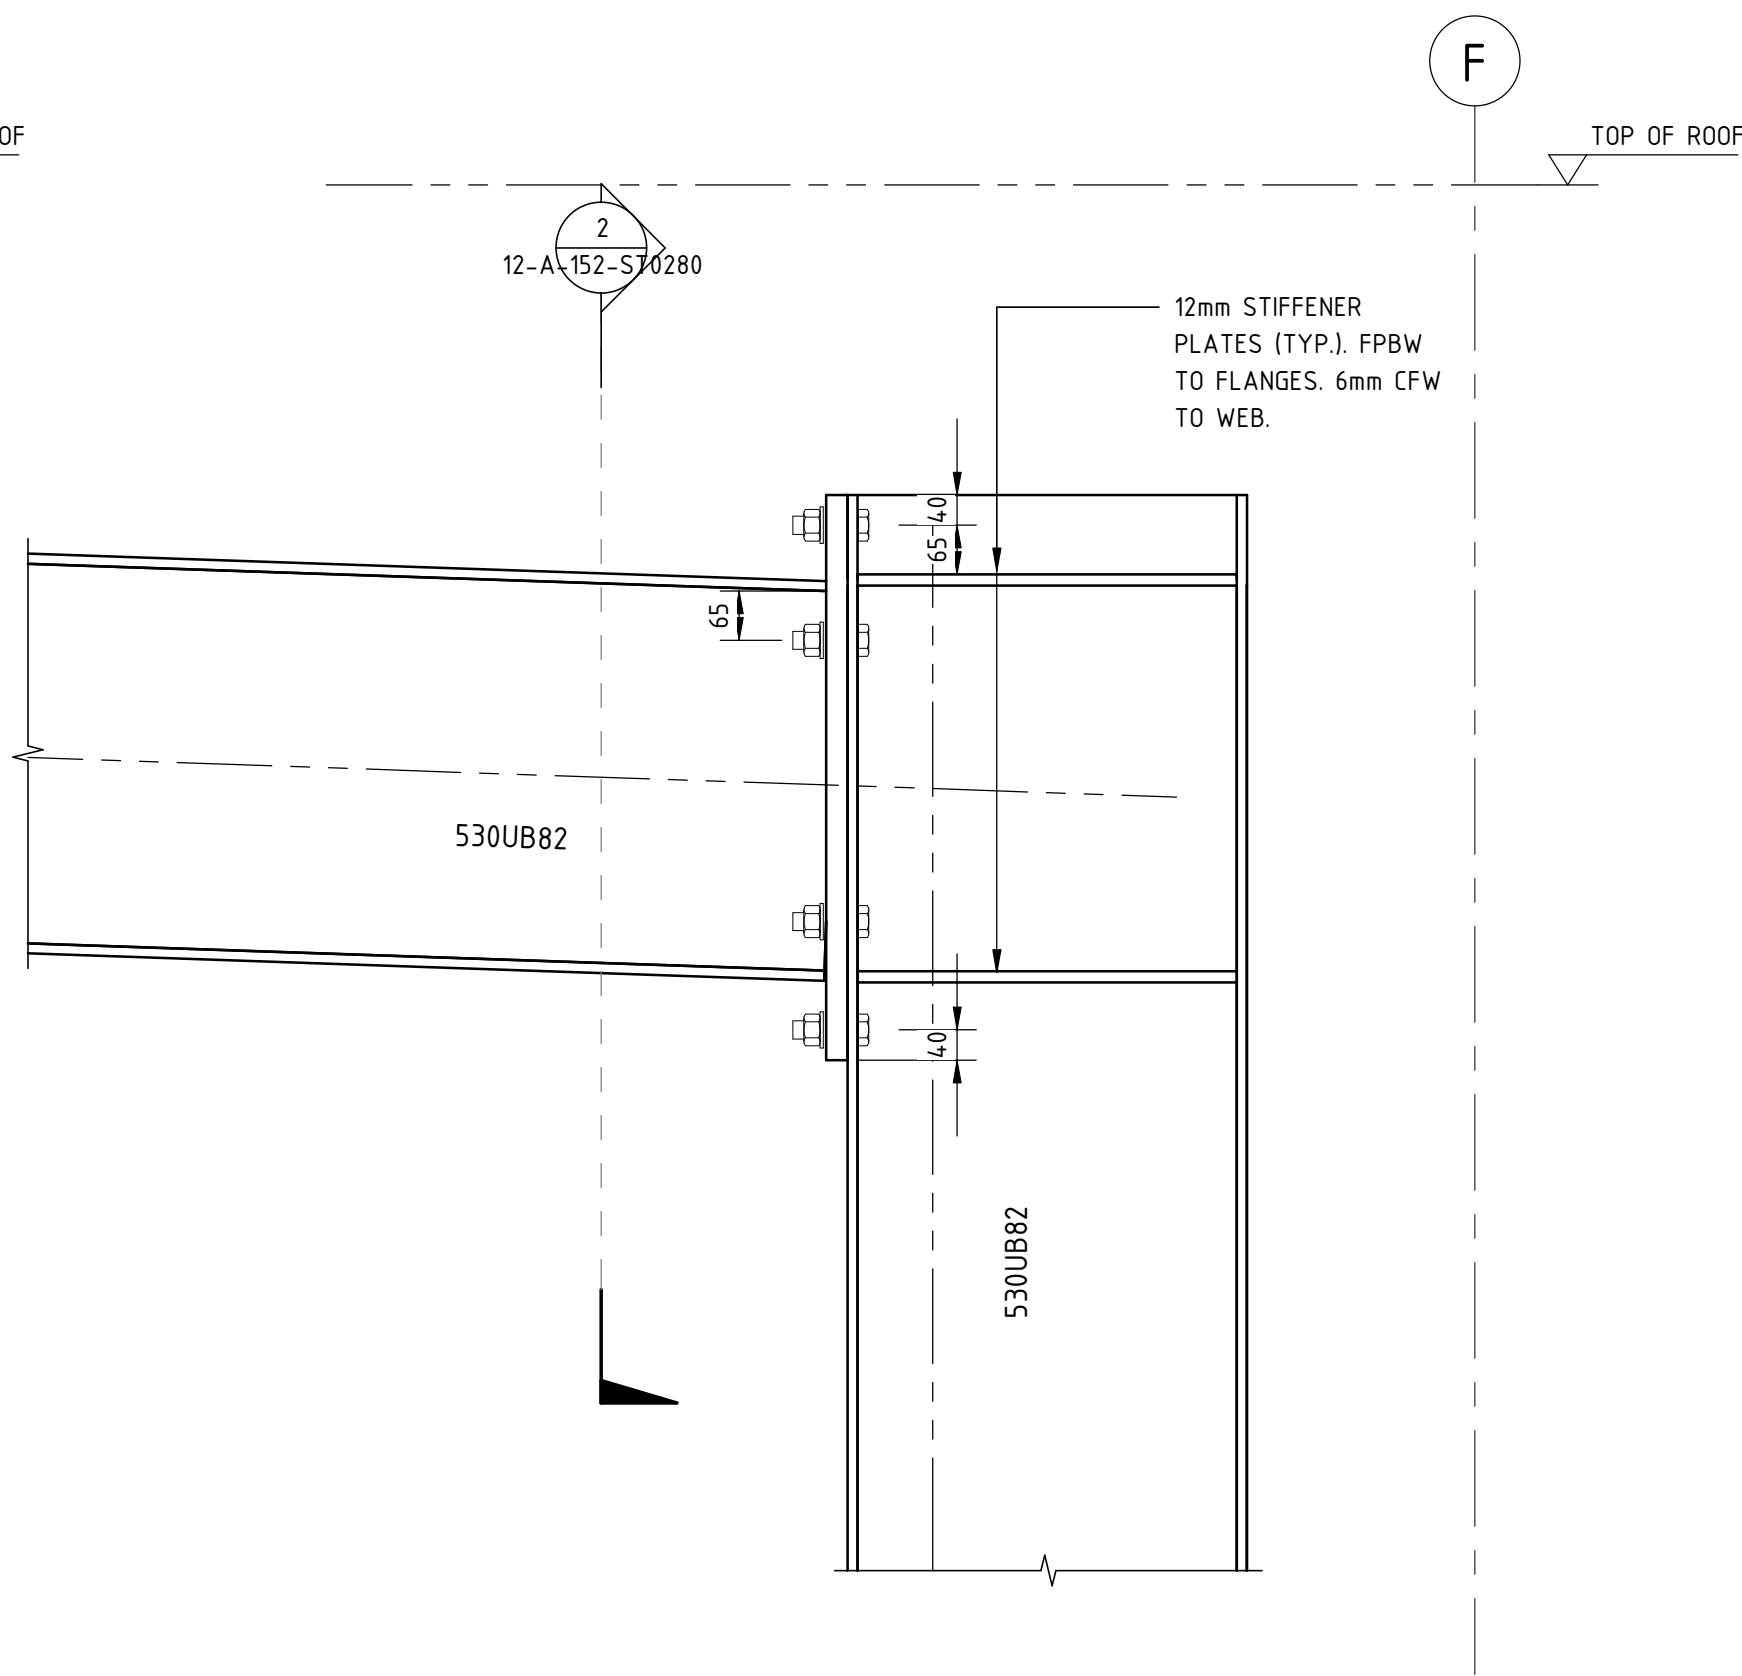


DETAIL 6
1 : 10 12-A-152-ST0258

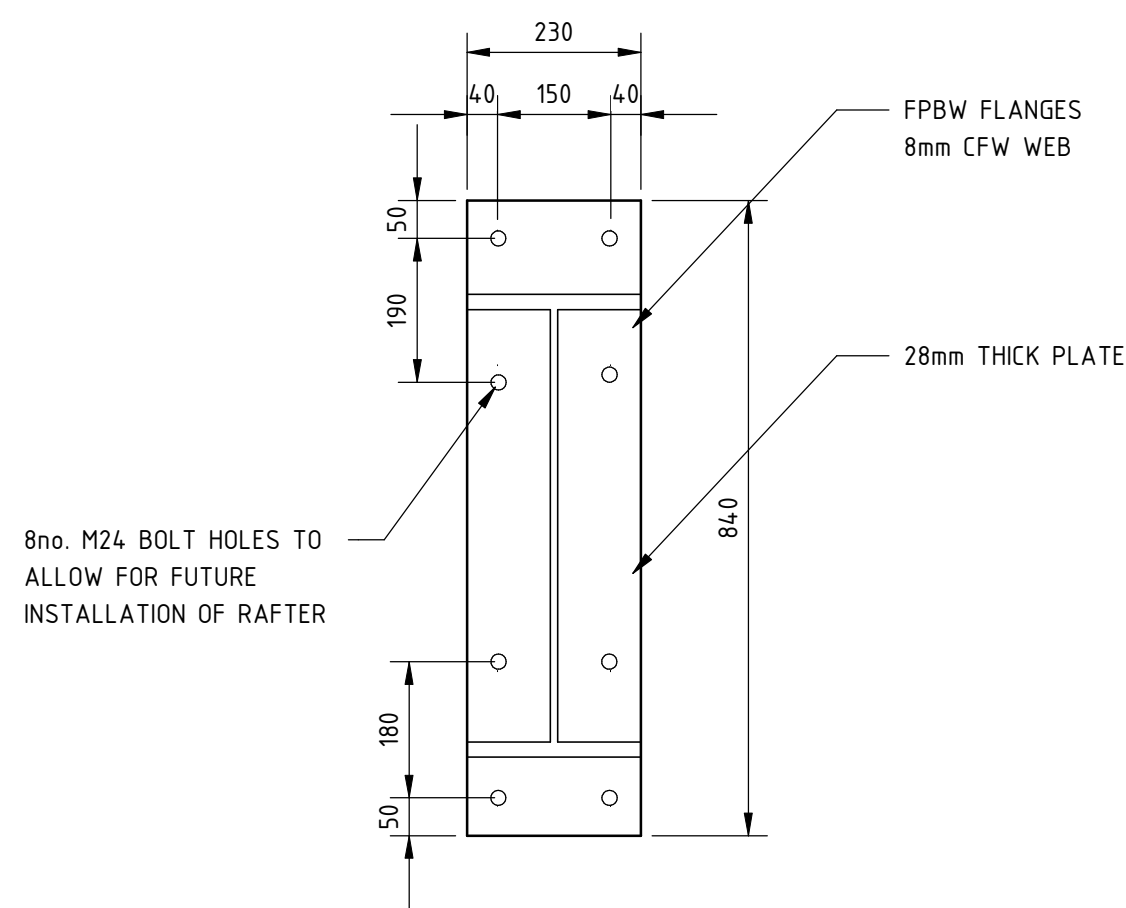

SECTION 1
1 : 10

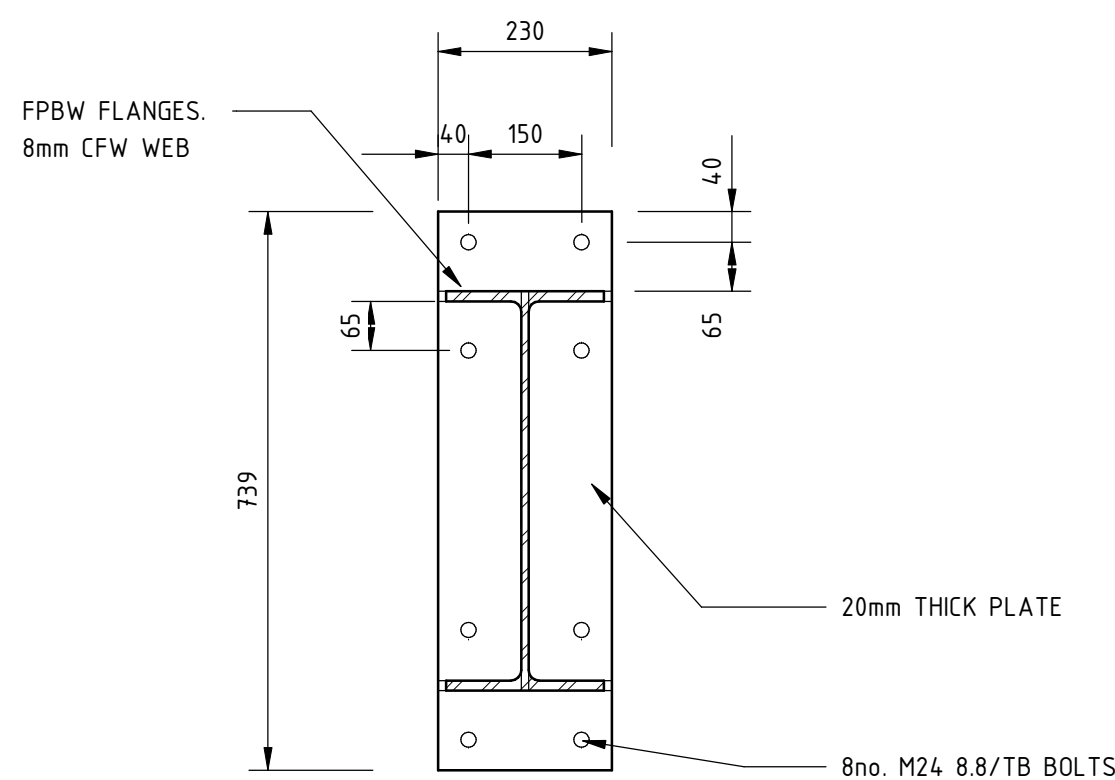

SECTION 2
1 : 10

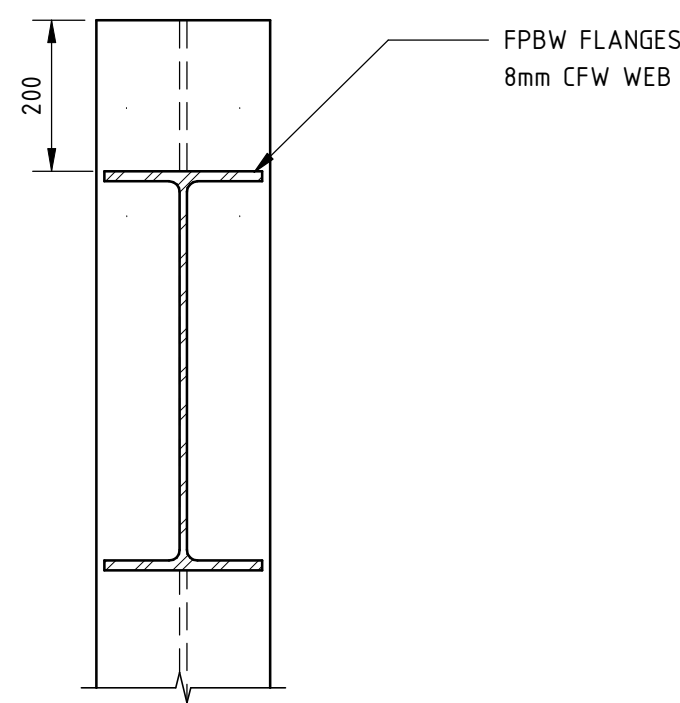

SECTION 3
1 : 10

ZONE PLAN

- NOTES:
- DO NO SCALE DRAWINGS. WRITTEN DIMENSIONS GOVERN.
 - ALL DIMENSIONS ARE IN MILLIMETRES UNLESS NOTED OTHERWISE
 - ALL DIMENSIONS SHALL BE VERIFIED ON SITE BEFORE PROCEEDING WITH THE WORK. RELEVANT PARTY SHALL BE NOTIFIED IN WRITING OF ANY DISCREPANCIES.
 - THIS DRAWING MUST BE READ IN CONJUNCTION WITH ALL RELEVANT CONTRACTS, SPECIFICATIONS, REPORTS AND DRAWINGS.

- NOTES:
- REFER TO 12-A-152-ST004 FOR GENERAL STEEL NOTES
 - REFER TO ARCHITECTURAL DRAWINGS FOR TYP. SYSTEM WIDE PROPRIETARY HANDRAIL DETAILS

- USE OF THESE DRAWINGS
- THIS DRAWING SHALL BE READ IN CONJUNCTION WITH THE DISCIPLINE CONTRACT SPECIFICATION AND OTHER PROJECT DOCUMENTS.
 - DRAWINGS AND DESIGNS UNDERTAKEN BY A SHOP DETAILER SHALL BE PRESENTED TO THE PTA FOR REVIEW AND CONCURRENCE THAT THE DESIGN INTENT HAS BEEN ACHIEVED.
 - THE CONTRACTORS SHALL BE FULLY AWARE OF THE OTHER INTERFACING PACKAGES AND SHALL HAVE DEEMED TO HAVE INCLUDED INTER-TRADE INTERFACES. THE INTERFACES IDENTIFIED IN THE DOCUMENTATION ARE TO INDICATE AN INTENT AND ARE NOT INTENDED TO BE EXHAUSTIVE. MAKE ALLOWANCES AS REQUIRED.





ISSUED FOR CONSTRUCTION

REV	DATE	AMENDMENT	DSN	DRN	CHKD	APP
0	01.10.19	ISSUED FOR CONSTRUCTION	J.S.	A.C.D.	M.P.	G.B.
1	01.10.19	AMENDMENT	J.S.	A.C.D.	M.P.	G.B.
2	01.10.19	AMENDMENT	J.S.	A.C.D.	M.P.	G.B.
aurecon www.aurecongroup.com
505695-0000-DRG-ST-1820

REFERENCES	SCALE :	DESIGNED
	As indicated (@ A1)	J.SPANO
	DATUM :	DRAWN
	HORIZONTAL: PCG94	A.DAWSON
	VERTICAL: AHD71	CHECKED
		M.PEARCE
		APPROVED FOR ISSUE
		G.BENTLEY
		DATE

Government of Western Australia Public Transport Authority	DETAILED DESIGN FOR THE BELLEVUE DEPOT
HV TESTING FACILITY	
STRUCTURAL	
SECTIONS AND DETAILS - SHEET 6 OF 7	
PTA Drawing No: 12-A-152-ST0280	REV : 0

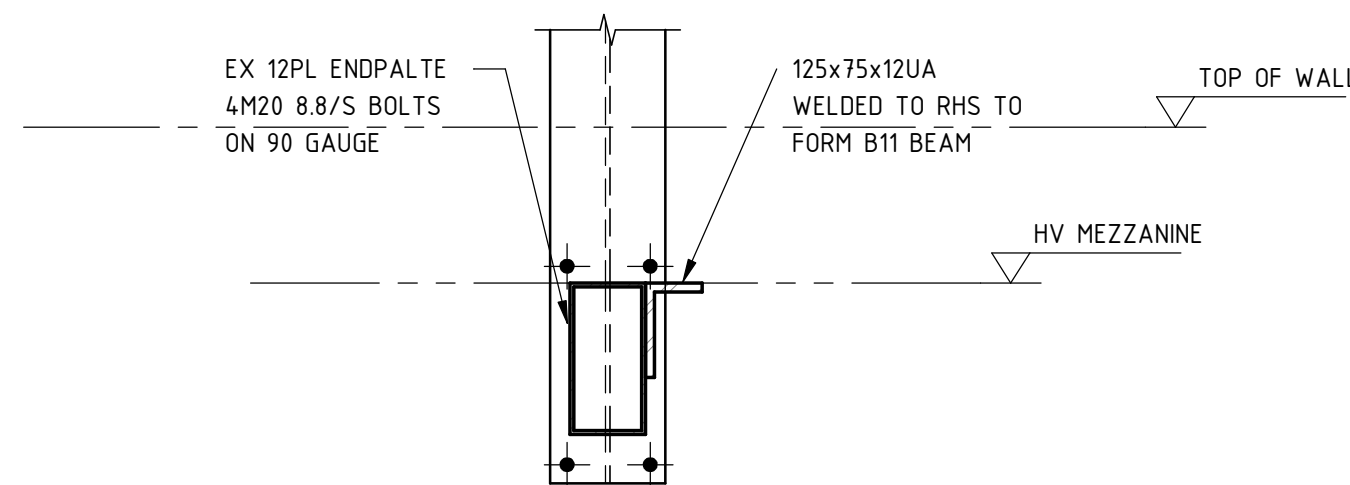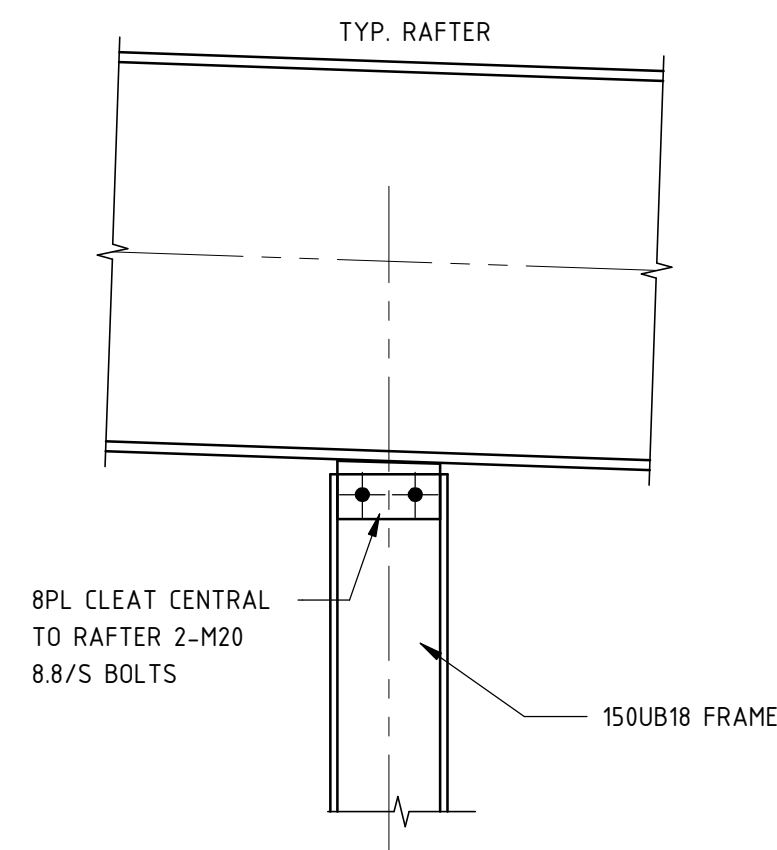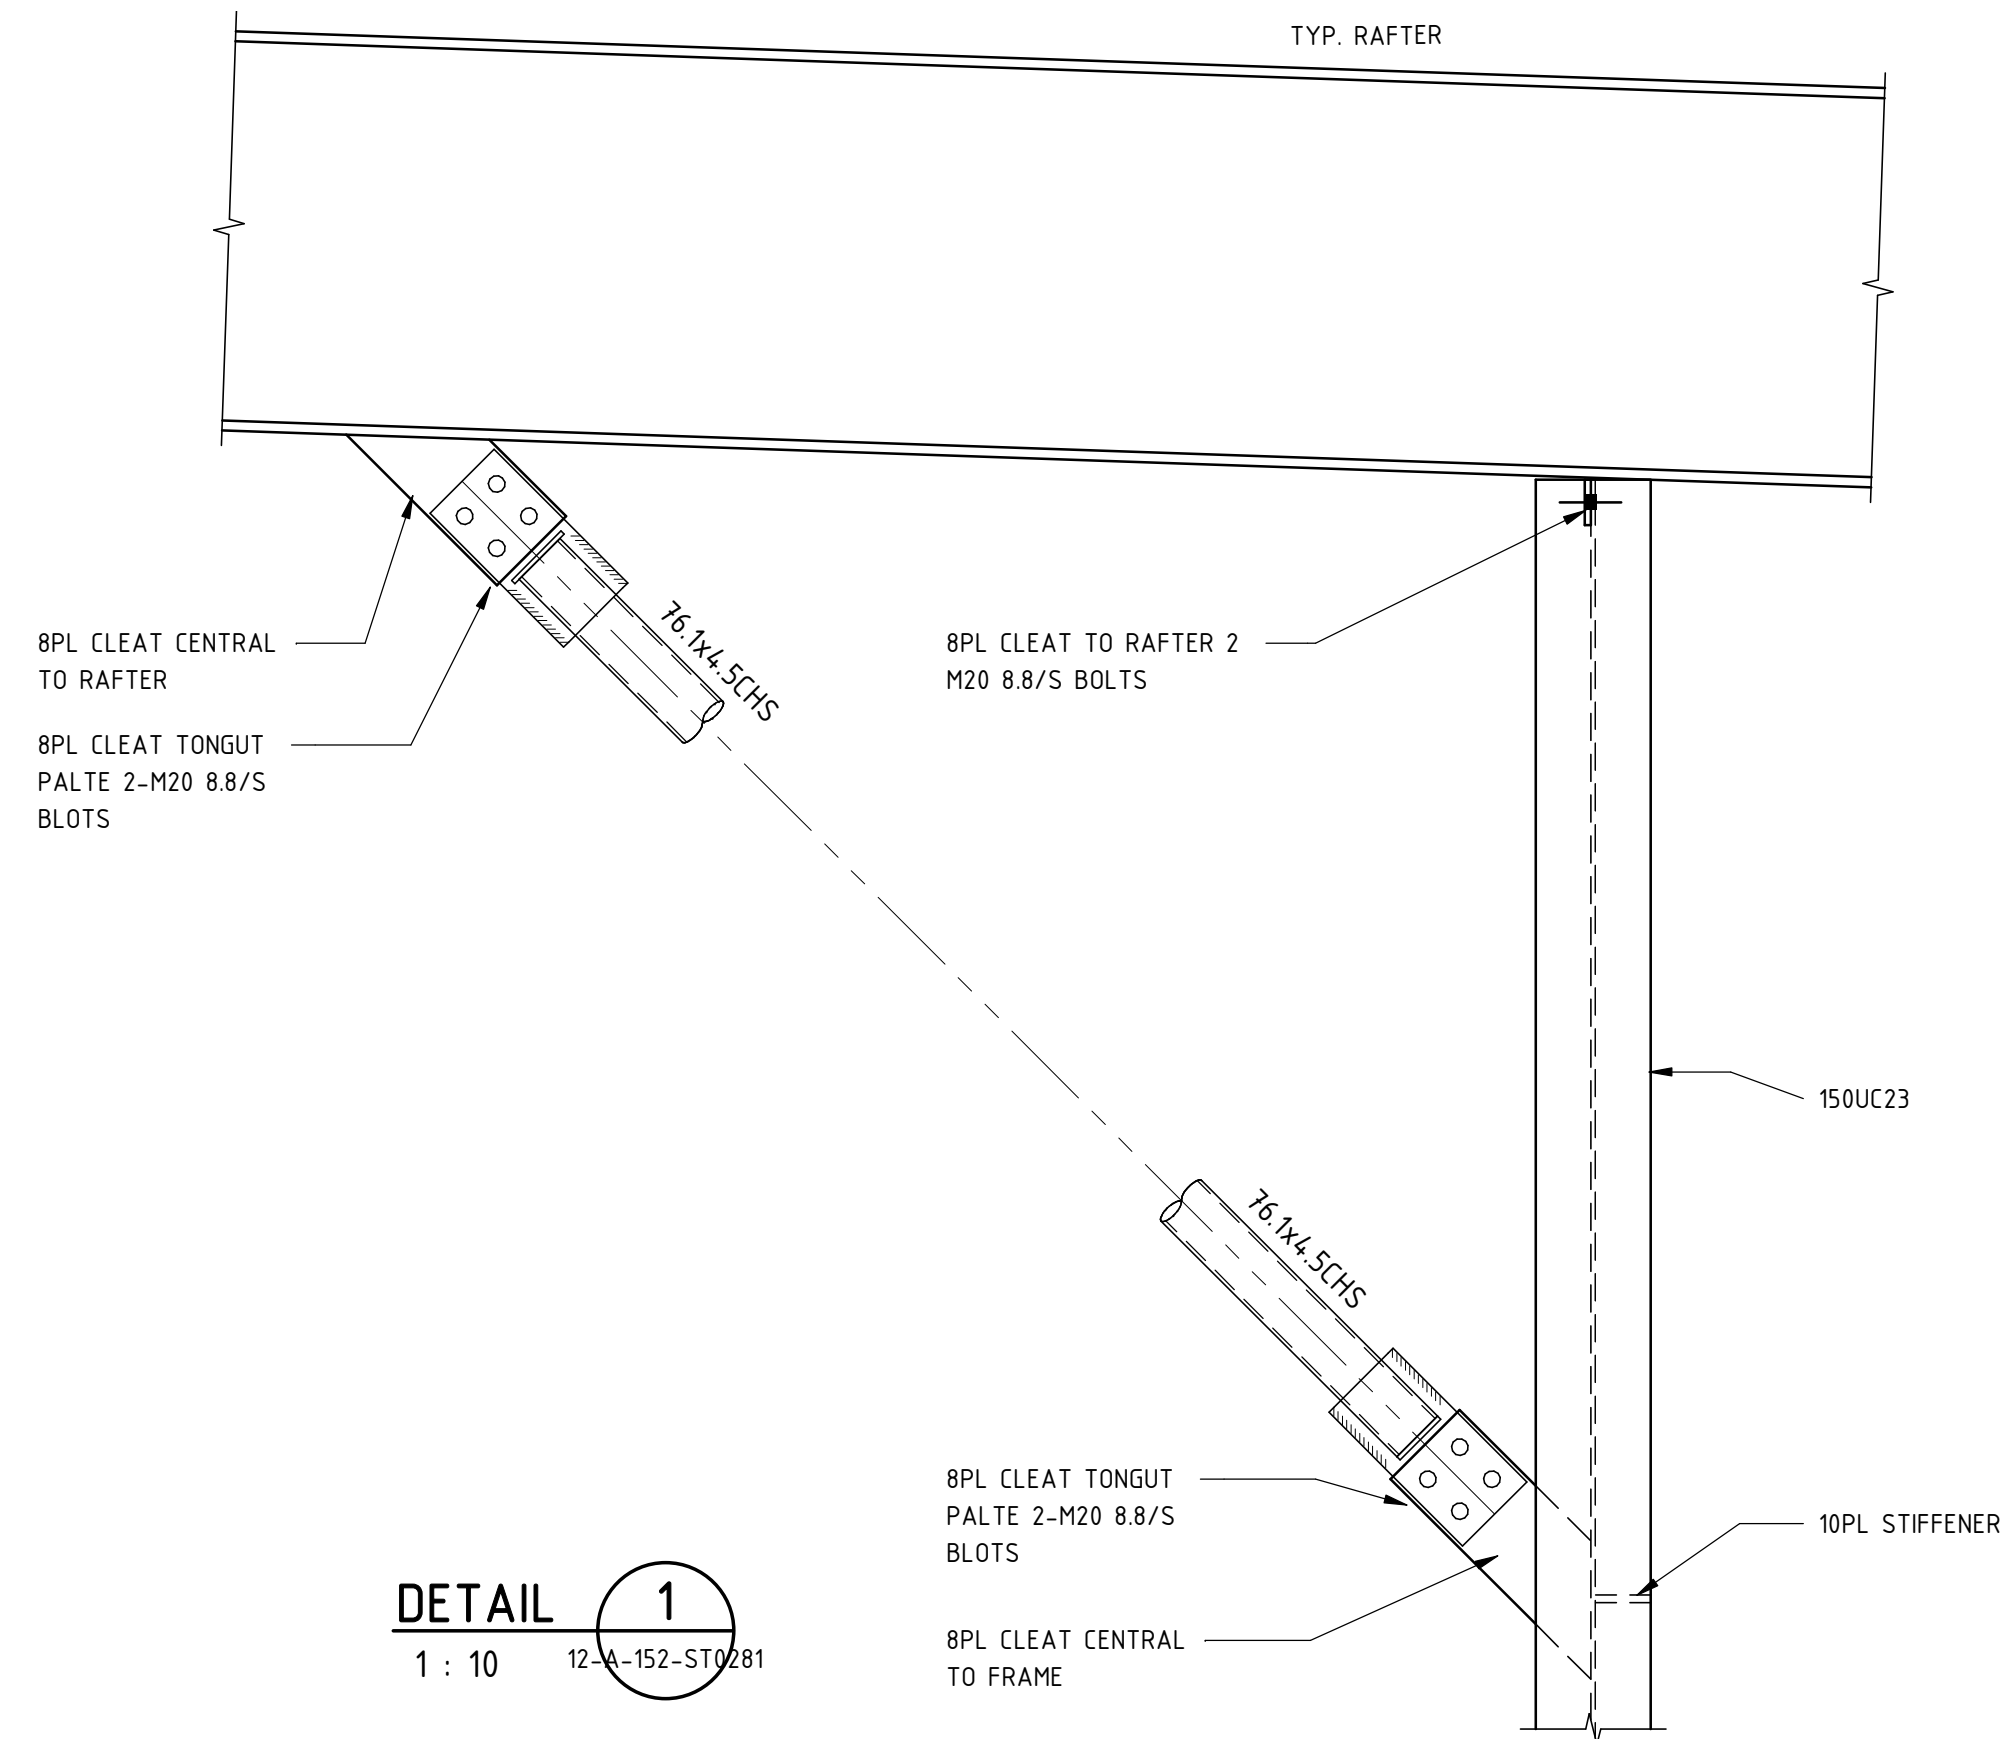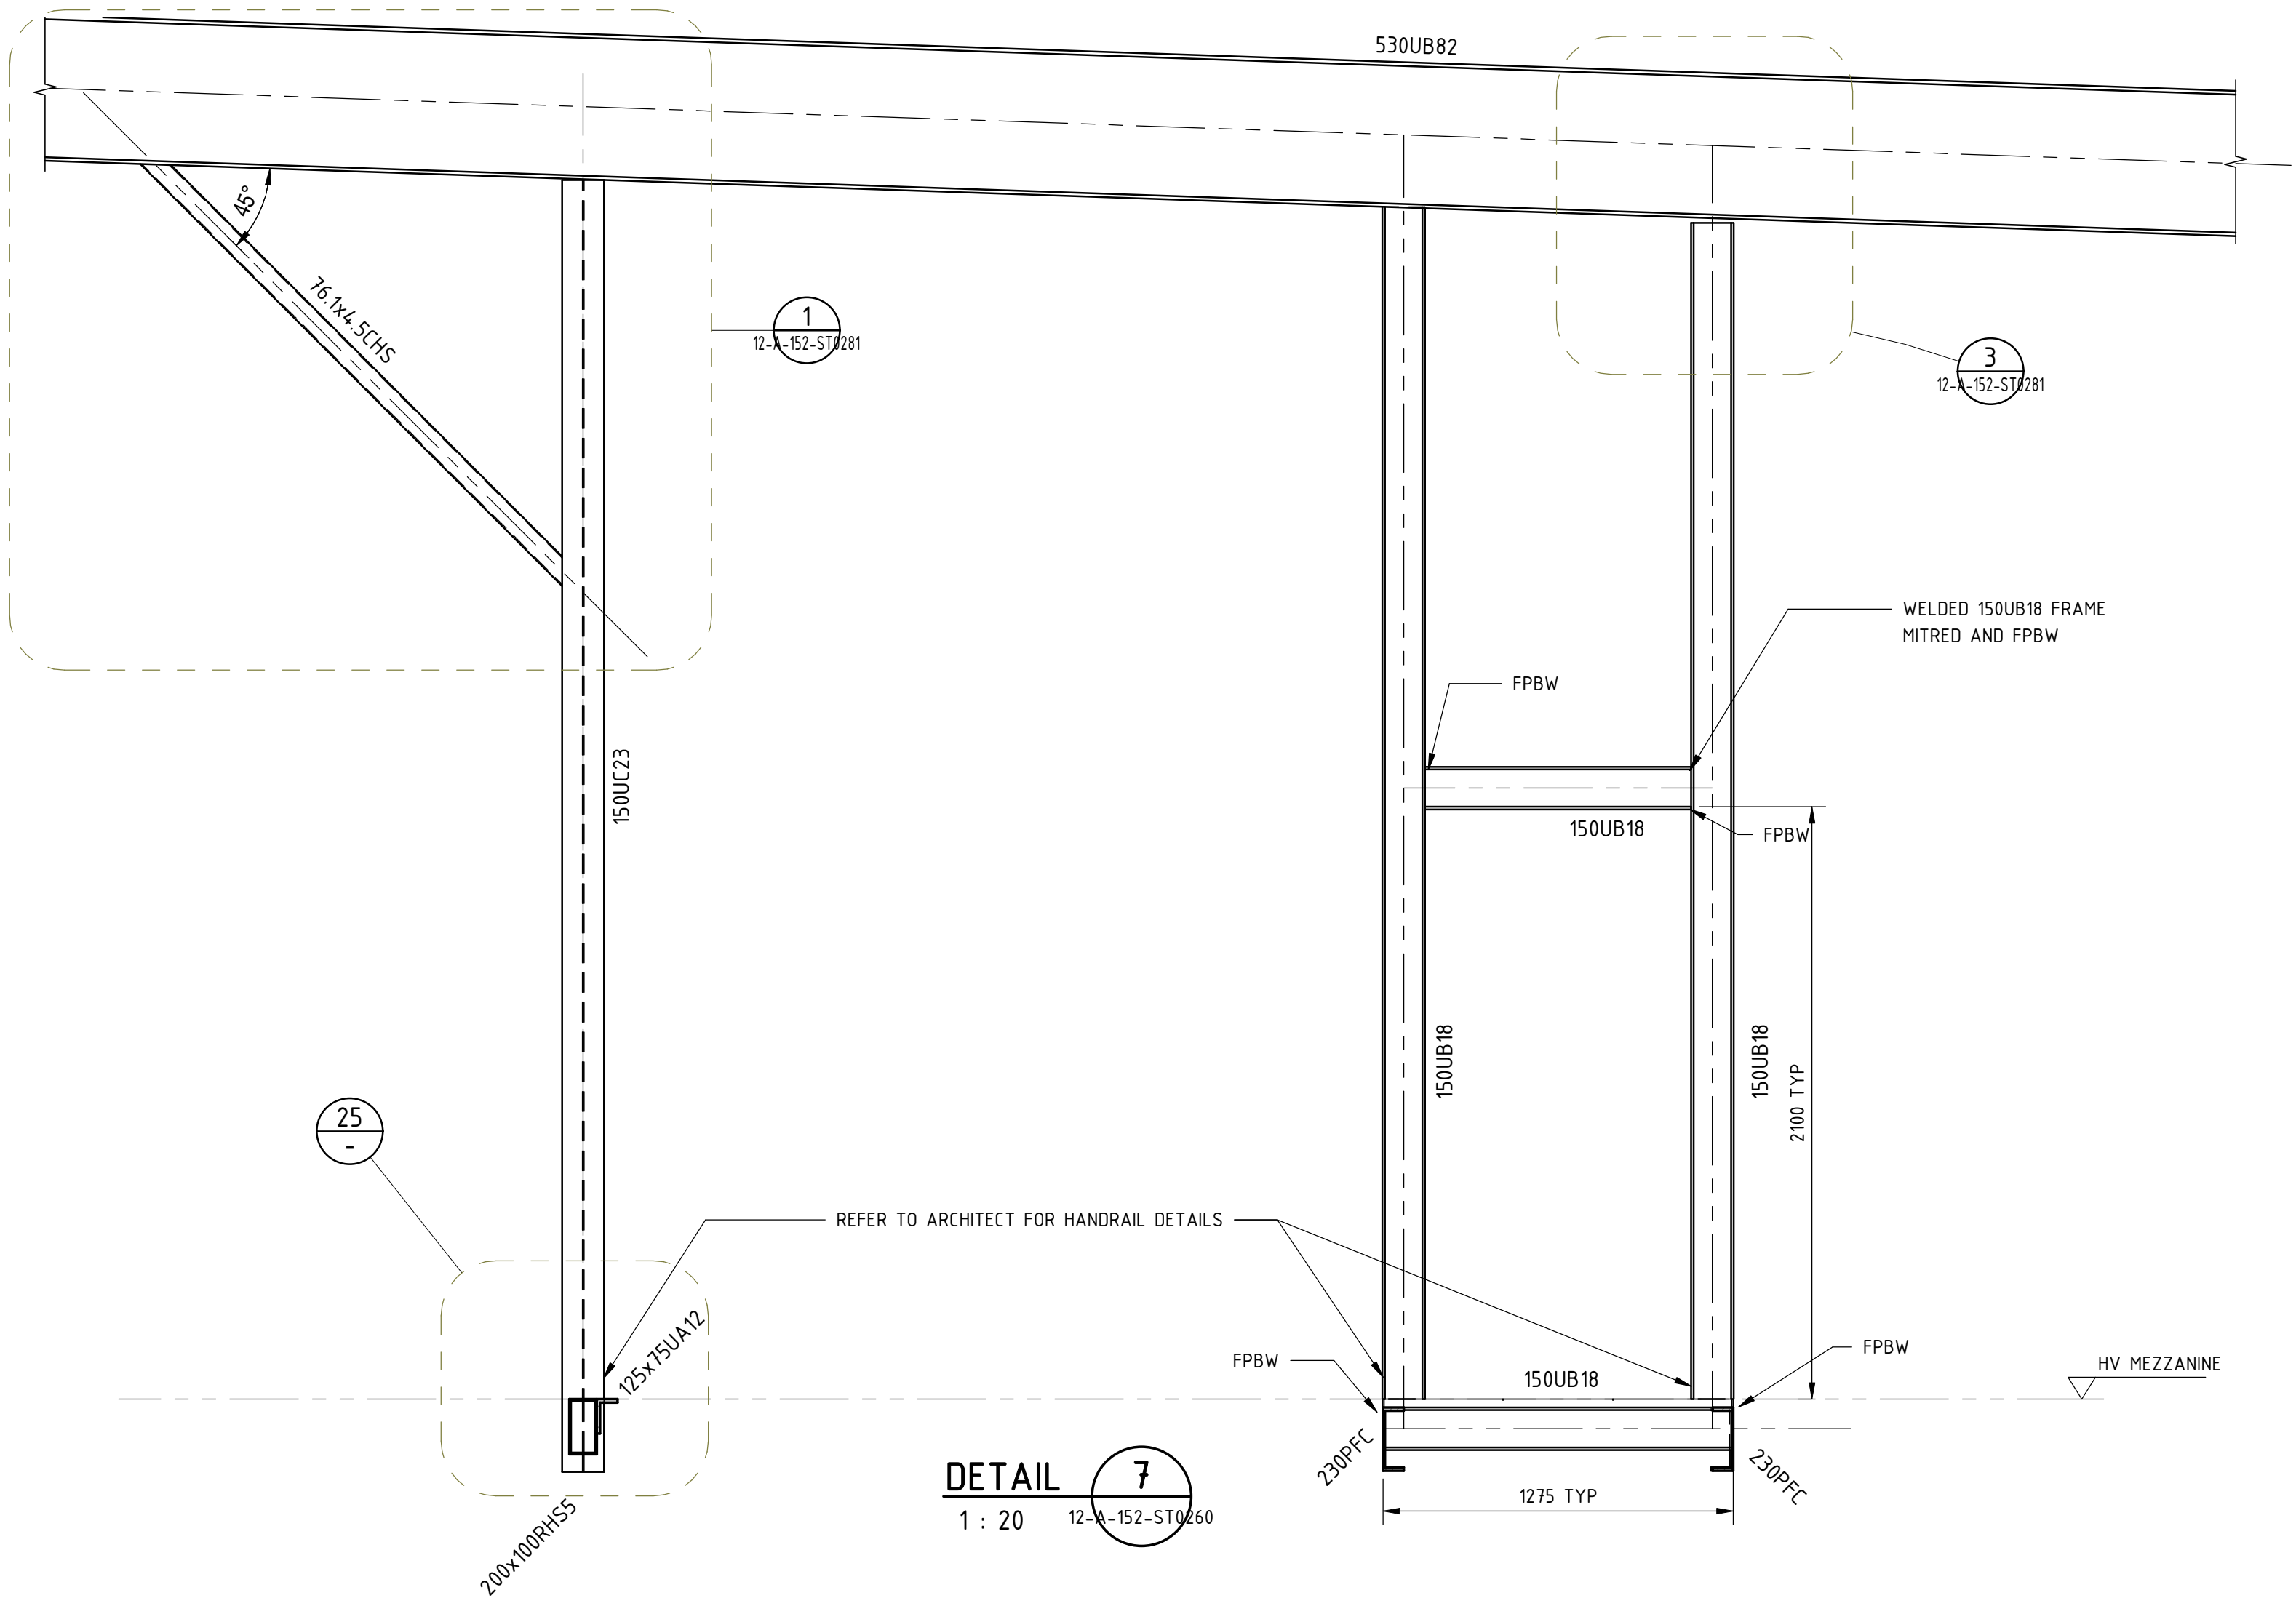

ZONE PLAN

- NOTES:**
- DO NO SCALE DRAWINGS. WRITTEN DIMENSIONS GOVERN.
 - ALL DIMENSIONS ARE IN MILLIMETRES UNLESS NOTED OTHERWISE
 - ALL DIMENSIONS SHALL BE VERIFIED ON SITE BEFORE PROCEEDING WITH THE WORK. RELEVANT PARTY SHALL BE NOTIFIED IN WRITING OF ANY DISCREPANCIES.
 - THIS DRAWING MUST BE READ IN CONJUNCTION WITH ALL RELEVANT CONTRACTS, SPECIFICATIONS, REPORTS AND DRAWINGS.

- NOTES:**
- REFER TO 12-A-152-ST004 FOR GENERAL STEEL NOTES
 - REFER TO ARCHITECTURAL DRAWINGS FOR TYP. SYSTEM WIDE PROPRIETARY HANDRAIL DETAILS

- USE OF THESE DRAWINGS**
- THIS DRAWING SHALL BE READ IN CONJUNCTION WITH THE DISCIPLINE CONTRACT SPECIFICATION AND OTHER PROJECT DOCUMENTS.
 - DRAWINGS AND DESIGNS UNDERTAKEN BY A SHOP DETAILER SHALL BE PRESENTED TO THE PTA FOR REVIEW AND CONCURRENCE THAT THE DESIGN INTENT HAS BEEN ACHIEVED.
 - THE CONTRACTORS SHALL BE FULLY AWARE OF THE OTHER INTERFACING PACKAGES AND SHALL HAVE DEEMED TO HAVE INCLUDED INTER-TRADE INTERFACES. THE INTERFACES IDENTIFIED IN THE DOCUMENTATION ARE TO INDICATE AN INTENT AND ARE NOT INTENDED TO BE EXHAUSTIVE. MAKE ALLOWANCES AS REQUIRED.

ISSUED FOR CONSTRUCTION

0	01.10.19	ISSUED FOR CONSTRUCTION	J.S.	A.C.D.	M.P.	G.B.
REV	DATE	AMENDMENT	DSN	DRN	CHKD	APP
ORIG SIZE	A1	SCALE 1:20 AT A1	This document must not be copied without PTA's written permission, and the contents thereof must not be imparted to a third party nor be used for any unauthorised purpose.			

aurecon
www.aurecongroup.com

505695-0000-DRG-ST-1821

REFERENCES

SCALE :
As indicated (@ A1)
DATUM :
HORIZONTAL: PCG94
VERTICAL: AHD71
PTA ACCEPTANCE STAMP

DESIGNED J.SPANO
DRAWN A.DAWSON
CHECKED M.PEARCE
APPROVED FOR ISSUE
G.BENTLEY
DATE

Government of Western Australia
Public Transport Authority
DETAILED DESIGN FOR THE BELLEVUE DEPOT
HV TESTING FACILITY
STRUCTURAL
SECTIONS AND DETAILS - SHEET 7 OF 7
PTA Drawing No: 12-A-152-ST0281
REV : 0



ZONE PLAN

1. DO NO SCALE DRAWINGS. WRITTEN DIMENSIONS GOVERN.
2. ALL DIMENSIONS ARE IN MILLIMETRES UNLESS NOTED OTHERWISE
3. ALL DIMENSIONS SHALL BE VERIFIED ON SITE BEFORE PROCEEDING WITH THE WORK. RELEVANT PARTY SHALL BE NOTIFIED IN WRITING OF ANY DISCREPANCIES.
4. THIS DRAWING MUST BE READ IN CONJUNCTION WITH ALL RELEVANT CONTRACTS, SPECIFICATIONS, REPORTS AND DRAWINGS.

USE OF THESE DRAWINGS

1. THIS DRAWING SHALL BE READ IN CONJUNCTION WITH THE DISCIPLINE CONTRACT SPECIFICATION AND OTHER PROJECT DOCUMENTS.
2. DRAWINGS AND DESIGNS UNDERTAKEN BY A SHOP DETAILER SHALL BE PRESENTED TO THE PTA FOR REVIEW AND CONCURRENCE THAT THE DESIGN INTENT HAS BEEN ACHIEVED.
3. THE CONTRACTORS SHALL BE FULLY AWARE OF THE OTHER INTERFACING PACKAGES AND SHALL HAVE DEEMED TO HAVE INCLUDED INTER-TRADE INTERFACES. THE INTERFACES IDENTIFIED IN THE DOCUMENTATION ARE TO INDICATE AN INTENT AND ARE NOT INTENDED TO BE EXHAUSTIVE. MAKE ALLOWANCES AS REQUIRED.

ISSUED FOR CONSTRUCTION

[illegible]

505695-0000-DRG-ST-1911

REFERENCES

SCALE :
1 : 1 (@ A1)

DATUM :
HORIZONTAL: PCG94
VERTICAL: AHD71

PTA ACCEPTANCE STAMP

DESIGNED	J.SPANO
BY	A.DAVISON

DRAWN	A.DAWSON
CHECKED	M.PEARCE

G.BENTLEY




Government of Western Australia
Public Transport Authority

DETAILED DESIGN FOR THE BELLEVUE DEPOT

HV TESTING FACILITY
STRUCTURAL

3D IMAGE - SHEET 2 OF 7 - OVERALL BUILDING

PTA Drawing No: 12-A-152-ST0291	REV : 0
---------------------------------	---------

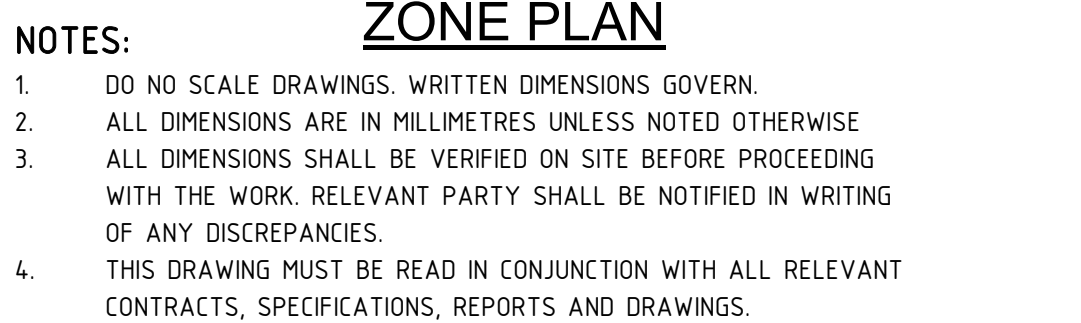

NOTES:

1. DO NO SCALE DRAWINGS. WRITTEN DIMENSIONS GOVERN.
2. ALL DIMENSIONS ARE IN MILLIMETRES UNLESS NOTED OTHERWISE
3. ALL DIMENSIONS SHALL BE VERIFIED ON SITE BEFORE PROCEEDING WITH THE WORK. RELEVANT PARTY SHALL BE NOTIFIED IN WRITING OF ANY DISCREPANCIES.
4. THIS DRAWING MUST BE READ IN CONJUNCTION WITH ALL RELEVANT CONTRACTS, SPECIFICATIONS, REPORTS AND DRAWINGS.

USE OF THESE DRAWINGS

1. THIS DRAWING SHALL BE READ IN CONJUNCTION WITH THE DISCIPLINE CONTRACT SPECIFICATION AND OTHER PROJECT DOCUMENTS.
2. DRAWINGS AND DESIGNS UNDERTAKEN BY A SHOP DETAILER SHALL BE PRESENTED TO THE PTA FOR REVIEW AND CONCURRENCE THAT THE DESIGN INTENT HAS BEEN ACHIEVED.
3. THE CONTRACTORS SHALL BE FULLY AWARE OF THE OTHER INTERFACING PACKAGES AND SHALL HAVE DEEMED TO HAVE INCLUDED INTER-TRADE INTERFACES. THE INTERFACES IDENTIFIED IN THE DOCUMENTATION ARE TO INDICATE AN INTENT AND ARE NOT INTENDED TO BE EXHAUSTIVE. MAKE ALLOWANCES AS REQUIRED.

ISSUED FOR CONSTRUCTION

[illegible]

505695-0000-DRG-ST-1912

REFERENCES

SCALE :
1 : 1 (@ A1)

DATUM :
HORIZONTAL: PCG94
VERTICAL: AHD71

PTA ACCEPTANCE STAMP

DESIGNED J.SPANO

DRAWN A.DAWSON

CHECKED M.PEARCE

APPROVED FOR ISSUE

G.BENTLEY

 Government of Western Australia
Public Transport Authority

DETAILED DESIGN FOR THE BELLEVUE DEPOT

HV TESTING FACILITY
STRUCTURAL


3D IMAGE - SHEET 3 OF 7 - OVERALL BUILDING

PTA Drawing No: 12-A-152-ST0292	REV : 0
---------------------------------	---------



NOTES:

1. DO NO SCALE DRAWINGS. WRITTEN DIMENSIONS GOVERN.
2. ALL DIMENSIONS ARE IN MILLIMETRES UNLESS NOTED OTHERWISE
3. ALL DIMENSIONS SHALL BE VERIFIED ON SITE BEFORE PROCEEDING WITH THE WORK. RELEVANT PARTY SHALL BE NOTIFIED IN WRITING OF ANY DISCREPANCIES.
4. THIS DRAWING MUST BE READ IN CONJUNCTION WITH ALL RELEVANT CONTRACTS, SPECIFICATIONS, REPORTS AND DRAWINGS.

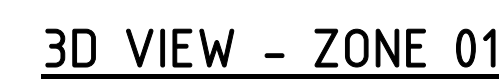

1. THIS DRAWING SHALL BE READ IN CONJUNCTION WITH THE DISCIPLINE CONTRACT SPECIFICATION AND OTHER PROJECT DOCUMENTS.
2. DRAWINGS AND DESIGNS UNDERTAKEN BY A SHOP DETAILER SHALL BE PRESENTED TO THE PTA FOR REVIEW AND CONCURRENCE THAT THE DESIGN INTENT HAS BEEN ACHIEVED.
3. THE CONTRACTORS SHALL BE FULLY AWARE OF THE OTHER INTERFACING PACKAGES AND SHALL HAVE DEEMED TO HAVE INCLUDED INTER-TRADE INTERFACES. THE INTERFACES IDENTIFIED IN THE DOCUMENTATION ARE TO INDICATE AN INTENT AND ARE NOT INTENDED TO BE EXHAUSTIVE. MAKE ALLOWANCES AS REQUIRED.

 Government of Western Australia
Public Transport Authority

DETAILED DESIGN FOR THE BELLEVUE DEPOT

PTA Drawing No: 12-A-152-ST0293

REV : 0

aurecon
www.aurecongroup.com

505695-0000-DRG-ST-1913

SCALE :	1 : 1	(@ A1)
---------	-------	--------

DATUM :
HORIZONTAL: PCG94
VERTICAL: AHD71


PTA ACCEPTANCE STAMP

DESIGNED	J.SPANO
DRAWN	A.BALOGH

DRAWN	A.DAWSON
CHECKED	M.PEARCE
APPROVED FOR ISSUE	

APPROVED FOR ISSUE

G.BENTLEY

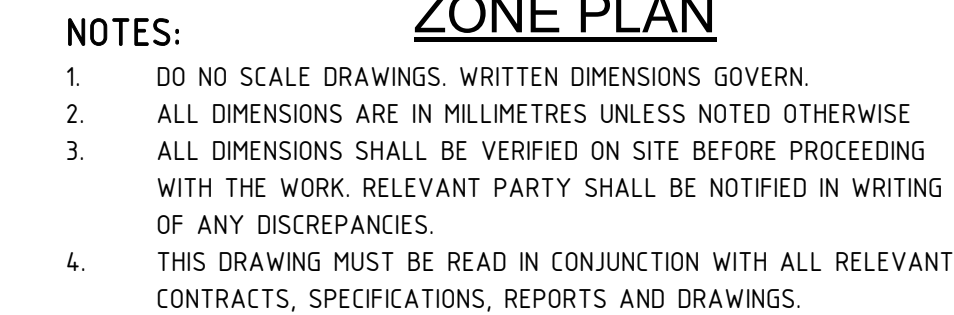

NOTES:

1. DO NO SCALE DRAWINGS. WRITTEN DIMENSIONS GOVERN.
2. ALL DIMENSIONS ARE IN MILLIMETRES UNLESS NOTED OTHERWISE.
3. ALL DIMENSIONS SHALL BE VERIFIED ON SITE BEFORE PROCEEDING WITH THE WORK. RELEVANT PARTY SHALL BE NOTIFIED IN WRITING OF ANY DISCREPANCIES.
4. THIS DRAWING MUST BE READ IN CONJUNCTION WITH ALL RELEVANT CONTRACTS, SPECIFICATIONS, REPORTS AND DRAWINGS.

1. THIS DRAWING SHALL BE READ IN CONJUNCTION WITH THE DISCIPLINE CONTRACT SPECIFICATION AND OTHER PROJECT DOCUMENTS.
2. DRAWINGS AND DESIGNS UNDERTAKEN BY A SHOP DETAILER SHALL BE PRESENTED TO THE PTA FOR REVIEW AND CONCURRENCE THAT THE DESIGN INTENT HAS BEEN ACHIEVED.
3. THE CONTRACTORS SHALL BE FULLY AWARE OF THE OTHER INTERFACING PACKAGES AND SHALL HAVE DEEMED TO HAVE INCLUDED INTER-TRADE INTERFACES. THE IDENTIFICATIONS IN THE DOCUMENTATION ARE TO INDICATE AN INTENT AND ARE NOT INTENDED TO BE EXHAUSTIVE. MAKE ALLOWANCES AS REQUIRED.



1. THIS DRAWING SHALL BE READ IN CONJUNCTION WITH THE DISCIPLINE CONTRACT SPECIFICATION AND OTHER PROJECT DOCUMENTS.
2. INFORMATION SHOWN ON THIS DRAWING SHALL NOT BE USED FOR CONSTRUCTION PURPOSES. THE DRAWINGS AND SPECIFICATIONS DO NOT PURPORT TO SHOW ALL MINOR ITEMS OF EQUIPMENT AND ACCESSORIES WHICH MAY BE NECESSARY. THESE MINOR ITEMS SHALL BE PROVIDED TO FORM COMPLETE AND FULLY OPERATIONAL SYSTEMS.
3. THE CONTRACTORS SHALL BE FULLY AWARE OF THE OTHER INTERFACING PACKAGES AND SHALL HAVE DEEMED TO HAVE INCLUDED INTER-TRADE INTERFACES. THE INTERFACES IDENTIFIED IN THE DOCUMENTATION ARE TO INDICATE AN INTENT AND ARE NOT INTENDED TO BE EXHAUSTIVE. MAKE ALLOWANCES AS REQUIRED.


 Government of Western Australia
Public Transport Authority

PTA Drawing No: 12-A-152-ST0294	REV : 0
---------------------------------	---------

aurecon
www.aurecongroup.com

PTA ACCEPTANCE STAMP

DESIGNED	J.SPANO
DRAWN	A.DAWSON
CHECKED	M.PEARCE
APPROVED FOR ISSUE	
G.BENTLEY	
DATE	

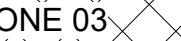

NOTES:

1. DO NO SCALE DRAWINGS. WRITTEN DIMENSIONS GOVERN.
2. ALL DIMENSIONS ARE IN MILLIMETRES UNLESS NOTED OTHERWISE
3. ALL DIMENSIONS SHALL BE VERIFIED ON SITE BEFORE PROCEEDING WITH THE WORK. RELEVANT PARTY SHALL BE NOTIFIED IN WRITING OF ANY DISCREPANCIES.
4. THIS DRAWING MUST BE READ IN CONJUNCTION WITH ALL RELEVANT CONTRACTS, SPECIFICATIONS, REPORTS AND DRAWINGS.



1. THIS DRAWING SHALL BE READ IN CONJUNCTION WITH THE DISCIPLINE CONTRACT SPECIFICATION AND OTHER PROJECT DOCUMENTS.
2. DRAWINGS AND DESIGNS UNDERTAKEN BY A SHOP DETAILER SHALL BE PRESENTED TO THE PTA FOR REVIEW AND CONCURRENCE THAT THE DESIGN INTENT HAS BEEN ACHIEVED.
3. THE CONTRACTORS SHALL BE FULLY AWARE OF THE OTHER INTERFACING PACKAGES AND SHALL HAVE DEEMED TO HAVE INCLUDED INTER-TRADE INTERFACES. THE INTERFACES IDENTIFIED IN THE DOCUMENTATION ARE TO INDICATE AN INTENT AND NOT INTENDED TO BE EXHAUSTIVE. MAKE ALLOWANCES AS REQUIRED.

 Government of Western Australia
Public Transport Authority

DETAILED DESIGN FOR THE BELLEVUE DEPOT

HV TESTING FACILITY

STRUCTURAL

3D IMAGE - SHEET 6 OF 7 - ZONE 03

PTA Drawing No: 12-A-152-ST0295

REV : 0

[illegible]

www.aurecongroup.com

505695-0000-DRG-ST-1914

REFERENCES

SCALE :
1 : 1 (@ A1)

DATUM :

HORIZONTAL: PCG94
VERTICAL: AHD71

PTA ACCEPTANCE STAMP

DESIGNED J.SPANO


DRAWN A.DAWSON

CHECKED M.PEARCE

APPROVED FOR ISSUE

G.BENTLEY

DATE _____

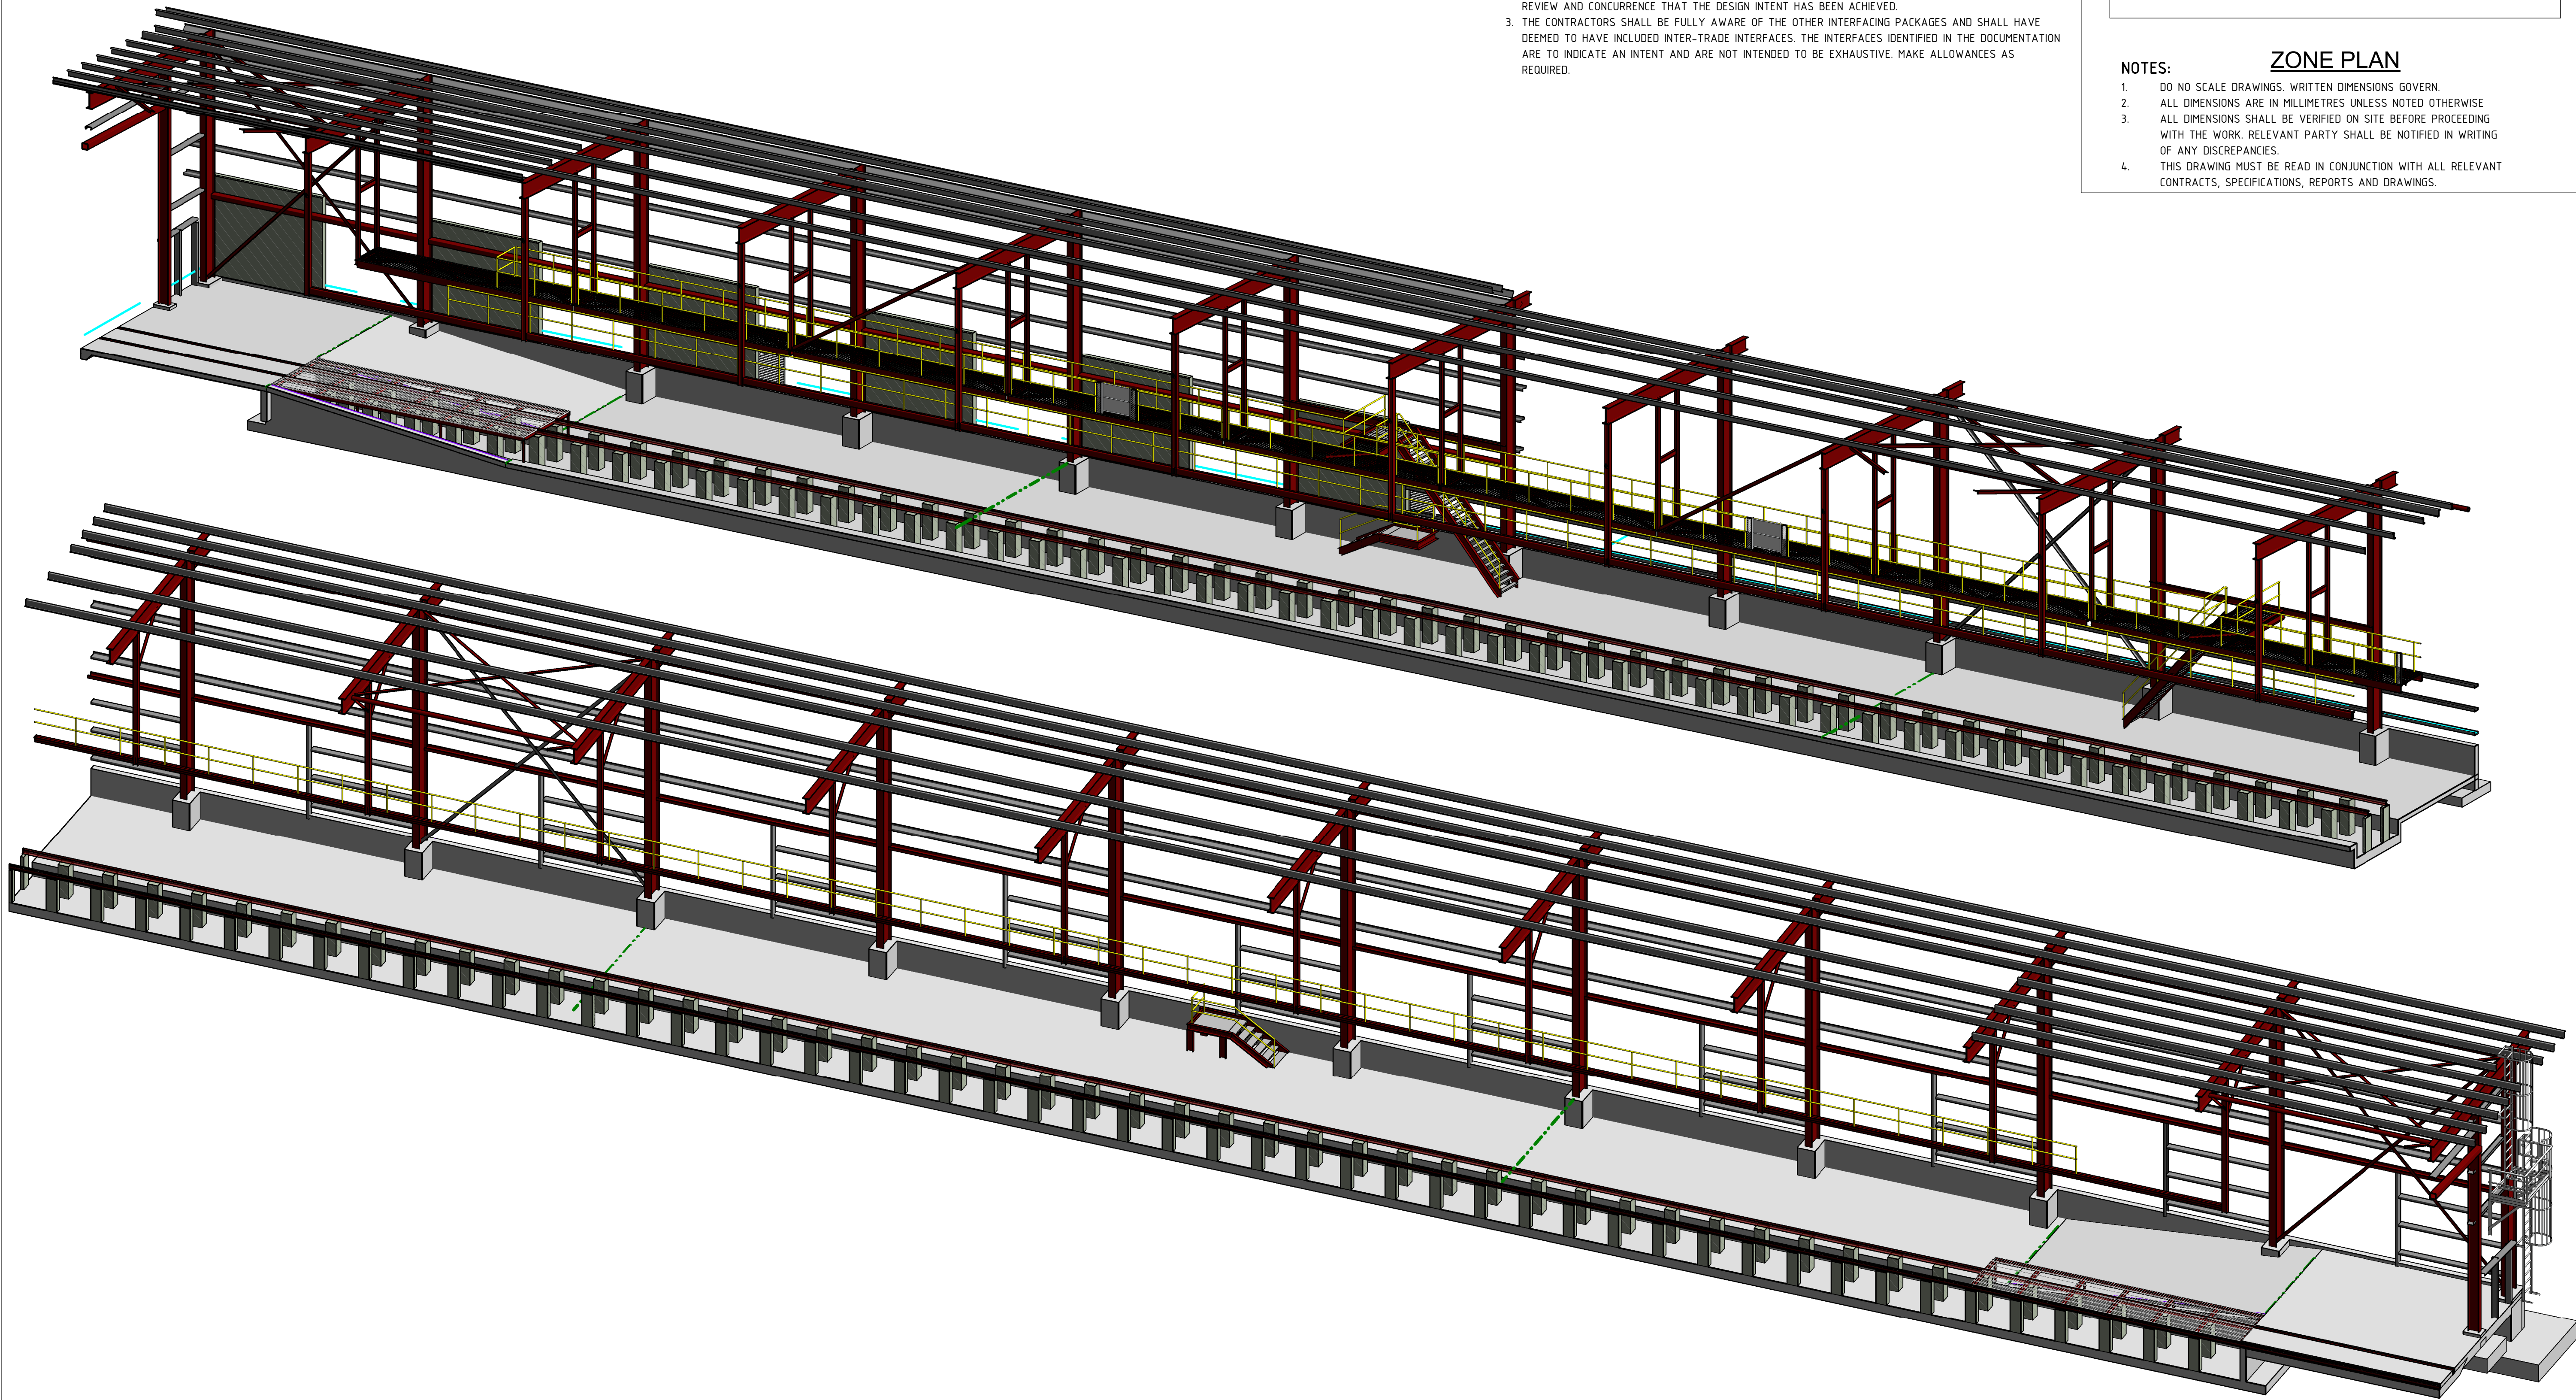

- USE OF THESE DRAWINGS**
1. THIS DRAWING SHALL BE READ IN CONJUNCTION WITH THE DISCIPLINE CONTRACT SPECIFICATION AND OTHER PROJECT DOCUMENTS.
 2. DRAWINGS AND DESIGNS UNDERTAKEN BY A SHOP DETAILER SHALL BE PRESENTED TO THE PTA FOR REVIEW AND CONCURRENCE THAT THE DESIGN INTENT HAS BEEN ACHIEVED.
 3. THE CONTRACTORS SHALL BE FULLY AWARE OF THE OTHER INTERFACING PACKAGES AND SHALL HAVE DEEMED TO HAVE INCLUDED INTER-TRADE INTERFACES. THE INTERFACES IDENTIFIED IN THE DOCUMENTATION ARE TO INDICATE AN INTENT AND ARE NOT INTENDED TO BE EXHAUSTIVE. MAKE ALLOWANCES AS REQUIRED.

- NOTES:**
1. DO NO SCALE DRAWINGS. WRITTEN DIMENSIONS GOVERN.
 2. ALL DIMENSIONS ARE IN MILLIMETRES UNLESS NOTED OTHERWISE
 3. ALL DIMENSIONS SHALL BE VERIFIED ON SITE BEFORE PROCEEDING WITH THE WORK. RELEVANT PARTY SHALL BE NOTIFIED IN WRITING OF ANY DISCREPANCIES.
 4. THIS DRAWING MUST BE READ IN CONJUNCTION WITH ALL RELEVANT CONTRACTS, SPECIFICATIONS, REPORTS AND DRAWINGS.

ZONE PLAN

0	01.10.19	ISSUED FOR CONSTRUCTION	J.S.	A.C.D.	M.P.	G.B.
REV	DATE	AMENDMENT	DSN	DRN	CHKD	APP
ORIG SIZE	A1	SCALE 1:100 AT A1	This document must not be copied without PTA's written permission, and the contents thereof must not be imparted to a third party nor be used for any unauthorised purpose.			

aurecon
www.aurecongroup.com

505695-0000-DRG-ST-1915

REFERENCES

SCALE :
1 : 1 (@ A1)
DATUM :
HORIZONTAL: PC694
VERTICAL: AHD71
PTA ACCEPTANCE STAMP

DESIGNED J.SPANO
DRAWN A.DAWSON
CHECKED M.PEARCE
APPROVED FOR ISSUE
G.BENTLEY
DATE

ISSUED FOR CONSTRUCTION

DETAILED DESIGN FOR THE BELLEVUE DEPOT

HV TESTING FACILITY
STRUCTURAL
3D IMAGE - SHEET 7 OF 7 - SECTIONS
PTA Drawing No: 12-A-152-ST0296

REV : 0