
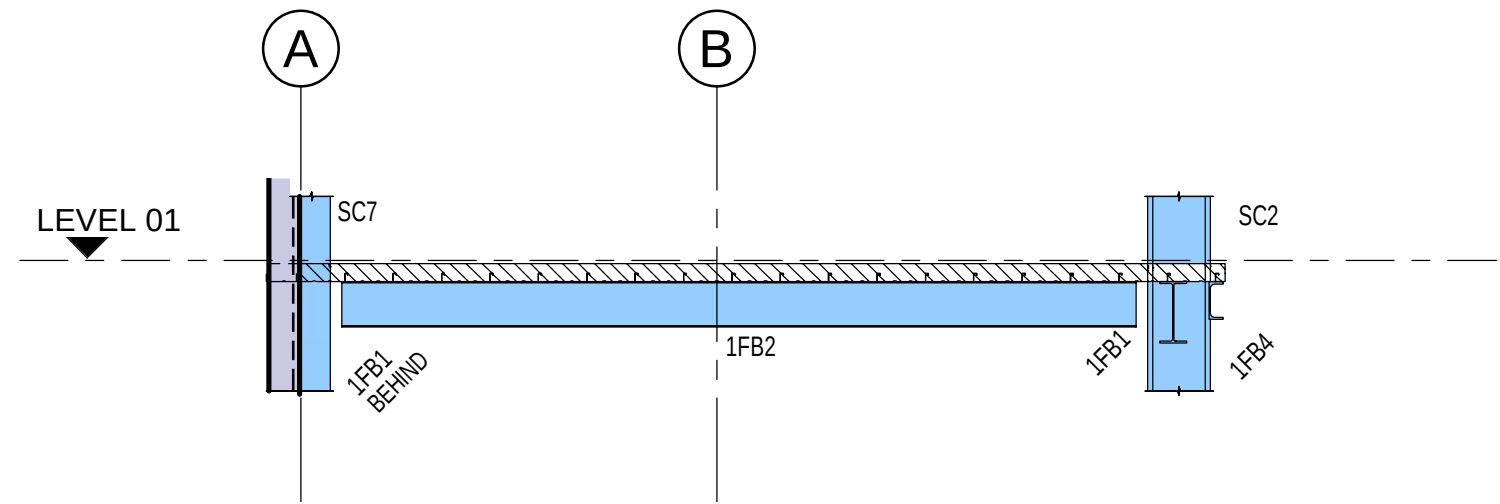


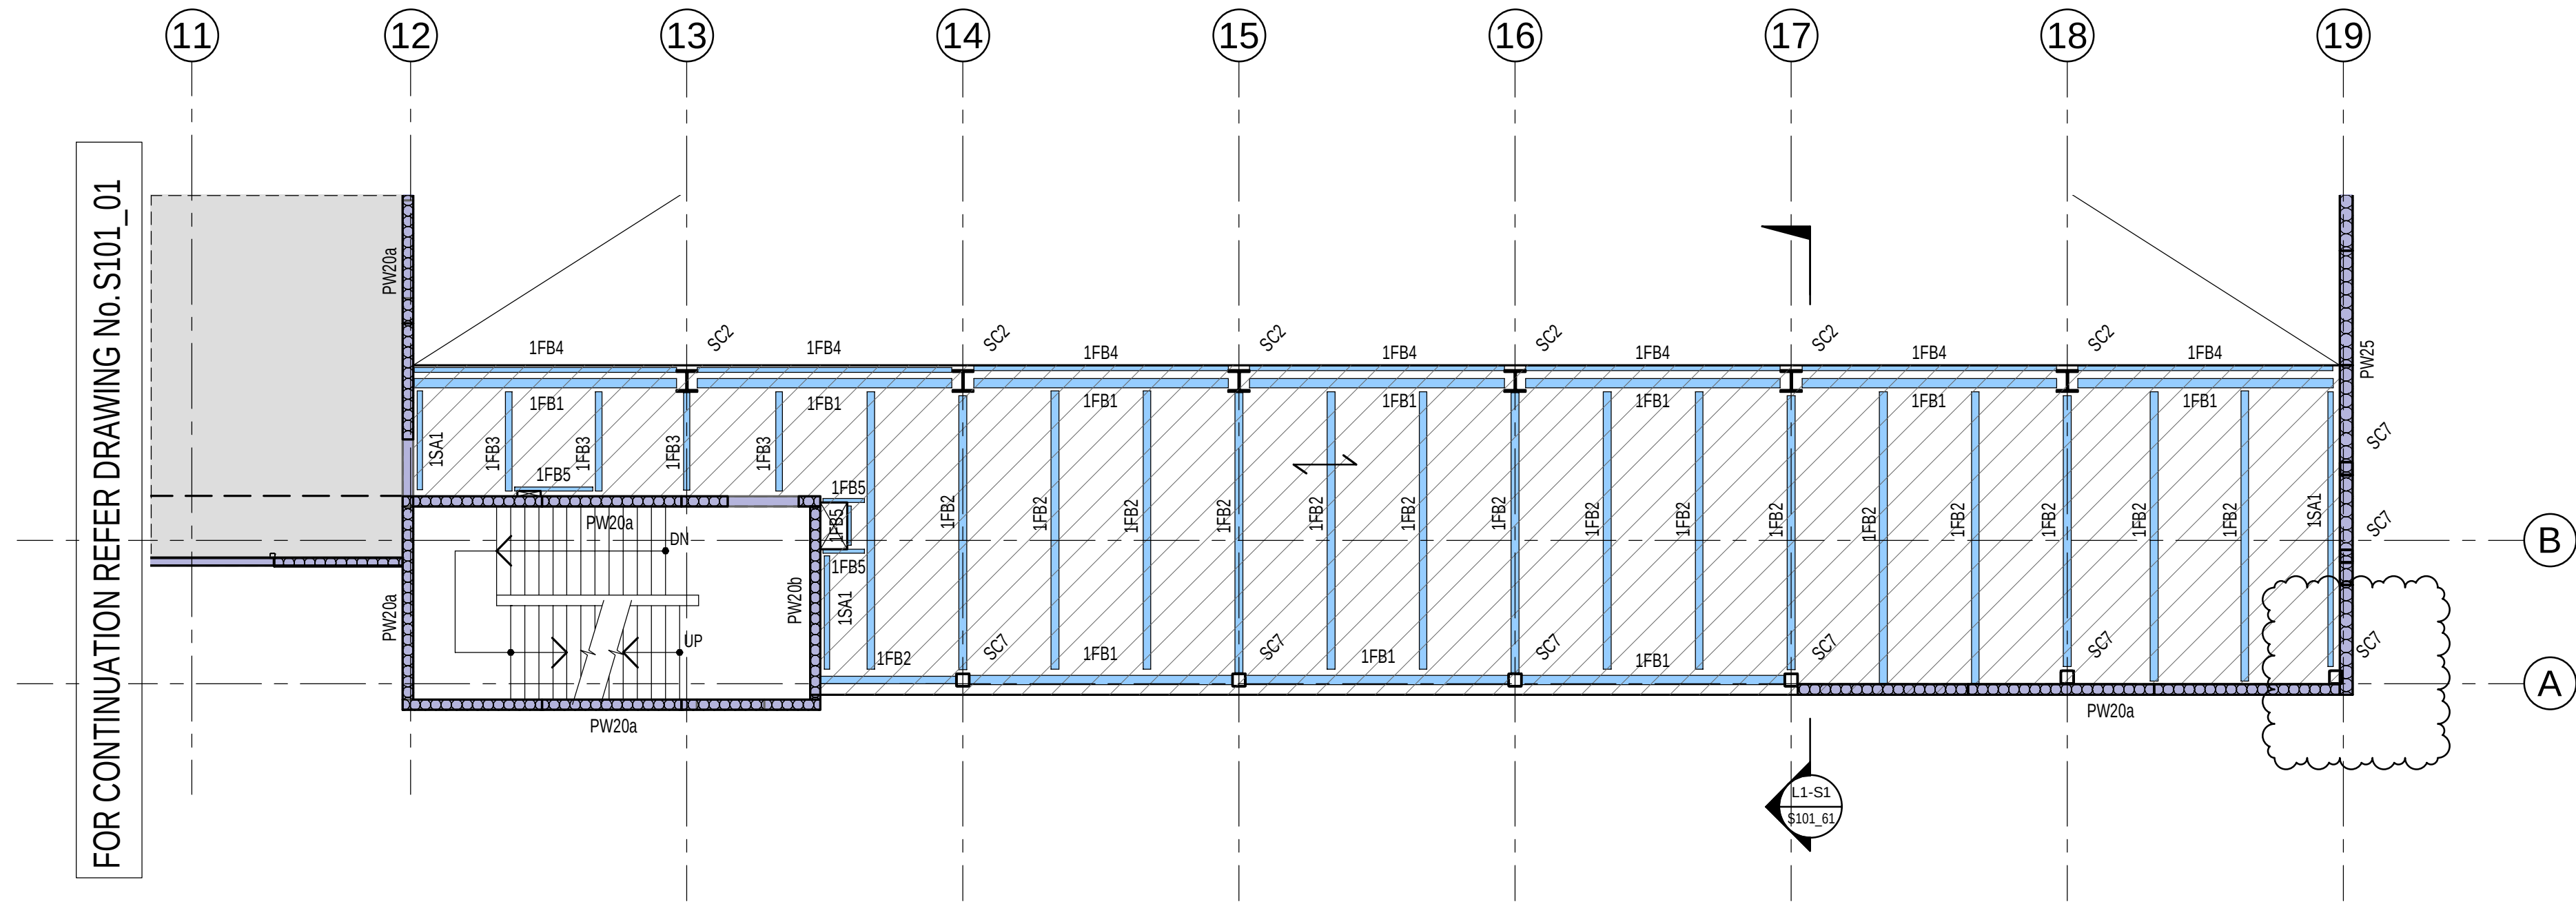

LEVEL 01 STEEL FRAMING PART PLAN

SCALE 1 : 100

STRUCTURAL SIZES:


REFER TO CONCRETE OUTLINE PLAN UNLESS NOTED OTHERWISE

CONCRETE GRADE:

ALL FLOOR ELEMENTS:

FC = 40 MPa (48MPa MIN. AT 90 DAYS)

SLAB THICKNESS:

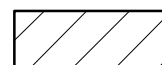

DENOTES 120mm THICK COMPOSITE RC SLAB ON CONTINUOUS 1.0mm CONDEK METAL TRAY FORMWORK. N12-300 BARS TOP EACH WAY N12-300 BARS BOTTOM ALONG CONDEK FOR ENDSPANS. 30 COVER TYPICAL.



DENOTES SPAN DIRECTION OF CONDEK TRAY

DESIGN LOADING:


REFER DESIGN DEVELOPMENT REPORT

STEEL FLOOR FRAMING SCHEDULE - LEVEL 01			
MARK	STRUCTURAL SIZE	SHEAR STUDS	COMMENTS
1FB1	410UB33.7	1 ROW 19 DIA SHEAR STUDS @ 450 MAX CTS.	STEEL PRIMARY FLOOR BEAM
1FB2	310UB32.0	1 ROW 19 DIA SHEAR STUDS @ 350 MAX CTS.	STEEL FLOOR BEAM
1FB3	250UB25.7	1 ROW 19 DIA SHEAR STUDS @ 350 MAX CTS.	STEEL FLOOR BEAM
1FB4	20UPFC	1 ROW 19 DIA SHEAR STUDS @ 450 MAX CTS.	STEEL BONDEK FLOOR SUPPORT
1FB5	150UPFC		STEEL TRIMMER FLOOR BEAM
1SA1	150x100x10 UA		STEEL SHELF ANGLE (M16 CHEMSET ANCHORS @ 600 CTS)

STEEL COLUMN SCHEDULE		
MARK	STRUCTURAL SIZE	COMMENTS
SC1	400MC270	STEEL COLUMN
SC2	400MC270	STEEL COLUMN
SC7	250x250x8.0 SHS	STEEL COLUMN (SYM)

NOTE:

- ALL EXPOSED STEELWORK TO BE HOT DIP GALVANISED.
- ALL STEELWORK TO BE FIRE PROTECTED TO ACHIEVE F.R.L AS REQUIRED BY THE BUILDING SURVEYOR.

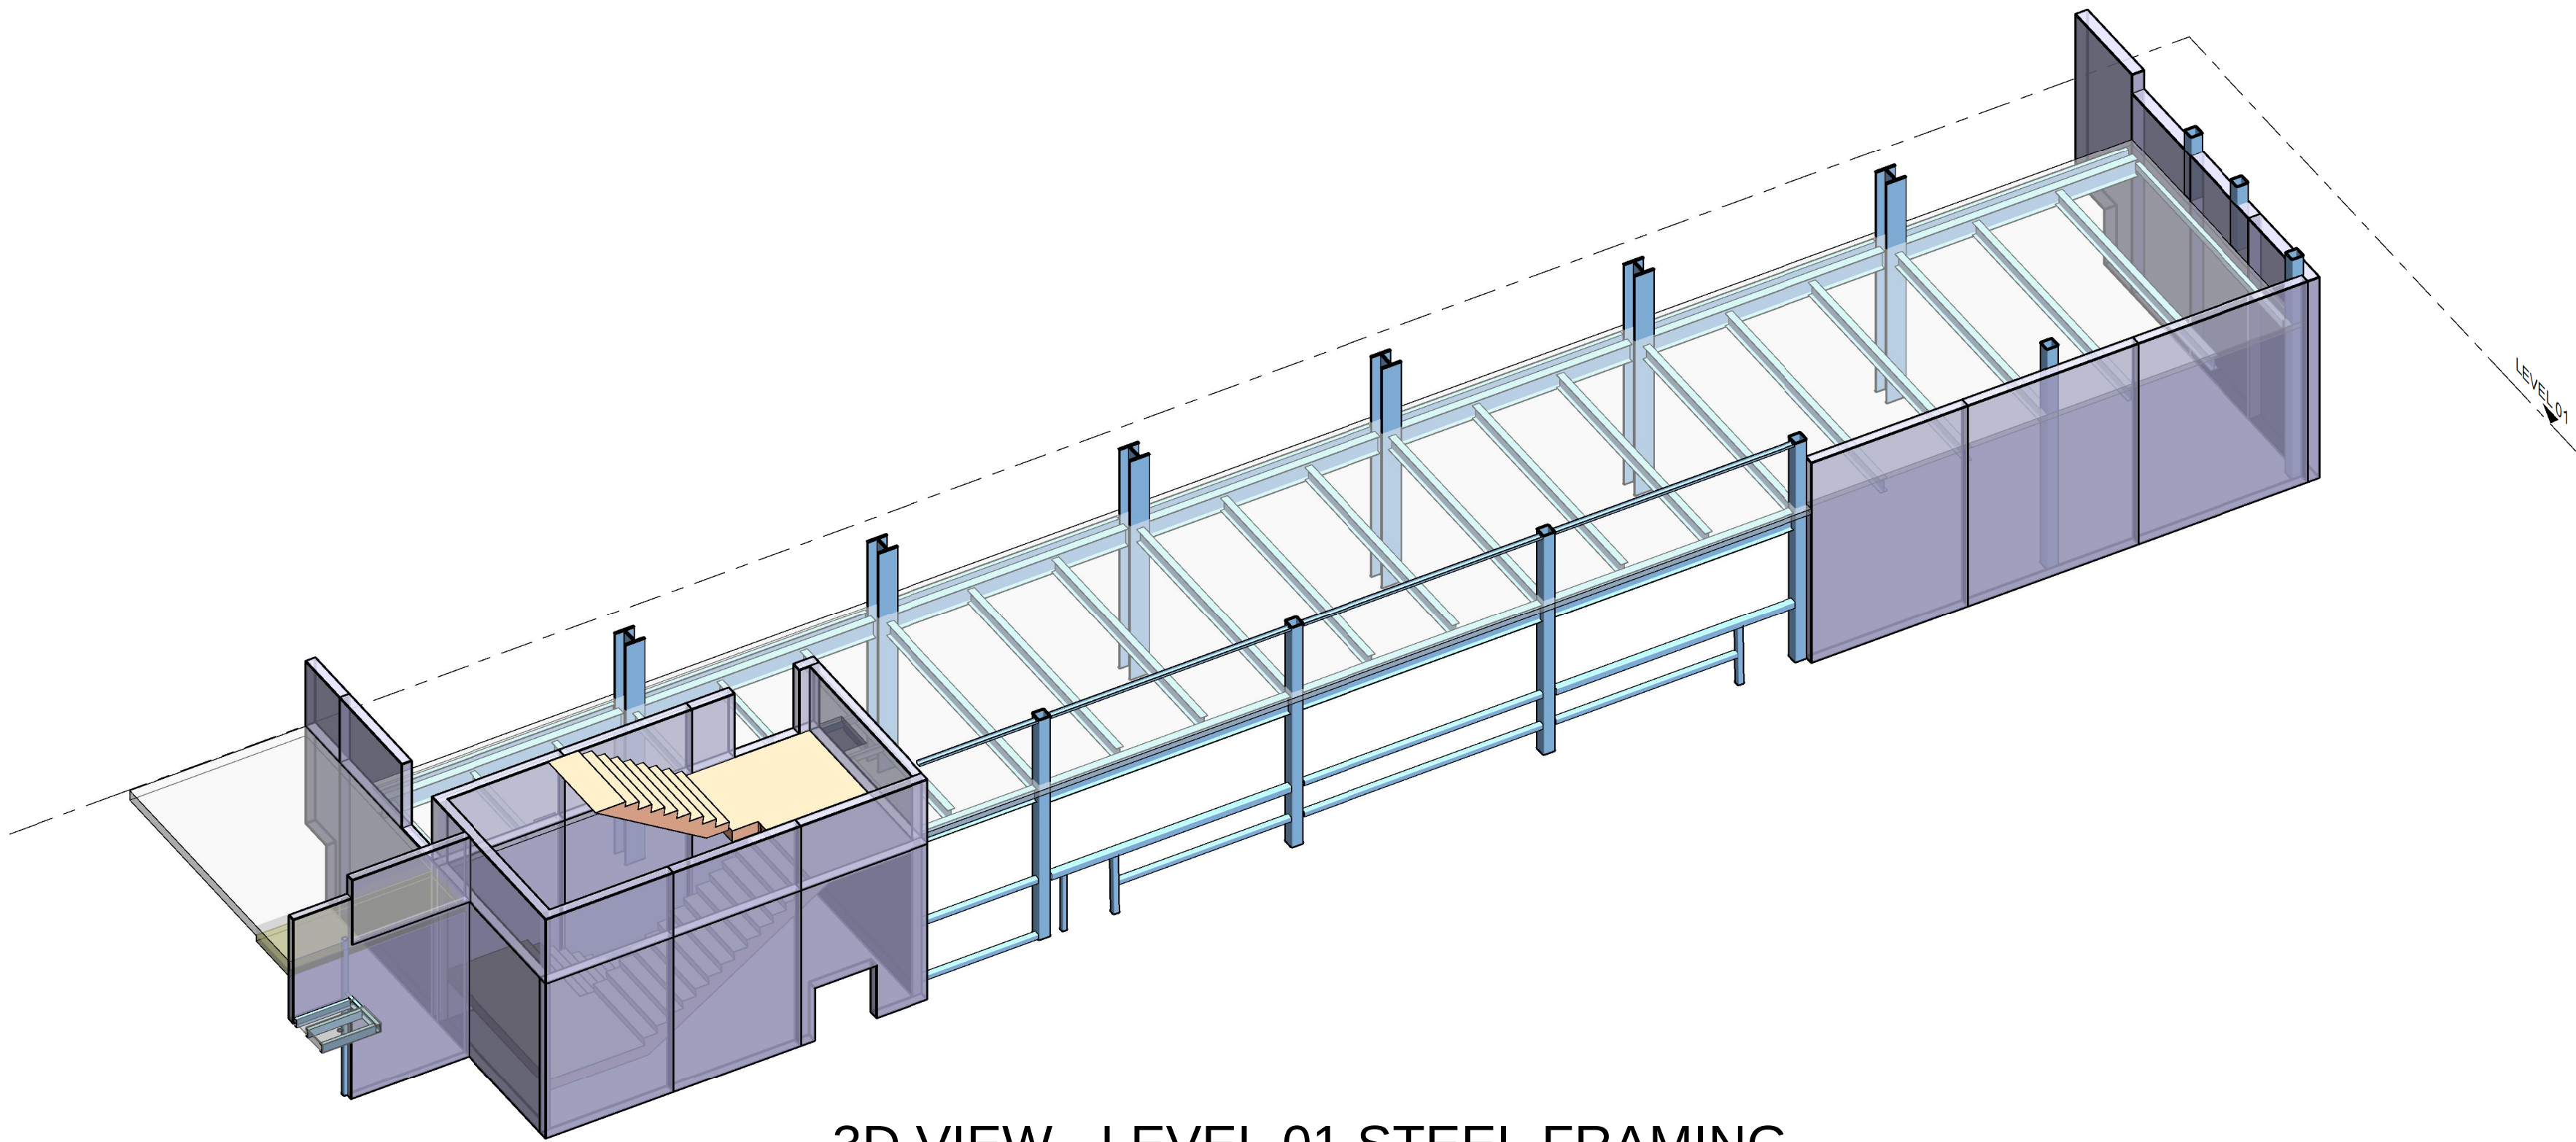

3D VIEW - LEVEL 01 STEEL FRAMING

T1	TENDER ADDENDUM (AS CLOUDED)	03.09.2019	SB
T0	ISSUED FOR TENDER	31.07.2019	SB
1	ISSUED FOR INFORMATION	29.07.2019	SB
ISSUE	REVISION	DATE	INITIAL



TENDER	
NOT FOR CONSTRUCTION	
© WSP Australia Pty Ltd. All rights reserved. These drawings, plans and specifications and the copyright therein are the property of WSP Australia Pty Ltd. and must not be used, reproduced or copied fully or in part without the written permission of WSP Australia Pty Ltd.	

McKINNON SECONDARY COLLEGE	
LEVEL 01 STEEL FRAMING PLAN	

STRUCTURAL DRAWING			
Designed: G.R.	Approved: Approver	North	
Drawn: J.Mac	Project Engineer/Director: Date:	Issue	
Scale:	Project No: Drawing No:	T1	
Date: 03.2019	PS112599 S101_61		