



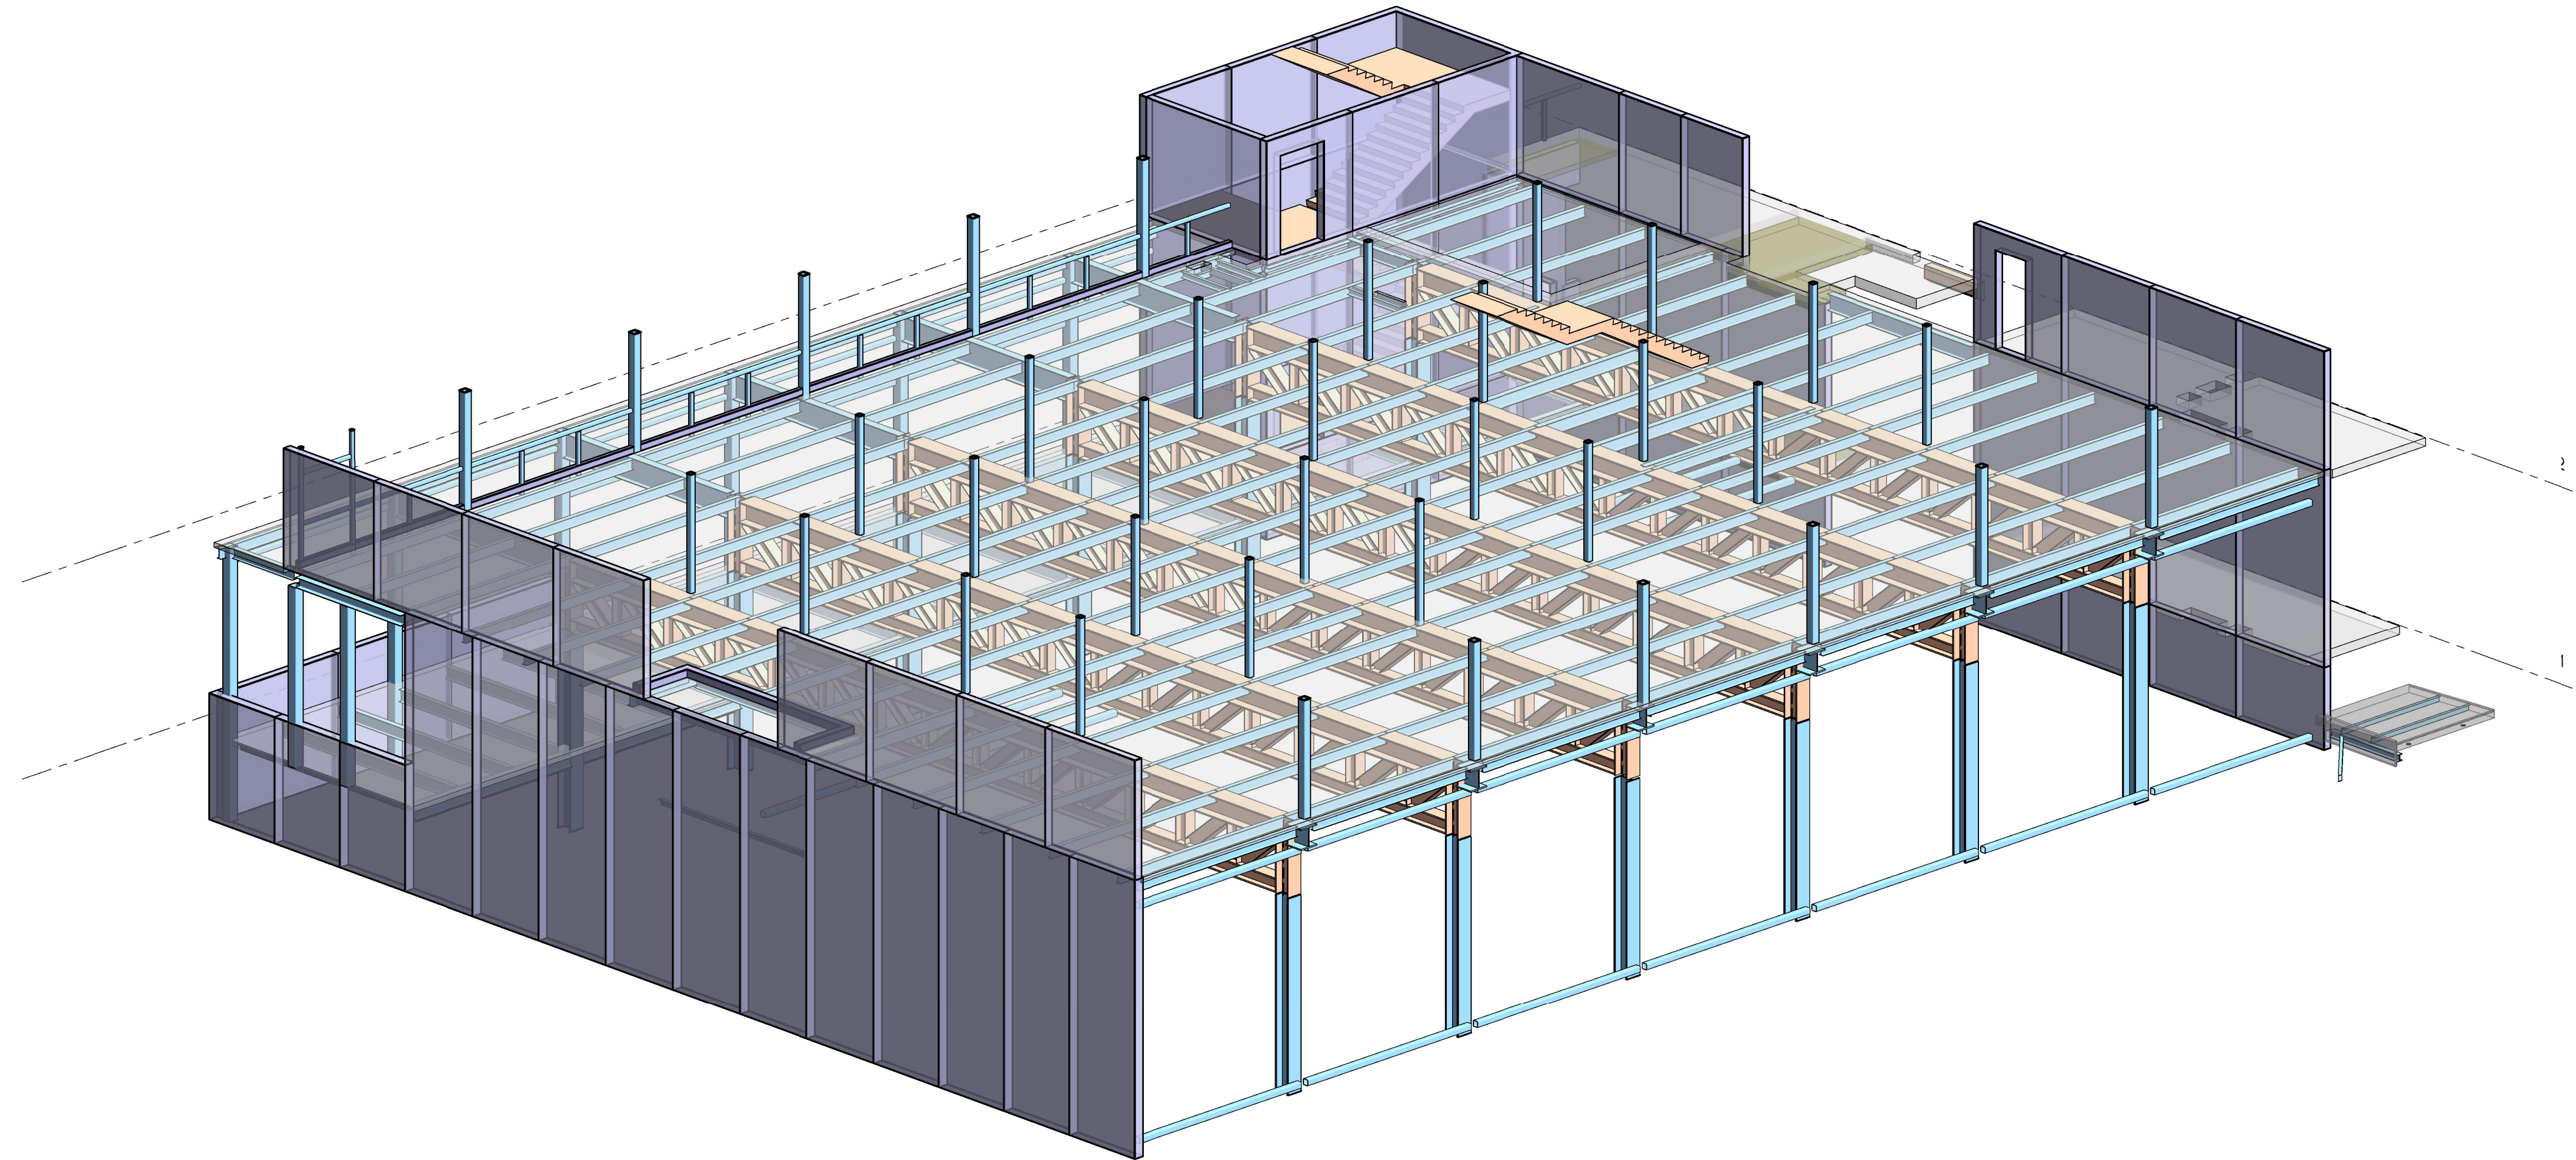

SCALE



1800mm OVERALL MAX DEPTH
60mm PRECAMBER

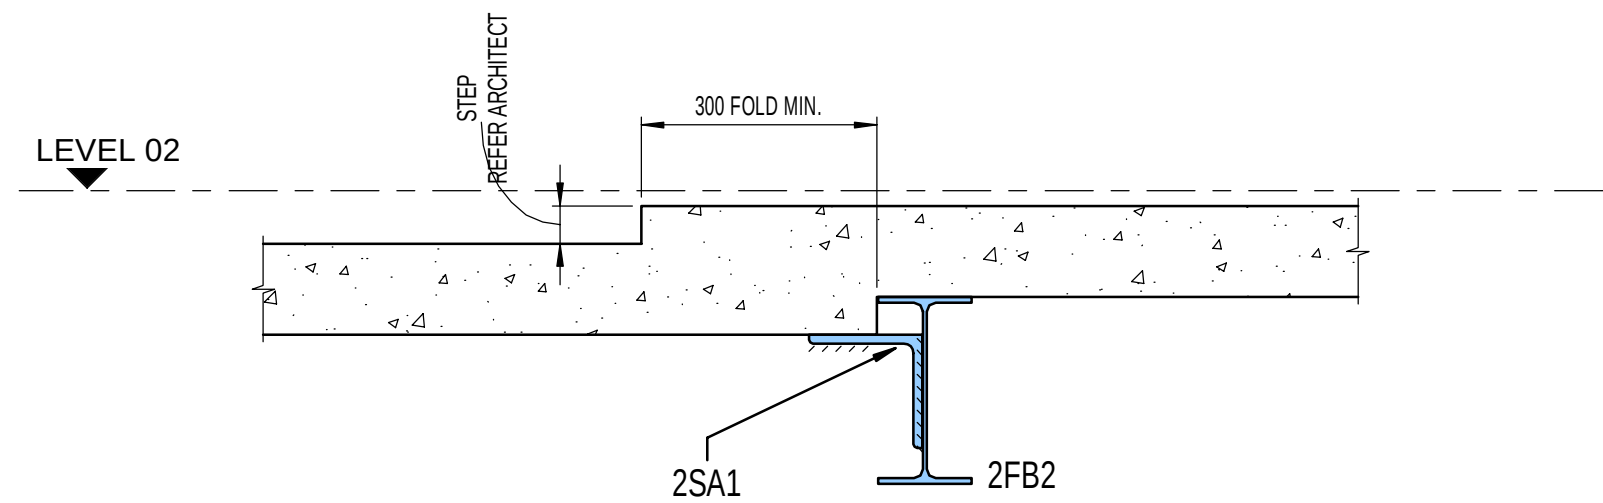

SECTION 1:10 L2-S2 S102_61

SCALE



Melbourne, VIC, Australia
www.wsp.com

NOT FOR CONSTRUCTION

LEVEL 02 STEEL FRAMING PLAN

Designed: G.R.	Approved: Approve
----------------	-------------------

Drawn: J.Mac	Project Engineer/Director:	Date:	North
Scale:	Project No:	Drawing No:	Issue
Date: 03.2019	PS112599	S102_61	T2

North

T2